# 点位定位尺寸图 说明 Setting-out notes

## Rev C（2026-10-14）：按模型 v47 —— 洗衣房后门挪位 / 无门洞口、冰箱挪位、电器 FCU 集中（洗衣房 + 楼梯下柜内）、洗衣房白色面板

- 本版所有点位的位置、高度、回路、备注都直接取自已完成的墙面立面图（业主逐面确认），立面图是准，本图是全屋汇总。
- 每个点位在表里都写了「立面图号」（W1-xx-x 一层 / W2-xx-x 二层）：施工时按那张立面图上的尺寸放线。
- 墙面名称按「站在房间里看这面墙」；水平尺寸从左端量到底盒中心，同时给到右端的距离，两数之和 = 墙净长，可核对。
- 高度：从本房间完成地面量到底盒中心；天花灯给出到四面墙（完成面）的距离。
- 同一编号可能在不同房间各有一个（如地暖温控 TH、智能马桶开关 SM / ST）：以「房间 + 编号」区分。
- 给排水出口位置见给排水施工图（立面图只画了靠近电气点的几个：SH1、FT、户外台盆 OW / OD）。

**图例**

- 插座
- 开关
- 专用 / FCU / 新增
- 灯
- 烟感
- 给排水点

## 高度标准（底盒中心，离本房间完成地面；个别点以立面图为准）

| 项 | 高度 mm | 说明 |
|---|---|---|
| 开关 | 1200 | 主卫 / 主卧套间部分开关 1500（主卧套间 Rev L）；卫生间排风扇开关 1800 |
| 一般插座 | 450 | 英国规格（业主 2026-10-08） |
| 厨房台面插座 | 1200 | 台面（900，Wren 橱柜图 S8097782/1）上方 300（业主 2026-10-09） |
| 专用插座（在柜内 / 机器后） | 300–450 / 1900 | 洗碗机 C38 h450、灶 / 烤箱 C39 h300、洗衣机 / 烘干机 C12 h450、烟机 C40 在烟机柜内 h1900；按管道 / 电器调整 |
| 电器开关 FCU（单联 fused switch） | 1200 | 洗衣房锅炉下 4 个 FU1–FU4（洗衣机 / 烘干机 / 锅炉 / 地暖电子控制，白色）；楼梯下柜内 4 个 FD / FO1–FO3（洗碗机 / 烤箱 / 灶 / 烟机，白色）；二层卫生间 SM / ST 不变 |
| 户外插座 / 户外壁灯 | 600 / 2000 | 户外插座 IP66 带盖（后院 C41 已取消，Rev C）；后院 B 墙壁灯 h2000；L08 挪到洗衣房后门左边 |
| EV 充电桩 | 1050 | 前门凹位北侧墙（前院 Rev B 预留位） |

## 依据的立面图（全部已完成）

- 27PR_墙面立面_后院_RevD_后门挪位_台盆.pdf
- 27PR_墙面立面_前院_RevB_充电桩挪北侧.pdf
- 27PR_墙面立面_厨房区_RevC_洗衣房后门_冰箱_FCU.pdf
- 27PR_墙面立面_主客厅区_RevI_楼梯下FCU.pdf
- 27PR_墙面立面_二楼走廊_RevH_S12中途开关.pdf
- 27PR_墙面立面_后书房_RevG_C16挪后墙.pdf
- 27PR_墙面立面_中间书房_RevD_天花2700.pdf
- 27PR_墙面立面_次卧_RevP_毛巾架出线_床头650.pdf
- 27PR_墙面立面_主卧套间_RevM_温控开关挪位.pdf
- 27PR_墙面立面_副客厅_RevH_加地暖温控.pdf

## 与 Rev A 相比取消 / 合并的点位


- 一层 C06：取消：原热水器旁插座，改为洗衣房锅炉下 4 个单联 fused switch FU1–FU4（模型 v47，业主 2026-10-14）
- 一层 C26：半岛台柜内插座（与 C23 同一线，h800，白色；业主 2026-10-14），只在平面（不在墙面）
- 一层 L41：围栏地灯取消，改户外灯带出线 L40（后院 Rev B）

| | |
|---|---|
| 项目 Project | 27PR 住宅改造 · 27 Penrith Road |
| 图名 Title | 点位定位尺寸图 说明 Setting-out notes |
| 图号 Sheet | SO-00 比例 — @A3 |
| 专业 Discipline | 电气定位 Setting out |
| 版次 Rev | C · 2026-10-14 · 施工图（待持证电工 / 水工复核） |

# 一层点位定位总平面 Setting-out plan

0 — 2 m

→ 后花园 Rear

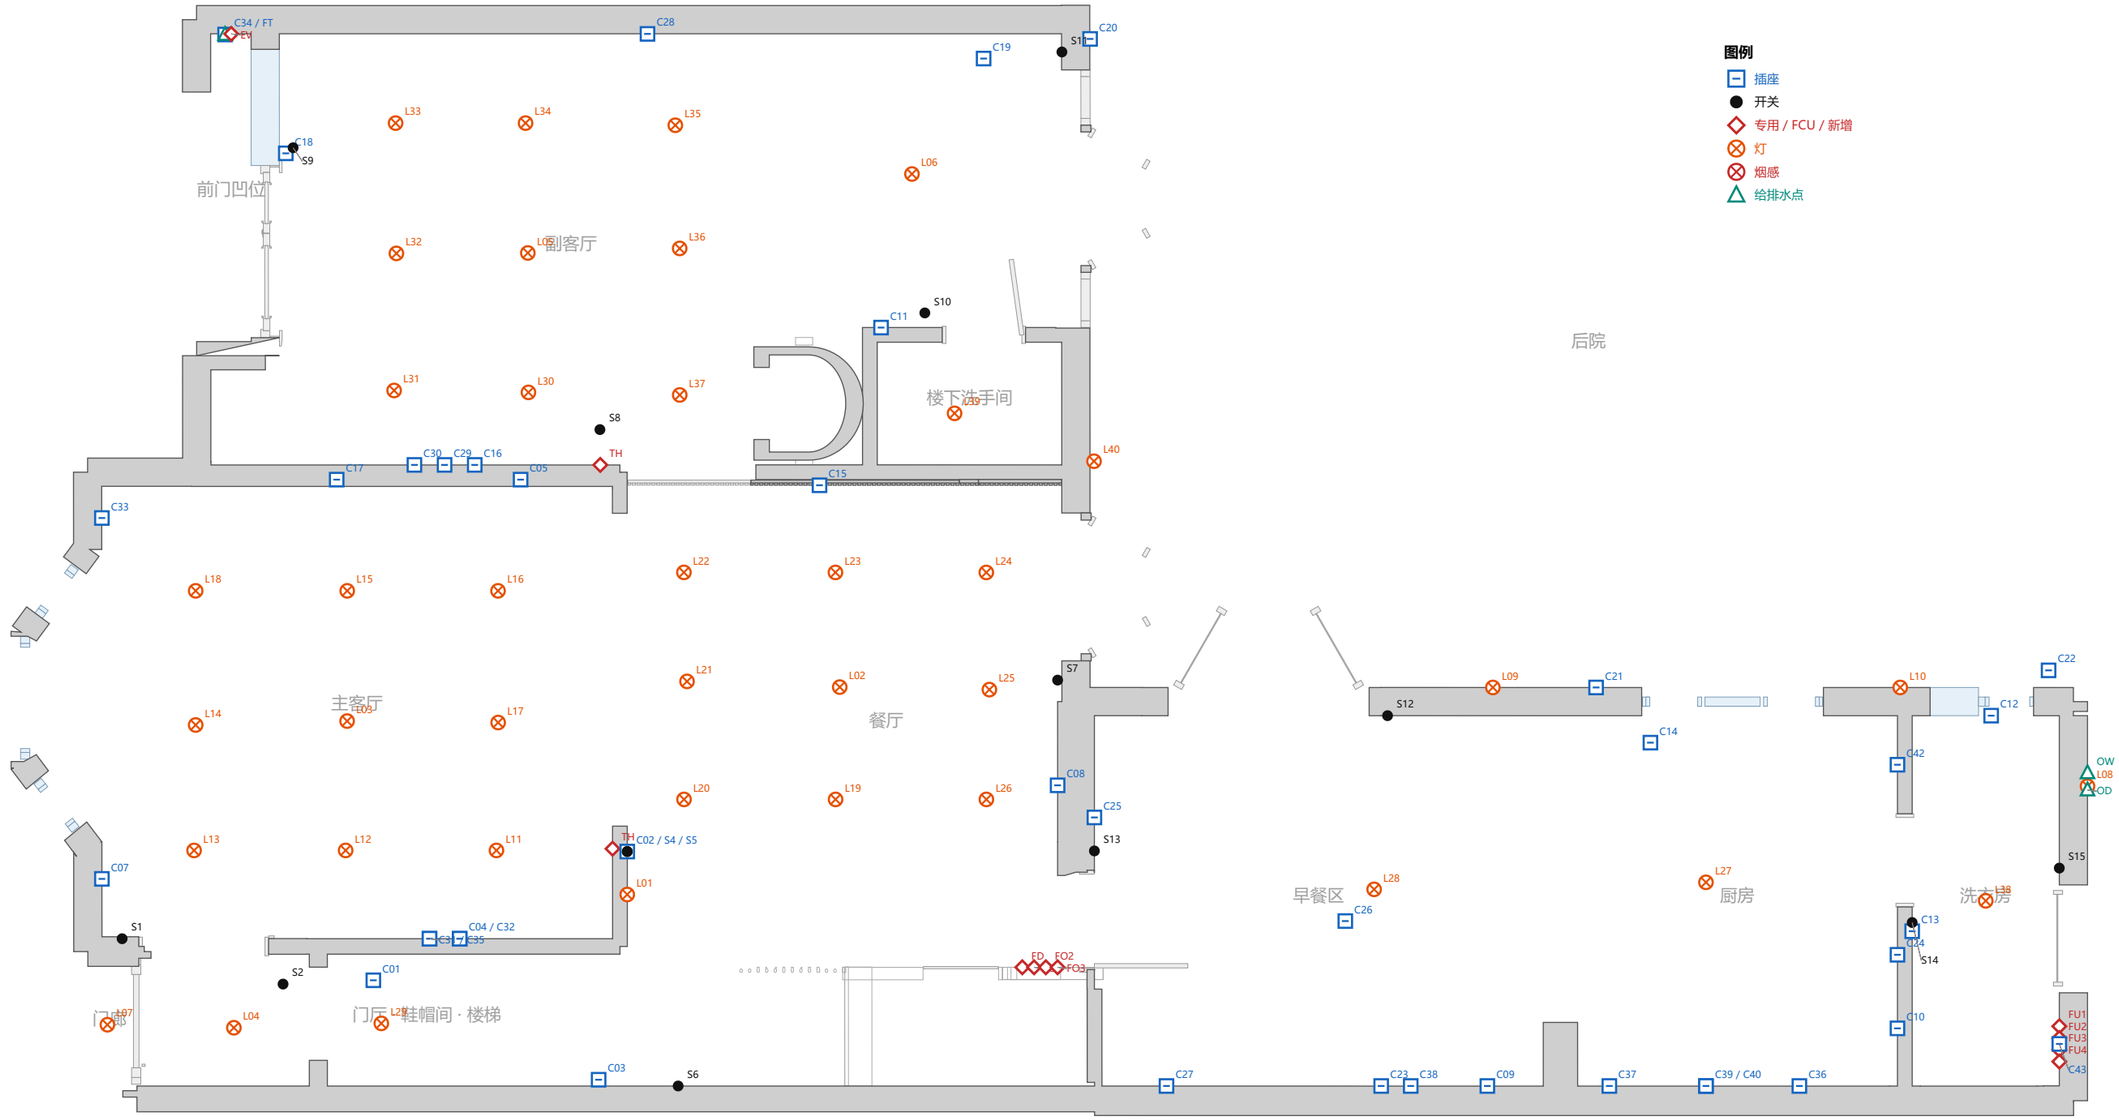


**说明 Notes**


1. Rev B：点位全部按已完成的墙面立面图（业主 2026-10-09 确认）。Rev C（2026-10-14）：厨房区 Rev C / 后院 Rev D / 主客厅区 Rev I（模型 v47）；洗衣房开关插座白色；柜内插座 C26 / C38 / C39 / C40 白色；C01 / C02 / C38 改双位。
2. 平面上的位置 = 墙面位置；放线尺寸、高度见定位表里的立面图号（W1- / W2-），哪个区域看哪个立面图文件见 SO-03 / SO-04。
3. 给排水出口见给排水施工图。

| | |
|---|---|
| 项目 Project | 27PR 住宅改造 · 27 Penrith Road |
| 图名 Title | 一层点位定位总平面 Setting-out plan |
| 图号 Sheet | SO-01 比例 1:50 @A3 |
| 专业 Discipline | 电气定位 Setting out |
| 版次 Rev | C · 2026-10-14 · 施工图（待持证电工 / 水工复核） |

# 二层点位定位总平面 Setting-out plan

0 2 m

→ 后花园 Rear

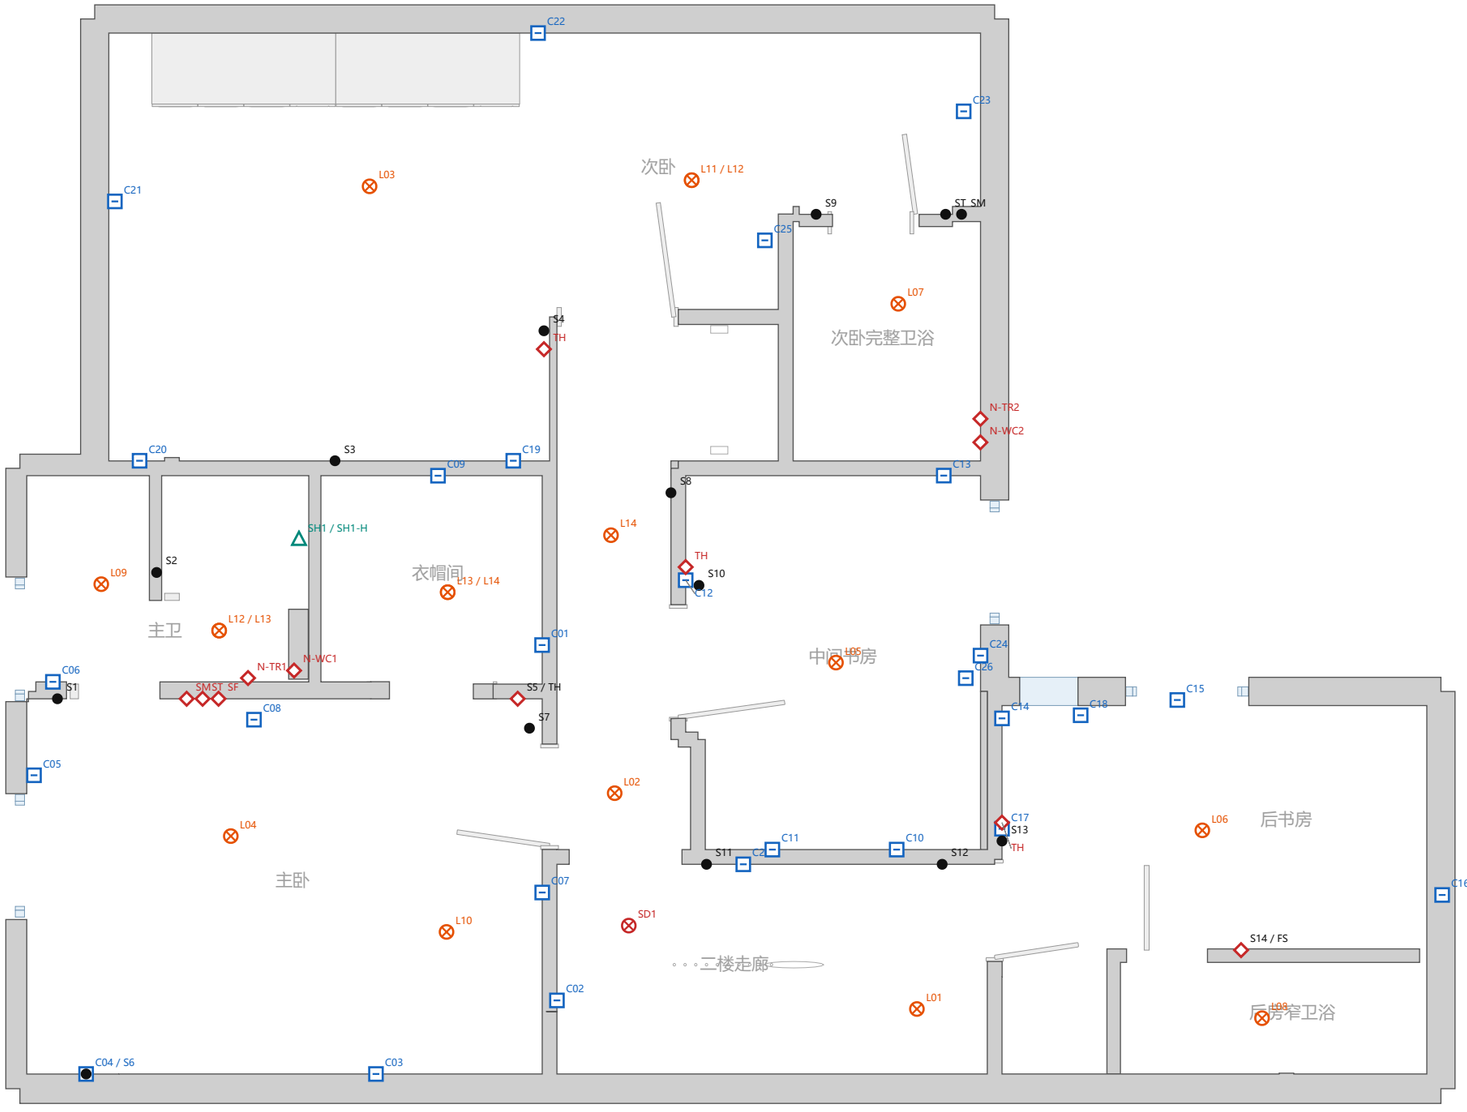


**图例**


- 插座
- 开关
- 专用 / FCU / 新增
- 灯
- 烟感
- 给排水点

**说明 Notes**

1. Rev B：点位全部按已完成的墙面立面图（业主 2026-10-09 确认）。Rev C（2026-10-14）：厨房区 Rev C / 后院 Rev D / 主客厅区 Rev I（模型 v47）；洗衣房开关插座白色；柜内插座 C26 / C38 / C39 / C40 白色；C01 / C02 / C38 改双位。
2. 平面上的位置 = 墙面位置；放线尺寸、高度见定位表里的立面图号（W1- / W2-），哪个区域看哪个立面图文件见 SO-03 / SO-04。
3. 给排水出口见给排水施工图。

| | |
|---|---|
| 项目 Project | 27PR 住宅改造 · 27 Penrith Road |
| 图名 Title | 二层点位定位总平面 Setting-out plan |
| 图号 Sheet | SO-02 比例 1:50 @A3 |
| 专业 Discipline | 电气定位 Setting out |
| 版次 Rev | C · 2026-10-14 · 施工图（待持证电工 / 水工复核） |

# 一层立面图索引 Which elevation set to read

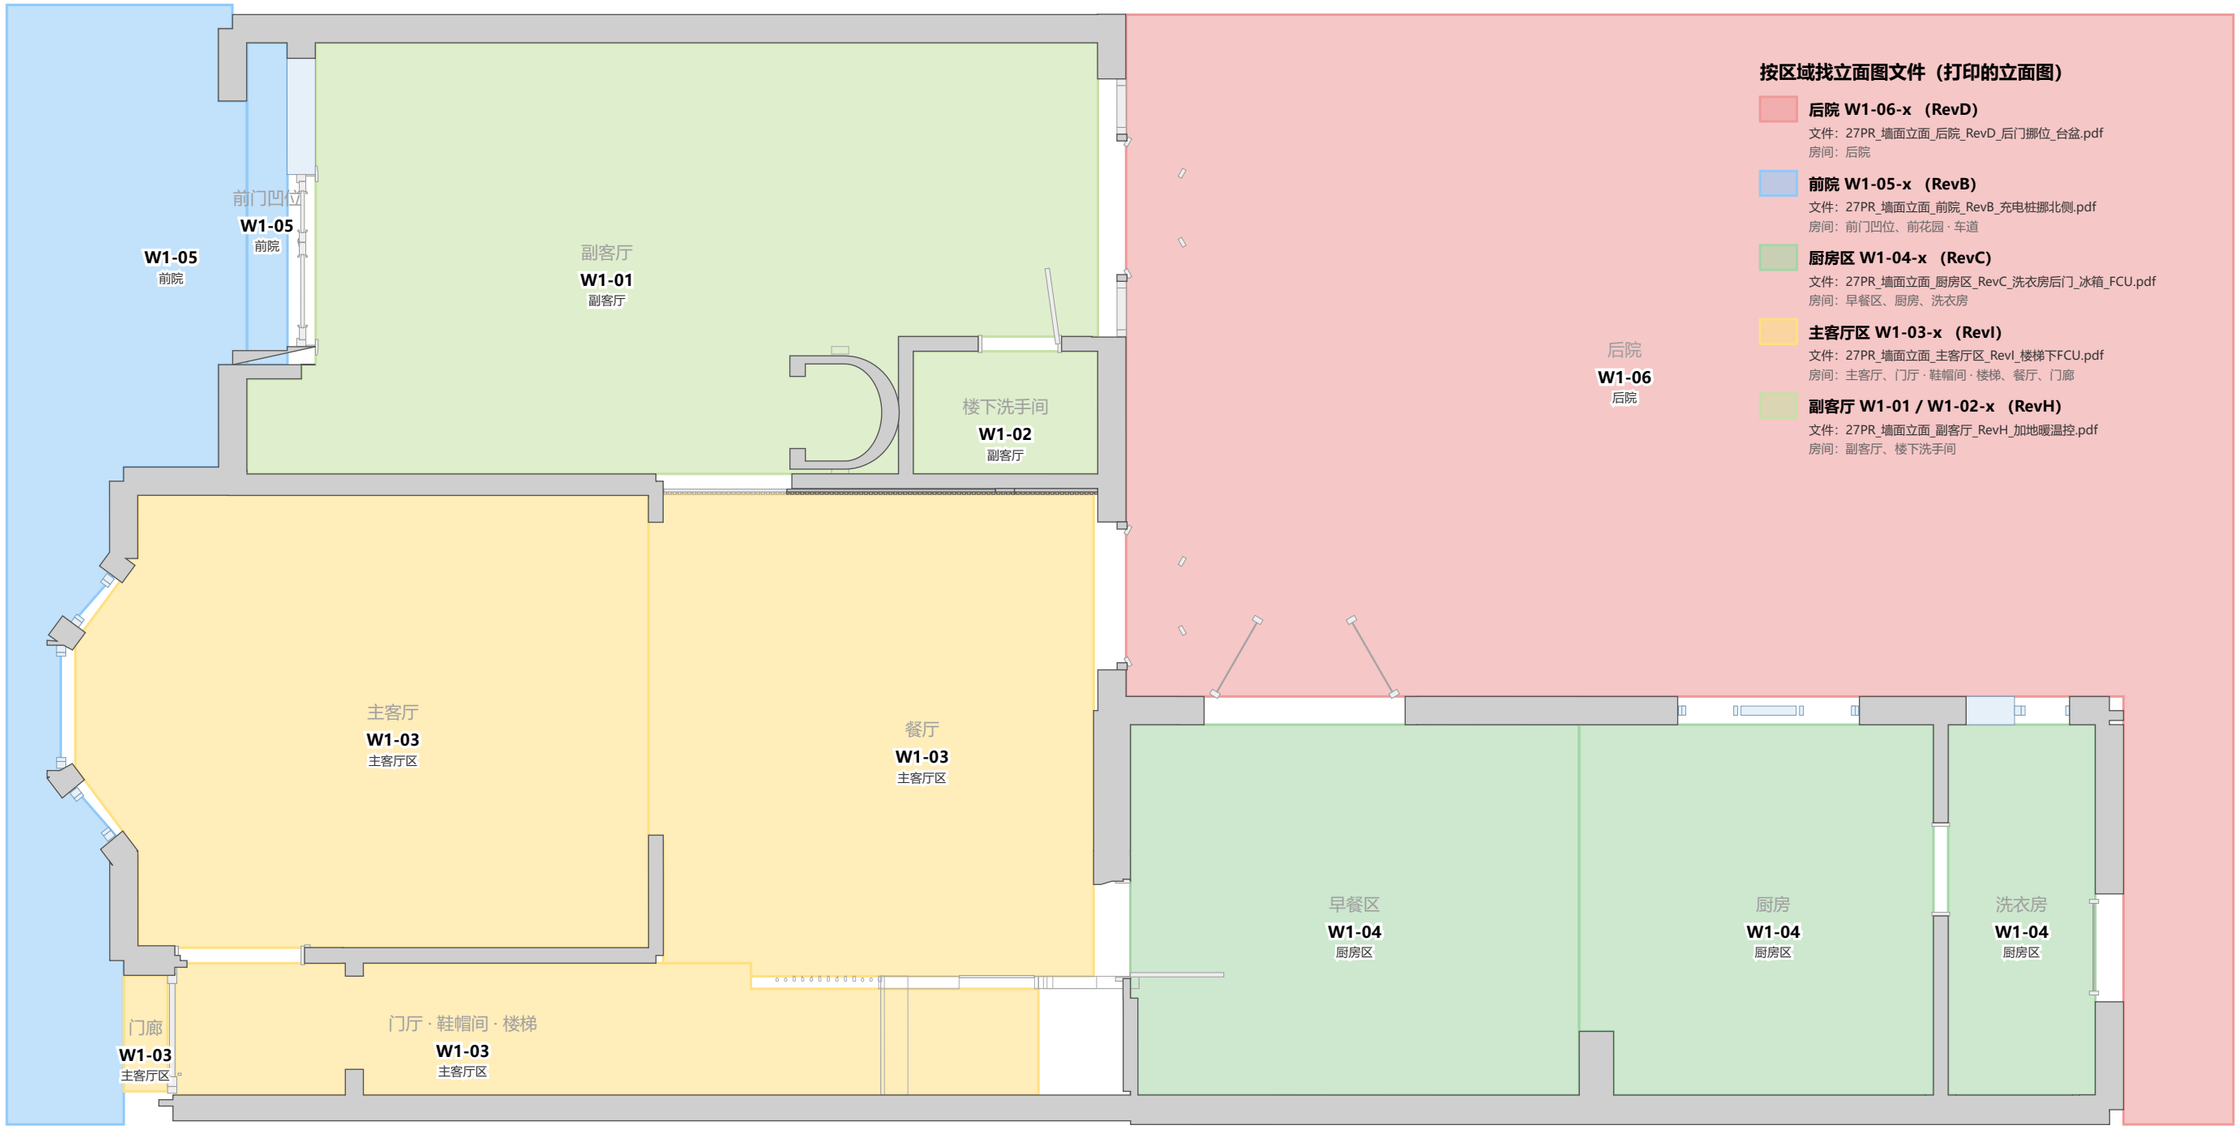


**按区域找立面图文件（打印的立面图）**

**后院 W1-06-x （RevD）**
文件：27PR_墙面立面_后院_RevD_后门挪位_台盆.pdf
房间：后院

**前院 W1-05-x （RevB）**
文件：27PR_墙面立面_前院_RevB_充电桩挪北侧.pdf
房间：前门凹位、前花园 · 车道

**厨房区 W1-04-x （RevC）**
文件：27PR_墙面立面_厨房区_RevC_洗衣房后门_冰箱_FCU.pdf
房间：早餐区、厨房、洗衣房

**主客厅区 W1-03-x （RevI）**
文件：27PR_墙面立面_主客厅区_RevI_楼梯下FCU.pdf
房间：主客厅、门厅 · 鞋帽间 · 楼梯、餐厅、门廊

**副客厅 W1-01 / W1-02-x （RevH）**
文件：27PR_墙面立面_副客厅_RevH_加地暖温控.pdf
房间：副客厅、楼下洗手间

**怎么用 How to use**
1. 定位表里每个点位都写了立面图号，例如 W1-04-6：前面 W1-04 = 区域（本图颜色块），后面 -6 = 该立面图文件里的第 6 张。
2. 按颜色块找到对应的立面图文件（已完成，打印版），翻到那一张按尺寸放线。
3. W1- 为一层，W2- 为二层。

| | |
|---|---|
| 项目 Project | 27PR 住宅改造 · 27 Penrith Road |
| 图名 Title | 一层立面图索引 Which elevation set to read |
| 图号 Sheet | SO-03 比例 1:50 @A3 |
| 专业 Discipline | 电气定位 Setting out |
| 版次 Rev | C · 2026-10-14 · 施工图（待持证电工 / 水工复核） |

# 二层立面图索引 Which elevation set to read

0 2 m

→ 后花园 Rear




## 按区域找立面图文件（打印的立面图）

**二楼走廊 W2-07-x （RevH）**
文件：27PR_墙面立面_二楼走廊_RevH_S12中途开关.pdf
房间：二楼走廊

**后书房 W2-05 / W2-06-x （RevG）**
文件：27PR_墙面立面_后书房_RevG_C16挪后墙.pdf
房间：后书房、后房窄卫浴

**中间书房 W2-04-x （RevD）**
文件：27PR_墙面立面_中间书房_RevD_天花2700.pdf
房间：中间书房

**次卧 W2-01 / W2-02-x （RevP）**
文件：27PR_墙面立面_次卧_RevP_毛巾架出线_床头650.pdf
房间：次卧、次卧完整卫浴

**主卧套间 W2-03-x （RevM）**
文件：27PR_墙面立面_主卧套间_RevM_温控开关挪位.pdf
房间：主卧、主卫、衣帽间

**怎么用 How to use**
1. 定位表里每个点位都写了立面图号，例如 W1-04-6：前面 W1-04 = 区域（本图颜色块），后面 -6 = 该立面图文件里的第 6 张。
2. 按颜色块找到对应的立面图文件（已完成，打印版），翻到那一张按尺寸放线。
3. W1- 为一层，W2- 为二层。

| | |
|---|---|
| 项目 Project | 27PR 住宅改造 · 27 Penrith Road |
| 图名 Title | 二层立面图索引 Which elevation set to read |
| 图号 Sheet | SO-04 比例 1:50 @A3 |
| 专业 Discipline | 电气定位 Setting out |
| 版次 Rev | C · 2026-10-14 · 施工图（待持证电工 / 水工复核） |

# 一层墙面点位定位表（插座 / 开关 / 专用 / 壁灯）

**一层墙面点位定位表（插座 / 开关 / 专用 / 壁灯）（尺寸 mm；左 / 右墙 = 面对墙看的左 / 右；高度 = 底盒中心离本房间完成地面；按立面图号放线）**

| 编号 | 类型 / 名称 | 房间 | 墙面 | 立面图号（见 SO-03 / 04） | 左墙 mm | 右墙 mm | 高度 | 回路 | 备注（立面图） |
|---|---|---|---|---|---|---|---|---|---|
| S1 | 开关 · 4 联开关 4-gang switch | 主客厅 | B · 南墙 | W1-03-3 | 墙角 4000 | 墙角 165 | 1200 | WL4 | 键 3 → 门廊壁灯 G25（户外）；键 4 → 主客厅主灯 G06；键 5 → 主客厅筒灯 上两排（含电梯旁）；键 6 → 主客厅筒灯 右列+下排；4 联开关：B 墙门洞右侧 330 宽墙垛正中（业主 2026-10-09），h1200 |
| S2 | 开关 · 2 联开关 2-gang switch | 门厅 · 鞋帽间 · 楼梯 | G · 北墙 | W1-03-6 | 墙角 1180 | 墙端（通餐厅） 2749 | 1200 | WL4 | 键 1 → 门厅吊灯 G08；键 2 → 前储物间筒灯（+门控开关）；数据写「门厅 · 前储物间旁」；按位置在门厅北墙，内门 F26 前 |
| S4 | 开关 · 4 联开关 4-gang switch | 餐厅 | I · 西墙 | W1-03-8 | 墙端（楼梯口） 837 | 墙角 2987 | 1200 | WL4 | 键 19 → 主客厅主灯 G06；键 20 → 主客厅筒灯 上两排（含电梯旁）；键 21 → 主客厅筒灯 右列+下排；键 18 → 楼梯壁灯 F32；中心离拱门边 200（业主 2026-10-09），h1200 |
| S5 | 开关 · 3 联开关 3-gang switch | 餐厅 | I · 西墙 | W1-03-8 | 墙端（楼梯口） 837 | 墙角 2987 | 1330 | WL4 | 键 7 → G07 区主灯；键 8 → G07 区筒灯 上排+左；键 9 → G07 区筒灯 右+下排；S4 正上方，中心离拱门边 200，h1330 |
| S6 | 开关 · 1 联开关 1-gang switch | 门厅 · 鞋帽间 · 楼梯 | H · 南墙 | W1-03-7 | 楼梯转角 2645 | 墙角 4398 | 1200 | WL4 | 楼梯三控开关（K 键）：楼梯第一级前约 300（业主 2026-10-09：按楼梯位置定），h1200 |
| S7 | 开关 · 1 联开关 1-gang switch | 餐厅 | K · 东墙 | W1-03-10 | 墙角 1589 | 墙角 2342 | 1200 | WL4 | 中心离法式门洞边 150（业主 2026-10-09），h1200 |
| S8 | 开关 · 4 联开关 4-gang switch | 副客厅 | F · 南墙 | W1-01-6 | 墙角 2140 | 墙角 3175 | 1200 | WL4 | 键 10 → G15 吊灯；键 11 → G16 吊灯；键 12 → G15 区筒灯 上排+左；键 13 → G15 区筒灯 下排+右；点位数据原点离墙面 290，已按墙面定位；离暗门洞边约 160（Rev C 暗门改 762 后此边不动） |
| S9 | 开关 · 3 联开关 3-gang switch | 副客厅 | A · 西墙 | W1-01-2 | 墙端（阳角） 1700 | 墙角 925 | 1200 | WL4 | 键 14 → G15 吊灯；键 16 → G15 区筒灯 上排+左；键 17 → G15 区筒灯 下排+右；数据写「储物间门旁」；按模型 v44 是副客厅前门北侧，离门洞边约 150 |
| S10 | 开关 · 1 联开关 1-gang switch | 副客厅 | D · 南墙 | W1-01-4 | 墙角 1120 | 墙端（阳角） 505 | 1200 | WL4 | 键 22 → 卫生间筒灯；洗手间门外，离门洞边约 140（Rev D 门改 686 后此边不动） |
| S11 | 开关 · 3 联开关 3-gang switch | 副客厅 | C · 东墙 | W1-01-4 | 墙角 147 | 墙角 2248 | 1200 | WL4 | 键 27 → 围栏户外 LED 灯带（L40 出线；户外，单控：S11）；键 28 → 后花园投光灯 SOLLA 三头 150W（离地约 3.5 m，双控：S11、S7）；原位落在新花园门组玻璃上 → 挪到左端 295 宽墙段正中（离左端 148），离地 1200 —— 待业主确认 |
| S12 | 开关 · 1 联开关 1-gang switch | 早餐区 | B · 北墙 | W1-04-3 | 墙角 2391 | 敞开（接厨房） 1269 | 1200 | WL4 | 键 26 → 后花园壁灯 G26_2、G26_3（双控：S11、S12）；中心离法式门洞边 150（法式门 v47 挪 91 后跟着挪），h1200 |
| S13 | 开关 · 2 联开关 2-gang switch | 早餐区 | A · 西墙 | W1-04-2 | 墙角 1917 | 墙角 1103 | 1200 | WL4 | 键 31 → 吧台区吊灯（待选）；键 32 → 厨房主灯（待选）；中心离门 KP762 洞边 150（业主 2026-10-09；原 133），h1200 |
| S14 | 开关 · 1 联开关 1-gang switch | 洗衣房 | I · 西墙 | W1-04-8 | 墙角 1330 | 墙角 1690 | 1200 | WL4 | 键 38 → 洗衣房筒灯；通厨房洞口南侧，离洞边约 130（模型 v47，业主 2026-10-14） |
| S15 | 开关 · 1 联开关 1-gang switch | 洗衣房 | K · 东墙 | W1-04-9 | 墙角 1240 | 墙角 1780 | 1200 | WL4 | 键 40 → 后花园壁灯 G26_1；后门锁侧，离门洞边约 140（模型 v47，业主 2026-10-14） |
| C01 | 插座 · 双联插座 Twin socket | 门厅 · 鞋帽间 · 楼梯 | G · 北墙 | W1-03-6 | 墙角 1910 | 墙端（通餐厅） 2019 | 450 | WX1 | 450（英国规格，业主 2026-10-08；数据里房间写「储物间」；按位置在鞋帽间北墙 |
| C02 | 插座 · 双联插座 Twin socket | 餐厅 | I · 西墙 | W1-03-8 | 墙端（楼梯口） 837 | 墙角 2987 | 450 | WX1 | 450（英国规格，业主 2026-10-08；中心离拱门边 200（业主 2026-10-09），h450 |
| C03 | 插座 · 双联插座 Twin socket | 门厅 · 鞋帽间 · 楼梯 | H · 南墙 | W1-03-7 | 楼梯转角 3290 | 墙角 3753 | 450 | WX1 | 450（英国规格，业主 2026-10-08；数据里房间写「储物间」；按位置在楼梯口南墙 |
| C04 | 插座 · 双联插座 Twin socket | 主客厅 | B · 南墙 | W1-03-3 | 墙角 1247 | 墙角 2918 | 1100 | WX1 | 电视墙插座组（4 个双联，面板净距 100）：左上，h1100（业主 2026-10-09） |
| C05 | 插座 · 双联插座 Twin socket | 主客厅 | D · 北墙 | W1-03-5 | 墙角 3415 | 墙角 750 | 450 | WX2 | 沙发背架平台 2（预估 1500）正中，h450（业主 2026-10-09） |
| C07 | 插座 · 双联插座 Twin socket | 主客厅 | A · 西墙 | W1-03-2 | 墙角 488 | 墙角 3748 | 450 | WX1 | 与 C33 同高对称（各离凸窗回墙 257），h450（业主 2026-10-09） |
| C08 | 插座 · 双联插座 Twin socket | 餐厅 | K · 东墙 | W1-03-10 | 墙角 2447 | 墙角 1484 | 450 | WX1 | 450（英国规格，业主 2026-10-08；点位数据原点离墙面 350，按墙面定位（距左端 683）；在餐桌端头旁 |
| C09 | 插座 · 双联插座 Twin socket | 早餐区 | D · 南墙 | W1-04-4 | 墙角（墙垛） 455 | 墙角 3205 | 1200 | WX3 | 台面 C（909）正中，台面上方 300（中心 h1200，业主 2026-10-09）；下面是洗碗机；按 Wren 橱柜图（S8097782/1） |
| C10 | 插座 · 双联插座 Twin socket | 厨房 | F · 东墙 | W1-04-6 | 墙角 2550 | 墙角 470 | 1200 | WX4 | 转角台面 D 上，台面上方 300（中心 h1200，业主 2026-10-09）（转角里面 242 为空腔，不放插座）；按 Wren 橱柜图（S8097782/1） |
| C11 | 插座 · 单联插座 Single socket | 副客厅 | D · 南墙 | W1-01-4 | 墙角 1475 | 墙端（阳角） 150 | 450 | WX2 | 450（英国规格，业主 2026-10-08；从电梯外壳后面挪到 D 墙右端阳角旁（业主 2026-10-08）：中心离右端 150，离地 450，方便插拔 |
| C12 | 插座 · 双联插座 Twin socket | 洗衣房 | J · 北墙 | W1-04-8 | 墙角 640 | 墙角 560 | 450 | WX4 | 450（英国规格，业主 2026-10-08；洗衣机 / 烘干机柜背后，h450；机器电源经 FU1 / FU2 fused switch（模型 v47，业主 2026-10-14） |
| C13 | 插座 · 双联插座 Twin socket | 洗衣房 | I · 西墙 | W1-04-8 | 墙角 1260 | 墙角 1760 | 450 | WX4 | 450（英国规格，业主 2026-10-08；隔墙洗衣房一侧，h450（模型 v47，业主 2026-10-14） |
| C14 | 插座 · 双联插座 Twin socket | 厨房 | E · 北墙 | W1-04-5 | 敞开（接早餐区） 880 | 墙角 2010 | 450 | WX3 | 450（英国规格，业主 2026-10-08；大窗北端下方（窗台约 1120） |
| C15 | 插座 · 双联插座 Twin socket | 餐厅 | L · 北墙 | W1-03-11 | 墙端（拱门旁） 1568 | 墙角 1942 | 450 | WX1 | 450（英国规格，业主 2026-10-08；中心离暗门 V15 洞边 800（业主 2026-10-09），h450 |
| C16 | 插座 · 双联插座 Twin socket | 副客厅 | F · 南墙 | W1-01-6 | 墙角 3164 | 墙角 2151 | 600 | WX2 | 电视柜上方 600（原位置被电视柜挡住）；电视插座三个一组，以 C29 为中，面板之间净距 100（中心距 246），离地 600（业主 2026-10-08） |
| C17 | 插座 · 双联插座 Twin socket | 主客厅 | D · 北墙 | W1-03-5 | 墙角 1915 | 墙角 2250 | 450 | WX1 | 沙发背架平台 1（预估 1500）正中，h450（业主 2026-10-09） |
| C18 | 插座 · 双联插座 Twin socket | 副客厅 | A · 西墙 | W1-01-2 | 墙端（阳角） 1650 | 墙角 975 | 450 | WX2 | 450（英国规格，业主 2026-10-08；⚠ 中心离门洞边仅约 100，门套外沿约 45，双联面板（146 宽）会压到门套 —— 建议挪到离门洞边 ≥ 250（v44 点位审阅模型原位约 250），待业主确认；数据里房间写「储物间」，按位置在副客厅前门北侧（Rev E 前门改 1200 单扇，此洞边不动） |
| C19 | 插座 · 双联插座 Twin socket | 副客厅 | B · 北墙 | W1-01-3 | 墙角 5740 | 墙角 640 | 450 | WX2 | 450（英国规格，业主 2026-10-08 |
| C20 | 插座 · 户外插座 IP66 | 后院 | A · 西墙（外） | W1-06-1 | 墙角 5289 | 墙角（围栏） 271 | 600 | WX5 | 户外 600，防水盖朝下；IP66；按模型在后墙北端（距右端墙角 271），盆栽棕榈后面 —— 现场核对 |
| C21 | 插座 · 户外插座 IP66 | 后院 | B · 南墙（外） | W1-06-2 | 墙角 4010 | 墙角 4125 | 600 | WX5 | 户外 600，防水盖朝下；IP66；v44 点位审阅模型另有建议位（离南端约 700，靠近 L09） |
| C22 | 插座 · 户外插座 IP66 | 后院 | B · 南墙（外） | W1-06-2 | 墙角 320 | 墙角 7815 | 600 | WX5 | 户外 600，防水盖朝下 |
| C23 | 插座 · 双联插座 Twin socket | 早餐区 | D · 南墙 | W1-04-4 | 墙角（墙垛） 1321 | 墙角 2339 | 1200 | WX3 | 半岛台 A 靠墙一端正中（824 宽），台面上方 300（中心 h1200，业主 2026-10-09）；按 Wren 橱柜图（S8097782/1） |
| C24 | 插座 · 双联插座 Twin socket | 厨房 | F · 东墙 | W1-04-6 | 墙角 1950 | 墙角 1070 | 1200 | WX4 | 转角台面 D 上，离冰箱边约 225，台面上方 300（中心 h1200，业主 2026-10-09）；按 Wren 橱柜图（S8097782/1） |
| C25 | 插座 · 双联插座 Twin socket | 早餐区 | A · 西墙 | W1-04-2 | 墙角 2190 | 墙角 830 | 450 | 冰箱专线 | 450（英国规格，业主 2026-10-08；冰箱专用插座（单独一路线 = 专线），冰箱背后，h450（模型 v47，业主 2026-10-14） |
| C27 | 插座 · 双联插座 Twin socket | 早餐区 | D · 南墙 | W1-04-4 | 墙角（墙垛） 3070 | 墙角 590 | 450 | WX3 | 450（英国规格，业主 2026-10-08；排水立管箱 S2 旁 |
| C28 | 插座 · 双联插座 Twin socket | 副客厅 | B · 北墙 | W1-01-3 | 墙角 3000 | 墙角 3380 | 450 | WX2 | 450（英国规格，业主 2026-10-08；从 L 形沙发后面挪出（业主 2026-10-08）：中心离左端墙角 3000，在沙发端头（约 2696）与书柜 G18（约 3335）之间，离地 450 |
| C29 | 插座 · 双联插座 Twin socket | 副客厅 | F · 南墙 | W1-01-6 | 墙角 3410 | 墙角 1905 | 600 | WX2 | 电视柜上方 600（原位置被电视柜挡住）；电视插座三个一组，以 C29 为中，面板之间净距 100（中心距 246），离地 600（业主 2026-10-08） |
| C30 | 插座 · 双联插座 Twin socket | 副客厅 | F · 南墙 | W1-01-6 | 墙角 3656 | 墙角 1659 | 600 | WX2 | 电视柜上方 600（原位置被电视柜挡住）；电视插座三个一组，以 C29 为中，面板之间净距 100（中心距 246），离地 600（业主 2026-10-08） |
| C31 | 插座 · 双联插座 Twin socket | 主客厅 | B · 南墙 | W1-03-3 | 墙角 1493 | 墙角 2672 | 1100 | WX1 | 电视墙插座组：右上，h1100 |
| C32 | 插座 · 双联插座 Twin socket | 主客厅 | B · 南墙 | W1-03-3 | 墙角 1247 | 墙角 2918 | 350 | WX1 | 电视墙插座组：左下，h350（在电视柜后面，柜高 450） |
| C33 | 插座 · 双联插座 Twin socket | 主客厅 | A · 西墙 | W1-03-2 | 墙角 3923 | 墙角 313 | 450 | WX1 | 与 C07 同高对称（各离凸窗回墙 257），h450（业主 2026-10-09；在柜 G02 后面） |
| C34 | 插座 · 户外插座 IP66 | 前门凹位 | A · 北侧 | W1-05-2 | 墙端（外） 120 | 墙角 210 | 600 | WX5 | 户外 600，防水盖朝下；⚠ 点位数据在北侧墙、洗车龙头 FT 正上方约 180（插座与龙头同一竖线）；v44 点位审阅模型放在 C 墙（墙垛内侧，离墙端约 60）—— 待业主定 |

| | |
|---|---|
| 项目 Project | 27PR 住宅改造 · 27 Penrith Road |
| 图名 Title | 一层墙面点位定位表（插座 / 开关 / 专用 / 壁灯） |
| 图号 Sheet | SO-05 比例 — @A3 |
| 专业 Discipline | 电气定位 Setting out |
| 版次 Rev | C · 2026-10-14 · 施工图（待持证电工 / 水工复核） |

# 一层墙面点位定位表（插座 / 开关 / 专用 / 壁灯）

**一层墙面点位定位表（插座 / 开关 / 专用 / 壁灯）（尺寸 mm；左 / 右端 = 面对墙看的左 / 右；高度 = 底盒中心离本房间完成地面；按立面图号放线）**

| 编号 | 类型 / 名称 | 房间 | 墙面 | 立面图号（见 SO-03 / 04） | 左端 mm | 右端 mm | 高度 | 回路 | 备注（立面图） |
|---|---|---|---|---|---|---|---|---|---|
| C35 | 插座 · 双联插座 Twin socket（新增） | 主客厅 | B · 南墙 | W1-03-3 | 墙角 1493 | 墙角 2672 | 350 | WX1 | 电视墙插座组：右下，h350（在电视柜后面）；新增（业主 2026-10-09） |
| C36 | 插座 · 双联插座 Twin socket | 厨房 | G · 南墙 | W1-04-6 | 墙角 800 | 墙角（墙垛） 1810 | 1200 | WX3 | 台面 B 上，台面上方 300（中心 h1200，业主 2026-10-09），灶左边，离灶边 332（≥ 300）；按 Wren 橱柜图（S8097782/1） |
| C37 | 插座 · 双联插座 Twin socket | 厨房 | G · 南墙 | W1-04-6 | 墙角 2350 | 墙角（墙垛） 260 | 1200 | WX3 | 台面 B 上，台面上方 300（中心 h1200，业主 2026-10-09），灶右边，离灶边 358（≥ 300），离墙垛 260；按 Wren 橱柜图（S8097782/1） |
| C38 | 插座 · 洗碗机插座 Twin socket（在角柜内，双位，白色） | 早餐区 | D · 南墙 | W1-04-4 | 墙角（墙垛） 1080 | 墙角 2580 | 450 | WX3 | 在洗碗机旁转角柜（Wren 7）后面，h450（业主 2026-10-09）；由楼梯下 FD 控制；洗碗机 Bosch 集成 600 位于离墙垛 36–636；按 Wren 橱柜图（S8097782/1） |
| C39 | 插座 · 灶台 / 烤箱供电插座（双联，在烤箱 / 灶背后）（柜内，白色） | 厨房 | G · 南墙 | W1-04-6 | 墙角 1562 | 墙角（墙垛） 1048 | 300 | 待定 | 用途：给灶 AEG HKB95820NB（点火）+ 烤箱 AEG BPX535061M 供电；放在烤箱 / 灶正后方（烤箱中心，离墙垛 1048），位置可按电器说明书 / 现场调整（业主 2026-10-09）；由楼梯下 FO 控制；烤箱按说明书确认 13A 插头或接独立 cooker 回路（电工定） |
| C40 | 插座 · 烟机插座 Single socket（在烟机柜内）（柜内，白色） | 厨房 | G · 南墙 | W1-04-6 | 墙角 1562 | 墙角（墙垛） 1048 | 1900 | 待定 | 烟机柜（Wren 18，1000 宽，1554–2129）内，烟机为内循环；由楼梯下 FO 控制；按 Wren 橱柜图（S8097782/1） |
| C42 | 插座 · 双位插座 Twin socket（antique brass） | 厨房 | F · 东墙 | W1-04-6 | 墙角 400 | 墙角 2620 | 450 | WX3 | 新增（业主 2026-10-14）：厨房一侧，通洗衣房洞口左边墙段（窗墙角到洞口 800）正中，h450（模型 v47，业主 2026-10-14） |
| C43 | 插座 · 双位插座 Twin socket（白色） | 洗衣房 | K · 东墙 | W1-04-9 | 墙角 2677 | 墙角 343 | 850 | 待定 | 新增（业主 2026-10-15）：锅炉 / 热水器处，FU1–FU4 正下方居中，h850（在软水机上方）；给软水机及热水器附属设备供电 |
| EV | 专用 / FCU / 新增 · EV 充电桩预留 Charger（D07） | 前门凹位 | A · 北侧 | W1-05-2 | 墙端（外） 165 | 墙角 165 | 1050 | WP5 | 预留位（业主 2026-10-09）：由 B 墙门边挪到北侧墙正中（墙宽 330），中心离地约 1050；电源 WP5 专线；室内隔离开关 D08 原定在副客厅墙内 —— 跟着挪位后请电工核对穿线路径；充电桩型号 / 安装支架按产品 |
| FD | 专用 / FCU / 新增 · Fused switch FCU · 洗碗机（柜内，白色） | 餐厅 | J · 南墙 | W1-03-9 | 墙端（厨房门框） 464 | 楼梯起步 2507 | 1200 | 待定 | 楼梯下柜内（配电箱旁）单联 fused switch，业主 2026-10-14 集中；装在楼梯下柜子里面（本面板背面，检修门旁），白色；洗碗机；一排 4 个（中心距 96） |
| FO1 | 专用 / FCU / 新增 · Fused switch FCU · 烤箱（柜内，白色） | 餐厅 | J · 南墙 | W1-03-9 | 墙端（厨房门框） 368 | 楼梯起步 2603 | 1200 | 待定 | 楼梯下柜内（配电箱旁）单联 fused switch，业主 2026-10-14 集中；装在楼梯下柜子里面（本面板背面，检修门旁），白色；烤箱；一排 4 个（中心距 96） |
| FO2 | 专用 / FCU / 新增 · Fused switch FCU · 灶（点火）（柜内，白色） | 餐厅 | J · 南墙 | W1-03-9 | 墙端（厨房门框） 272 | 楼梯起步 2699 | 1200 | 待定 | 楼梯下柜内（配电箱旁）单联 fused switch，业主 2026-10-14 集中；装在楼梯下柜子里面（本面板背面，检修门旁），白色；灶（点火）；一排 4 个（中心距 96） |
| FO3 | 专用 / FCU / 新增 · Fused switch FCU · 烟机（柜内，白色） | 餐厅 | J · 南墙 | W1-03-9 | 墙端（厨房门框） 176 | 楼梯起步 2795 | 1200 | 待定 | 楼梯下柜内（配电箱旁）单联 fused switch，业主 2026-10-14 集中；装在楼梯下柜子里面（本面板背面，检修门旁），白色；烟机；一排 4 个（中心距 96） |
| FU1 | 专用 / FCU / 新增 · Fused switch FCU · 洗衣机（白色） | 洗衣房 | K · 东墙 | W1-04-9 | 墙角 2533 | 墙角 487 | 1200 | 待定 | 锅炉下方一排 4 个单联 fused switch（中心距 96），白色；洗衣机（模型 v47，业主 2026-10-14） |
| FU2 | 专用 / FCU / 新增 · Fused switch FCU · 烘干机（白色） | 洗衣房 | K · 东墙 | W1-04-9 | 墙角 2629 | 墙角 391 | 1200 | 待定 | 锅炉下方一排 4 个单联 fused switch（中心距 96），白色；烘干机（模型 v47，业主 2026-10-14） |
| FU3 | 专用 / FCU / 新增 · Fused switch FCU · 锅炉（白色） | 洗衣房 | K · 东墙 | W1-04-9 | 墙角 2725 | 墙角 295 | 1200 | 待定 | 锅炉下方一排 4 个单联 fused switch（中心距 96），白色；锅炉（模型 v47，业主 2026-10-14） |
| FU4 | 专用 / FCU / 新增 · Fused switch FCU · 地暖电子控制（白色） | 洗衣房 | K · 东墙 | W1-04-9 | 墙角 2821 | 墙角 199 | 1200 | 待定 | 锅炉下方一排 4 个单联 fused switch（中心距 96），白色；地暖电子控制（模型 v47，业主 2026-10-14） |
| TH | 专用 / FCU / 新增 · 地暖温控面板 UFH thermostat | 主客厅 | C · 东墙 | W1-03-4 | 墙角 3010 | 墙角 734 | 1050 | 待定 | S3 正下方，中心距 150（业主 2026-10-10，同主卧 做法）；有线温控需穿线到地暖分水器接线中心，无线温控也按此位置留底盒；型号由地暖供应商定 |
| TH | 专用 / FCU / 新增 · 地暖温控面板 UFH thermostat | 副客厅 | F · 南墙 | W1-01-6 | 墙角 2140 | 墙角 3175 | 1050 | 待定 | S8 正下方，中心距 150（业主 2026-10-10，同主卧 做法）；有线温控需穿线到地暖分水器接线中心，无线温控也按此位置留底盒；型号由地暖供应商定 |
| FT | 给排水点 · 洗车龙头 Car-wash tap | 前门凹位 | A · 北侧 | W1-05-2 | 墙端（外） 116 | 墙角 214 | 420 | 冷 / 热 | 给排水施工图 Rev C：热水器下软水机前三通引出，穿新砌外墙出户；模型中心约离地 420 |
| OD | 给排水点 · 户外台盆排水 Waste 32 | 后院 | C · 西墙（外） | W1-06-3 | 墙角（围墙） 2654 | 墙角 836 | 350 | 排水 32 | 排水 32：穿后墙接洗衣房地坪下管（给排水图）；高度按立柱盆存水弯现场定（模型 v47，业主 2026-10-14） |
| OW | 给排水点 · 户外台盆冷水 Cold supply 15 | 后院 | C · 西墙（外） | W1-06-3 | 墙角（围墙） 2794 | 墙角 696 | 600 | 冷水 15 | 户外台盆（立柱盆，挪到后门左边、壁灯 L08 下）冷水：15 硬水，室内设隔离阀 + 防回流 DCV，室外段防冻保温；出水位按台盆 / 龙头产品现场定（模型 v47，业主 2026-10-14） |
| L01 | 灯 · 壁灯 F32 | 餐厅 | I · 西墙 | W1-03-8 | 墙端（楼梯口） 486 | 墙角 3338 | 2100 |  | 壁灯：位置不变，加高到 h2100（业主 2026-10-09；原 1930） |
| L08 | 灯 · 壁灯 G26_1（户外） | 后院 | C · 西墙（外） | W1-06-3 | 墙角（围墙） 2685 | 墙角 805 | 1770 |  | 户外壁灯 G26_1，IP44 以上；挪到洗衣房后门左边（中心 x 1.845）（模型 v47，业主 2026-10-14） |
| L09 | 灯 · 壁灯 G26_2（户外） | 后院 | B · 南墙（外） | W1-06-2 | 墙角 4850 | 墙角 3285 | 2000 |  | 户外壁灯 G26_2，IP44 以上；位置不变，h2000（业主 2026-10-09，与 L10 同高；原 1800） |
| L10 | 灯 · 壁灯 G26_3（户外） | 后院 | B · 南墙（外） | W1-06-2 | 墙角 1527 | 墙角 6608 | 2000 |  | 户外壁灯 G26_3，IP44 以上；在洗衣房小窗与厨房大窗之间墙段正中（两边各约 627），h2000（业主 2026-10-09；原贴厨房大窗边、h1800） |
| L40 | 灯 · 壁灯 G26_4（户外） | 后院 | A · 西墙（外） | W1-06-1 | 墙角 1840 | 墙角（围栏） 3720 | 3350 |  |  |

| | |
|---|---|
| 项目 Project | 27PR 住宅改造 · 27 Penrith Road |
| 图名 Title | 一层墙面点位定位表（插座 / 开关 / 专用 / 壁灯） |
| 图号 Sheet | SO-06 比例 — @A3 |
| 专业 Discipline | 电气定位 Setting out |
| 版次 Rev | C · 2026-10-14 · 施工图（待持证电工 / 水工复核） |

# 一层天花灯位 / 其他点位定位表

**一层天花灯位 / 其他点位定位表（尺寸 mm；左 / 右端 = 面对墙看的左 / 右；高度 = 底盒中心离本房间完成地面；按立面图号放线）**

| 编号 | 类型 / 名称 | 房间 | 天花图号（见 SO-03 / 04） | 南北向：距墙 | 东西向：距墙 | 天花高 | 回路 | 开关 / 备注 |
|---|---|---|---|---|---|---|---|---|
| L02 | 灯 · 主灯 G07 | 餐厅 | W1-03-1 | 北 1650 / 南 2280 | 西 1850 / 东 1780 | 2600 | WL1 | S5 键 7 |
| L03 | 灯 · 主灯 G06 | 主客厅 | W1-03-1 | 北 1970 / 南 1780 | 西 2510 / 东 2160 | 2600 | WL1 | S1 键 4 / S4 键 19 |
| L04 | 灯 · 主灯 G08 | 门厅 · 鞋帽间 · 楼梯 | W1-03-1 | 北 600 / 南 480 | 西 770 / 东 630 | 2600 | WL1 | S2 键 1 |
| L05 | 灯 · 主灯 G15 | 副客厅 | W1-01-1 | 北 1790 / 南 1730 | 西 2020 / 东 4360 | 2600 | WL2 | S8 键 10 / S9 键 14 |
| L06 | 灯 · 主灯 G16 | 副客厅 | W1-01-1 | 北 1140 / 南 1250 | 西 5160 / 东 1220 | 2600 | WL2 | S8 键 11 |
| L07 | 灯 · 门廊吊灯 G25（户外） | 门廊 | W1-03-1 | 北 480 / 南 470 | 西 160 / 东 200 | 2600 | WL1 | S1 键 3 |
| L11 | 灯 · GU10 筒灯 | 主客厅 | W1-03-1 | 北 3020 / 南 720 | 西 3220 / 东 950 | 2600 | WL1 | S1 键 6 / S4 键 21 |
| L12 | 灯 · GU10 筒灯 | 主客厅 | W1-03-1 | 北 3020 / 南 720 | 西 1990 / 东 2180 | 2600 | WL1 | S1 键 6 / S4 键 21 |
| L13 | 灯 · GU10 筒灯 | 主客厅 | W1-03-1 | 北 3020 / 南 720 | 西 750 / 东 3410 | 2600 | WL1 | S1 键 6 / S4 键 21 |
| L14 | 灯 · GU10 筒灯 | 主客厅 | W1-03-1 | 北 2000 / 南 1740 | 西 1280 / 东 3400 | 2600 | WL1 | S1 键 5 / S4 键 20 |
| L15 | 灯 · GU10 筒灯 | 主客厅 | W1-03-1 | 北 910 / 南 2840 | 西 2260 / 东 2160 | 2600 | WL1 | S1 键 5 / S4 键 20 |
| L16 | 灯 · GU10 筒灯 | 主客厅 | W1-03-1 | 北 910 / 南 2840 | 西 3490 / 东 930 | 2600 | WL1 | S1 键 5 / S4 键 20 |
| L17 | 灯 · GU10 筒灯 | 主客厅 | W1-03-1 | 北 1980 / 南 1760 | 西 3740 / 东 930 | 2600 | WL1 | S1 键 6 / S4 键 21 |
| L18 | 灯 · GU10 筒灯 | 主客厅 | W1-03-1 | 北 910 / 南 2840 | 西 1020 / 东 3400 | 2600 | WL1 | S1 键 5 / S4 键 20 |
| L19 | 灯 · GU10 筒灯 | 餐厅 | W1-03-1 | 北 2560 / 南 1370 | 西 1820 / 东 1810 | 2600 | WL1 | S5 键 9 |
| L20 | 灯 · GU10 筒灯 | 餐厅 | W1-03-1 | 北 2560 / 南 1260 | 西 580 / 东 3050 | 2600 | WL1 | S5 键 9 |
| L21 | 灯 · GU10 筒灯 | 餐厅 | W1-03-1 | 北 1600 / 南 2220 | 西 610 / 东 3020 | 2600 | WL1 | S5 键 8 |
| L22 | 灯 · GU10 筒灯 | 餐厅 | W1-03-1 | 北 710 / 南 3110 | 西 580 / 东 3050 | 2600 | WL1 | S5 键 8 |
| L23 | 灯 · GU10 筒灯 | 餐厅 | W1-03-1 | 北 710 / 南 3220 | 西 1820 / 东 1810 | 2600 | WL1 | S5 键 8 |
| L24 | 灯 · GU10 筒灯 | 餐厅 | W1-03-1 | 北 710 / 南 3220 | 西 3050 / 东 580 | 2600 | WL1 | S5 键 8 |
| L25 | 灯 · GU10 筒灯 | 餐厅 | W1-03-1 | 北 1670 / 南 2260 | 西 3070 / 东 560 | 2600 | WL1 | S5 键 9 |
| L26 | 灯 · GU10 筒灯 | 餐厅 | W1-03-1 | 北 2560 / 南 1370 | 西 3050 / 东 580 | 2600 | WL1 | S5 键 9 |
| L27 | 灯 · 主灯位（灯具待选） | 厨房 | W1-04-1 | 北 1360 / 南 1660 | 西 1330 / 东 1560 | 2600 | WL2 | S13 键 32 |
| L28 | 灯 · 主灯位（灯具待选） | 早餐区 | W1-04-1 | 北 1420 / 南 1600 | 西 2280 / 东 1380 | 2600 | WL2 | S13 键 31 |
| L29 | 灯 · GU10 筒灯 | 门厅 · 鞋帽间 · 楼梯 | W1-03-1 | 北 560 / 南 510 | 西 460 / 东 5070 | 2600 | WL1 | S2 键 2 |
| L30 | 灯 · GU10 筒灯 | 副客厅 | W1-01-1 | 北 2920 / 南 590 | 西 2590 / 东 2730 | 2600 | WL2 | S8 键 13 / S9 键 17 |
| L31 | 灯 · GU10 筒灯 | 副客厅 | W1-01-1 | 北 2910 / 南 610 | 西 1490 / 东 3820 | 2600 | WL2 | S8 键 13 / S9 键 17 |
| L32 | 灯 · GU10 筒灯 | 副客厅 | W1-01-1 | 北 1790 / 南 1730 | 西 950 / 东 5430 | 2600 | WL2 | S8 键 12 / S9 键 16 |
| L33 | 灯 · GU10 筒灯 | 副客厅 | W1-01-1 | 北 730 / 南 2790 | 西 950 / 东 5430 | 2600 | WL2 | S8 键 12 / S9 键 16 |
| L34 | 灯 · GU10 筒灯 | 副客厅 | W1-01-1 | 北 730 / 南 2790 | 西 2010 / 东 4370 | 2600 | WL2 | S8 键 12 / S9 键 16 |
| L35 | 灯 · GU10 筒灯 | 副客厅 | W1-01-1 | 北 750 / 南 2770 | 西 3230 / 东 3150 | 2600 | WL2 | S8 键 12 / S9 键 16 |
| L36 | 灯 · GU10 筒灯 | 副客厅 | W1-01-1 | 北 1750 / 南 1770 | 西 3260 / 东 3120 | 2600 | WL2 | S8 键 13 / S9 键 17 |
| L37 | 灯 · GU10 筒灯 | 副客厅 | W1-01-1 | 北 2940 / 南 570 | 西 3820 / 东 1490 | 2600 | WL2 | S8 键 13 / S9 键 17 |
| L38 | 灯 · GU10 筒灯 | 洗衣房 | W1-04-1 | 北 1510 / 南 1510 | 西 600 / 东 600 | 2600 | WL2 | S14 键 38 |
| L39 | 灯 · GU10 筒灯 | 楼下洗手间 | W1-02-1 | 北 580 / 南 420 | 西 630 / 东 880 | 2600 | WL2 | S10 键 22 |
| C26 | 插座 · 单联插座 | 厨房（吧台区） | （平面） | — | — | 800 |  | 岛台；半岛台柜内插座 h 800（白色，业主 2026-10-14） |

| | |
|---|---|
| 项目 Project | 27PR 住宅改造 · 27 Penrith Road |
| 图名 Title | 一层天花灯位 / 其他点位定位表 |
| 图号 Sheet | SO-07 比例 — @A3 |
| 专业 Discipline | 电气定位 Setting out |
| 版次 Rev | C · 2026-10-14 · 施工图（待持证电工 / 水工复核） |

# 二层墙面点位定位表（插座 / 开关 / 专用 / 壁灯）

**二层墙面点位定位表（插座 / 开关 / 专用 / 壁灯）（尺寸 mm；左 / 右墙 = 面对墙看的左 / 右；高度 = 底盒中心离本房间完成地面；按立面图号放线）**

| 编号 | 类型 / 名称 | 房间 | 墙面 | 立面图号（见 SO-03 / 04） | 左墙 mm | 右墙 mm | 高度 | 回路 | 备注（立面图） |
|---|---|---|---|---|---|---|---|---|---|
| S1 | 开关 · 1 联开关 1-gang switch | 主卧 | B · 北墙 | W2-03-3 | 墙角 116 | 墙角 3954 | 1200 | WL4 | 键 6 → 盥洗室筒灯；主卫入口 F25 洞口与前墙之间 232 宽墙垛正中（各 116）；Rev E 按 PD 一门两用定位后墙垛 232 |
| S2 | 开关 · 1 联开关 1-gang switch | 主卫 | G · 东墙 | W2-03-6 | 墙角 789 | 墙角 892 | 1200 | WL4 | 键 6+ → 主卫筒灯；隔墙端头往北 150（端头装 PD 47 框，面板边离框约 60），h1200 |
| S3 | 开关 · 1 联开关 1-gang switch | 次卧 | H · 南墙 | W2-01-6 | 墙角 1704 | 墙角 1844 | 1360 | WL4 | 键 2 → 次卧主灯 F19；床头板水平居中；中心高于床头板顶 150，h=1360 |
| S4 | 开关 · 2 联开关 2-gang switch | 次卧 | G · 东墙 | W2-01-5 | 门洞边 150 | 墙角 1060 | 1200 | WL4 | 键 10 → 次卧主灯 F19；键 11 → 次卧主灯位（待选）；靠 F 墙转角：开关中心距左端 150，离地 1200 |
| S5 | 开关 · 1 联开关 1-gang switch | 主卧 | B · 北墙 | W2-03-3 | 墙角 3870 | 墙角 200 | 1200 | WL4 | 键 5 → 衣帽间吸顶灯；衣帽间洞口与东墙角之间 400 宽墙段正中（各 200），在 F27 合页侧外；业主 2026-10-08 确认（点位图 Rev A 原落在洞口内） |
| S6 | 开关 · 2 联开关 2-gang switch | 主卧 | D · 南墙 | W2-03-5 | 墙角 3720 | 墙角 425 | 850 | WL4 | 键 12 → 主卧 主灯 F20；键 13 → 主卧 筒灯；床头开关：C04 正上方，h850（业主 2026-10-09，躺在床上够得到） |
| S7 | 开关 · 2 联开关 2-gang switch | 主卧 | C · 东墙 | W2-03-4 | 墙角 240 | 墙角 2820 | 1200 | WL4 | 键 14 → 主卧 主灯 F20；键 15 → 主卧 筒灯；门洞与北墙角之间 369 宽墙段（锁舌侧） |
| S8 | 开关 · 1 联开关 1-gang switch | 二楼走廊 | F · 东墙 | W2-07-5 | 墙角 200 | 墙角 2013 | 1200 | WL4 | 键 3 → 走廊吸顶灯 F11 ×2；走廊北端：中心离 F 墙左端墙角 200（业主 2026-10-09），h1200 |
| S9 | 开关 · 1 联开关 1-gang switch | 次卧 | D · 南墙 | W2-01-4 | 墙角 1340 | 墙端（阳角） 350 | 1200 | WL4 | 键 1 → 次卧卫浴筒灯；卫浴门外 D 墙：离门洞边 150、离墙端 350（业主 2026-10-08：门洞到 E 墙转角留 500） |
| S10 | 开关 · 1 联开关 1-gang switch | 中间书房 | A · 西墙 | W2-04-2 | 墙角（南端墙面凸出 100 / 160 两级） 1200 | 墙角 892 | 1200 | WL4 | 键 4 → 中间书房 主灯 F22 |
| S11 | 开关 · 2 联开关 2-gang switch | 二楼走廊 | H · 北墙 | W2-07-6 | 墙端（靠 G 墙） 200 | 后书房门口（下行台阶尽头） 2272 | 1200 | WL4 | 键 16 → 走廊吸顶灯 F11 ×2；键 17 → 楼梯吊灯 F06（三控：一层 S6 + 二层 S11、S12）；楼梯口，两联双控（BG NAB42，一块面板）：D 键 = 走廊灯（与 S8 双控），K 键 = 楼梯吊灯 F06 三控：一层 S6（双控）+ 二层 S12（中途）+ 二层 S11（双控）；中心离 H 墙左端（靠 G 墙）200，h1200 |
| S12 | 开关 · 1 联开关 1-gang switch | 二楼走廊 | H · 北墙 | W2-07-6 | 墙端（靠 G 墙） 2122 | 后书房门口（下行台阶尽头） 350 | 1200 | WL4 | 键 7 → 楼梯吊灯 F06（三控：一层 S6 + 二层 S11、S12）；后书房门旁，单联中途开关（BG NAB13）K 键（K 键 = 楼梯吊灯 F06 三控：一层 S6（双控）+ 二层 S12（中途）+ 二层 S11（双控））；中心离后书房门口 350；此段地面为下行台阶，h1200 起算面现场按台阶 / 平台定 |
| S13 | 开关 · 1 联开关 1-gang switch | 后书房 | A · 西墙 | W2-05-2 | 墙角 1900 | 墙角 1150 | 1200 | WL4 | 键 8 → 后书房 主灯 F23；中心离房门洞边 150（业主 2026-10-09），h1200 |
| S14 | 开关 · 1 联开关 1-gang switch | 后书房 | D · 南墙 | W2-05-4 | 墙角 1640 | 墙端（阳角） 900 | 1200 | WL4 | 键 9 → 后卫生间筒灯（套卫）；卫浴灯开关：D 墙卫浴门左边，中心离门洞边 100（业主 2026-10-09），h1200；门合页已换到右侧（凹位一端） |
| SM | 开关 · 智能马桶开关 | 次卧 | D · 南墙 | W2-01-4 | 墙角 154 | 墙端（阳角） 1536 | 1800 | 待定 | 卫浴门左侧墙段（门洞到墙角 434），中心离地 1800；两开关中心距 130，ST 离门洞边 150；控制卫浴内智能马桶 / 电热毛巾架（不装排风扇）；双极 FCU（建议 SM 13A、ST 3A），型号由电工定 |
| ST | 开关 · 电热毛巾架开关 | 次卧 | D · 南墙 | W2-01-4 | 墙角 284 | 墙端（阳角） 1406 | 1800 | 待定 | 卫浴门左侧墙段（门洞到墙角 434），中心离地 1800；两开关中心距 130，ST 离门洞边 150；控制卫浴内智能马桶 / 电热毛巾架（不装排风扇）；双极 FCU（建议 SM 13A、ST 3A），型号由电工定 |
| C01 | 插座 · 单联插座 Single socket | 衣帽间 | N · 东墙 | W2-03-10 | 墙角 1381 | 墙角 300 | 450 | WX8 | 450（英国规格，业主 2026-10-08；离 O 墙（门墙）墙角 300（业主 2026-10-09），h450 |
| C02 | 插座 · 双联插座 Twin socket | 二楼走廊 | A · 西墙 | W2-07-2 | 墙角 600 | 墙垛（凸出 100） 1098 | 450 | WX7 | 450（英国规格，业主 2026-10-08；从楼梯平台外墙 I 挪到 A 墙，中心离 I 墙墙角 600（业主 2026-10-09），h450 |
| C03 | 插座 · 双联插座 Twin socket | 主卧 | D · 南墙 | W2-03-5 | 墙角 1356 | 墙角 2789 | 650 | WX8 | 床头柜面 500 + 150（略高于柜面）；床头柜 F07 正中（业主 2026-10-09：床 1800，插座往外挪到床头柜上方），h650 |
| C04 | 插座 · 双联插座 Twin socket | 主卧 | D · 南墙 | W2-03-5 | 墙角 3720 | 墙角 425 | 650 | WX8 | 床头柜面 500 + 150（略高于柜面）；床头柜 F08 正中（业主 2026-10-09），h650 |
| C05 | 插座 · 双联插座 Twin socket | 主卧 | A · 西墙 | W2-03-2 | 墙角 2436 | 墙垛阳角（往北 414 段墙面凸出 75） 210 | 450 | WX8 | 450（英国规格，业主 2026-10-08；中心离窗洞边 150（往北，远离窗，业主确认）；原点位离窗洞边仅 32 |
| C06 | 插座 · 双联插座 Twin socket | 主卫 | H1 · 南墙 | W2-03-7 | 副门洞边 985 | 墙角 154 | 450 | WX8 | ⚠ 业主 2026-10-09：挪到 H1 墙（盥洗室侧，F25 洞口与墙角之间 307 宽墙段正中），h450；卫生间内插座按 BS 7671 请电工判定（可能需改剃须插座） |
| C07 | 插座 · 双联插座 Twin socket | 主卧 | C · 东墙 | W2-03-4 | 墙角 1580 | 墙角 1480 | 450 | WX8 | 450（英国规格，业主 2026-10-08；离房门洞边 450（业主 2026-10-09），h450 |
| C08 | 插座 · 双联插座 Twin socket | 主卧 | B · 北墙 | W2-03-3 | 墙角 1720 | 墙角 2350 | 450 | WX8 | 450（英国规格，业主 2026-10-08 |
| C09 | 插座 · 单联插座 Single socket | 衣帽间 | M · 北墙 | W2-03-9 | 墙角 849 | 墙角 849 | 450 | WX8 | 450（英国规格，业主 2026-10-08；M 墙正中（业主 2026-10-09），h450 |
| C10 | 插座 · 双联插座 Twin socket | 中间书房 | D · 南墙 | W2-04-3 | 墙角 684 | 墙角 1561 | 450 | WX6A | 书桌墙：由台面上方改到离地 450（书桌下方，业主 2026-10-09） |
| C11 | 插座 · 双联插座 Twin socket | 中间书房 | D · 南墙 | W2-04-3 | 墙角 1698 | 墙角 547 | 450 | WX6A | 书桌墙：由台面上方改到离地 450（书桌下方，业主 2026-10-09） |
| C12 | 插座 · 双联插座 Twin socket | 中间书房 | A · 西墙 | W2-04-2 | 墙角（南端墙面凸出 100 / 160 两级） 1239 | 墙角 853 | 450 | WX6A | 业主 2026-10-09：改双联；中心离门洞边约 200，h450 |
| C13 | 插座 · 双联插座 Twin socket | 中间书房 | B · 北墙 | W2-04-2 | 墙角 2105 | 墙角 300 | 450 | WX6A | 450（英国规格，业主 2026-10-08；中心离东墙角 300（业主 2026-10-09），h450 |
| C14 | 插座 · 空调插座 A/C socket | 后书房 | A · 西墙 | W2-05-2 | 墙角 2900 | 墙角 150 | 2300 | WP4 | 空调插座：中心离北墙角 150（业主 2026-10-09）；天花降到约 2600 后原 h2540 会碰顶角线，暂改 h2300 —— 按内机位置现场定；内机位置 / 是否保留待业主定 |
| C15 | 插座 · 双联插座 Twin socket | 后书房 | B · 北墙 | W2-05-3 | 墙角 1430 | 墙角 2160 | 450 | WX6 | 450（英国规格，业主 2026-10-08；大窗正中下方（业主 2026-10-09：多功能房，不放床时窗下可放书桌），h450 |
| C16 | 插座 · 双联插座 Twin socket | 后书房 | C · 东墙 | W2-05-3 | 墙角 1590 | 墙角 450 | 450 | WX6 | 业主 2026-10-09：从 D 墙挪到 C 墙（后墙），中心离 D 墙角约 450，h450；床（占位）贴 C 墙时在床侧，床定了再核 |
| C17 | 插座 · 双联插座 Twin socket | 后书房 | A · 西墙 | W2-05-2 | 墙角 2000 | 墙角 1050 | 450 | WX6 | 450（英国规格，业主 2026-10-08；中心离房门洞边 250（业主 2026-10-09），h450 |
| C18 | 插座 · 双联插座 Twin socket | 后书房 | B · 北墙 | W2-05-3 | 墙角 640 | 墙角 2950 | 450 | WX6 | 450（英国规格，业主 2026-10-08 |
| C19 | 插座 · 双联插座 Twin socket | 次卧 | H · 南墙 | W2-01-6 | 墙角 250 | 墙角 3298 | 650 | WX8 | 床头插座：中心离左墙角 250（业主 2026-10-08），高 650（同主卧，业主 2026-10-09） |
| C20 | 插座 · 双联插座 Twin socket | 次卧 | H · 南墙 | W2-01-6 | 墙角 3298 | 墙角 250 | 650 | WX7 | 床头插座：中心离右墙角 250（业主 2026-10-08），高 650（同主卧，业主 2026-10-09） |
| C21 | 插座 · 双联插座 Twin socket | 次卧 | A · 西墙 | W2-01-2 | 墙角 2110 | 墙角 1378 | 450 | WX7 | 450（英国规格，业主 2026-10-08 |
| C22 | 插座 · 双联插座 Twin socket | 次卧 | B · 北墙 | W2-01-3 | 墙角 3500 | 墙角 3608 | 450 | WX7 | 450（英国规格，业主 2026-10-08；中心距左侧墙角 3500，距右侧墙角 3608；离地 450；已移出衣柜占位范围 |
| C23 | 插座 · 双联插座 Twin socket | 次卧 | C · 东墙 | W2-01-4 | 墙角 640 | 墙角 838 | 450 | WX7 | 450（英国规格，业主 2026-10-08 |
| C24 | 插座 · 空调插座 A/C socket | 中间书房 | C · 东墙 | W2-04-3 | 墙角 1468 | 墙角 1582 | 2190 | WP3 | 空调内机侧面，与机身中高齐平（内机底 2040）；空调插座：与窗错开，中心离窗洞边 250（业主 2026-10-09），h2190；在空调内机范围内，现场按内机接线位置核对 |
| C25 | 插座 · 单联插座 Single socket | 次卧 | E · 东墙 | W2-01-4 | 墙端（阳角） 210 | 墙角 590 | 450 | WX7 | 450（英国规格，业主 2026-10-08；数据里房间写「电梯」，按位置在次卧入口 E 墙（次卧一侧） |
| C26 | 插座 · 双联插座 Twin socket | 中间书房 | C · 东墙 | W2-04-3 | 墙角 1650 | 墙角 1400 | 450 | WX6A | 450（英国规格，业主 2026-10-08 |
| C27 | 插座 · 双联插座 Twin socket（新增） | 二楼走廊 | H · 北墙 | W2-07-6 | 墙端（靠 G 墙） 500 | 后书房门口（下行台阶尽头） 1972 | 450 | 待定 | 新增（业主 2026-10-09）：大概位置，中心离 H 墙左端（靠 G 墙）约 500，上完楼梯顺手处；如有必要可改放在 S11 正下方；h450 |
| FS | 专用 / FCU / 新增 · 排风扇开关 Extract fan switch（卫浴） | 后书房 | D · 南墙 | W2-05-4 | 墙角 1640 | 墙端（阳角） 900 | 1800 | 待定 | 排风扇开关：与 S14 同一竖线，h1800（业主 2026-10-09）；排风扇本体按产品定 |
| N-TR1 | 专用 / FCU / 新增 · 主卫电热毛巾架出线面板（新增） | 主卫 | H2 · 南墙 | W2-03-7 | 墙角（假墙） 420 | 副门洞边 602 | 1100 | WX8 | 毛巾架下沿旁出线面板（模型位置），FCU 13A 装在卫生间外 h 1100；毛巾架下沿旁出线面板（非插座），FCU 在卫生间外 |
| N-TR2 | 专用 / FCU / 新增 · 电热毛巾架出线口 | 次卧完整卫浴 | C · 东墙 | W2-02-3 | 墙角 1568 | 墙角 342 | 1400 | WX7 | 在毛巾架 F31 正中、底边（1300）上方 100，被毛巾架挡住（同主卫做法）；由门边 ST 供电；出线面板（非插座），IPX4 |
| N-WC1 | 专用 / FCU / 新增 · 主卫智能马桶电源出线面板（新增） | 主卫 | I · 东墙 | W2-03-7 | 墙角 1590 | 墙角 91 | 300 | WX8 | 马桶侧后方出线面板 h 300，FCU 13A 装在卫生间外开关旁 h 1100；马桶旁出线面板（非插座），FCU 在卫生间外；面板防护 ≥ IPX4 |

| | |
|---|---|
| 项目 Project | 27PR 住宅改造 · 27 Penrith Road |
| 图名 Title | 二层墙面点位定位表（插座 / 开关 / 专用 / 壁灯） |
| 图号 Sheet | SO-08 比例 — @A3 |
| 专业 Discipline | 电气定位 Setting out |
| 版次 Rev | C · 2026-10-14 · 施工图（待持证电工 / 水工复核） |

# 二层墙面点位定位表（插座 / 开关 / 专用 / 壁灯）

**二层墙面点位定位表（插座 / 开关 / 专用 / 壁灯）（尺寸 mm；左 / 右端 = 面对墙看的左 / 右；高度 = 底盒中心离本房间完成地面；按立面图号放线）**

| 编号 | 类型 / 名称 | 房间 | 墙面 | 立面图号（见 SO-03 / 04） | 左端 mm | 右端 mm | 高度 | 回路 | 备注（立面图） |
|---|---|---|---|---|---|---|---|---|---|
| N-WC2 | 专用 / FCU / 新增 · 智能马桶出线口 | 次卧完整卫浴 | C · 东墙 | W2-02-3 | 墙角 1760 | 墙角 150 | 400 | WX7 | 马桶后面右侧，被马桶挡住；出线面板（非插座）IPX4；由门上 SM 供电；按马桶说明书核对进线位置 |
| SF | 专用 / FCU / 新增 · 排风扇开关（风扇隔离开关） | 主卧 | B · 北墙 | W2-03-3 | 墙角 1430 | 墙角 2640 | 450 | 待定 | 本房间 B 墙，主卫入口 F25 洞口右边，一排三个（中心距 130，离地 450；业主 2026-10-09 从主卫 G 墙挪出）；主卫排风扇；风扇位置 / 型号现场定 |
| SM | 专用 / FCU / 新增 · 智能马桶盖开关（带开关 FCU） | 主卧 | B · 北墙 | W2-03-3 | 墙角 1170 | 墙角 2900 | 450 | FCU→N-WC1 | 本房间 B 墙，主卫入口 F25 洞口右边，一排三个（中心距 130，离地 450；业主 2026-10-09 从主卫 G 墙挪出）；供主卫 N-WC1 出线面板 |
| ST | 专用 / FCU / 新增 · 电热毛巾架开关（带开关 FCU） | 主卧 | B · 北墙 | W2-03-3 | 墙角 1300 | 墙角 2770 | 450 | FCU→N-TR1 | 本房间 B 墙，主卫入口 F25 洞口右边，一排三个（中心距 130，离地 450；业主 2026-10-09 从主卫 G 墙挪出）；供主卫 N-TR1 出线面板 |
| TH | 专用 / FCU / 新增 · 地暖温控面板 UFH thermostat | 中间书房 | A · 西墙 | W2-04-2 | 墙角（南端墙面凸出 100 / 160 两级） 1346 | 墙角 746 | 1200 | 待定 | S10 右侧同高，中心距 150（业主 2026-10-09）；有线温控需穿线到地暖分水器接线中心，无线温控也按此位置留底盒；型号由地暖供应商定 |
| TH | 专用 / FCU / 新增 · 地暖温控面板 UFH thermostat | 主卧 | B · 北墙 | W2-03-3 | 墙角 3870 | 墙角 200 | 1050 | 待定 | S5 正下方，中心距 150（业主 2026-10-09 挪到 B 墙）；有线温控需穿线到地暖分水器接线中心，无线温控也按此位置留底盒；型号由地暖供应商定 |
| TH | 专用 / FCU / 新增 · 地暖温控面板 UFH thermostat | 后书房 | A · 西墙 | W2-05-2 | 墙角 2050 | 墙角 1000 | 1200 | 待定 | S13 右侧同高，中心距 150（业主 2026-10-09）；有线温控需穿线到地暖分水器接线中心，无线温控也按此位置留底盒；型号由地暖供应商定 |
| TH | 专用 / FCU / 新增 · 地暖温控面板 UFH thermostat | 次卧 | G · 东墙 | W2-01-5 | 门洞边 300 | 墙角 910 | 1200 | 待定 | S4 右侧同高，中心距 S4 150；有线温控需穿线到地暖分水器接线中心，无线温控也按此位置留底盒；型号由地暖供应商定 |
| SH1 | 给排水点 · 恒温淋浴杆阀 Thermostatic bar valve | 主卫 | I · 东墙 | W2-03-7 | 墙角 519 | 墙角 1162 | 1050 | 冷 / 热 | 冷 / 热 150 c/c，明装；两个壁龛中间（P-07） |
| SH1-H | 给排水点 · 顶喷 Ø250 Rain head | 主卫 | I · 东墙 | W2-03-7 | 墙角 519 | 墙角 1162 | 1975 | 冷 / 热 | 顶喷中心离地约 1975，带滑杆手持（P-07） |

| | |
|---|---|
| 项目 Project | 27PR 住宅改造 · 27 Penrith Road |
| 图名 Title | 二层墙面点位定位表（插座 / 开关 / 专用 / 壁灯） |
| 图号 Sheet | SO-09 比例 — @A3 |
| 专业 Discipline | 电气定位 Setting out |
| 版次 Rev | C · 2026-10-14 · 施工图（待持证电工 / 水工复核） |

# 二层天花灯位 / 其他点位定位表

**二层天花灯位 / 其他点位定位表（尺寸 mm；左 / 右端 = 面对墙看的左 / 右；高度 = 底盒中心离本房间完成地面；按立面图号放线）**

| 编号 | 类型 / 名称 | 房间 | 天花图号（见 SO-03 / 04） | 南北向：距墙 | 东西向：距墙 | 天花高 | 回路 | 开关 / 备注 |
|---|---|---|---|---|---|---|---|---|
| L01 | 灯 · 主灯 F06 | 二楼走廊 | W2-07-1 | 北 1180 / 南 530 | 西 2940 / 东 560 | 2700 | WL4 | S11 键 17 / S12 键 7 |
| L02 | 灯 · 主灯 F11 | 二楼走廊 | W2-07-1 | 北 3880 / 南 2290 | 西 470 / 东 620 | 2700 | WL4 | S8 键 3 / S11 键 16 |
| L03 | 灯 · 主灯 F19 | 次卧 | W2-01-1 | 北 1250 / 南 2240 | 西 2130 / 东 4980 | 2500 | WL4 | S3 键 2 / S4 键 10 |
| L04 | 灯 · 主灯 F20 | 主卧 | W2-03-1 | 北 1120 / 南 1940 | 西 1600 / 东 2540 | 2700 | WL4 | S6 键 12 / S7 键 14 |
| L05 | 灯 · 主灯 F22 | 中间书房 | W2-04-1 | 北 1520 / 南 1530 | 西 1230 / 东 1180 | 2700 | WL4 | S10 键 4 |
| L06 | 灯 · 主灯 F23 | 后书房 | W2-05-1 | 北 1060 / 南 980 | 西 1630 / 东 1960 | 2600 | WL4 | S13 键 8 |
| L07 | 灯 · GU10 筒灯 | 次卧完整卫浴 | W2-02-1 | 北 630 / 南 1280 | 西 920 / 东 670 | 2500 | WL4 | S9 键 1 |
| L08 | 灯 · GU10 筒灯 | 后房窄卫浴 | W2-06-1 | 北 460 / 南 460 | 西 970 / 东 1470 | 2600 | WL4 | S14 键 9 |
| L09 | 灯 · GU10 筒灯 | 主卫 | W2-03-1 | 北 880 / 南 800 | 西 550 / 东 450 | 2700 | WL4 | S1 键 6 |
| L10 | 灯 · GU10 筒灯 | 主卧 | W2-03-1 | 北 1900 / 南 1160 | 西 3360 / 东 780 | 2700 | WL4 | S6 键 13 / S7 键 15 |
| L11 | 灯 · 主灯位（灯具待选） | 次卧 | W2-01-1 | 北 1200 / 南 1080 | 西 4750 / 东 2360 | 2500 | WL4 | S4 键 11 |
| L12 | 灯 · GU10 筒灯 | 次卧 | W2-01-1 | 北 1200 / 南 1080 | 西 4750 / 东 2350 | 2500 | WL4 | S2 键 6+ |
| L12 | 灯 · GU10 筒灯 | 主卫 | W2-03-1 | 北 1260 / 南 420 | 西 1510 / 东 650 | 2700 | WL4 | S2 键 6+ |
| L13 | 灯 · 主灯 衣帽间 | 主卫 | W2-03-1 | 北 1260 / 南 420 | 西 1510 / 东 650 | 2700 | WL4 | S5 键 5 |
| L13 | 灯 · 主灯 衣帽间 | 衣帽间 | W2-03-1 | 北 950 / 南 730 | 西 930 / 东 770 | 2700 | WL4 | S5 键 5 |
| L14 | 灯 · 主灯 F11#2 | 二楼走廊 | W2-07-1 | 北 1780 / 南 4390 | 西 440 / 东 490 | 2700 | WL4 | S8 键 3 / S11 键 16 |
| L14 | 灯 · 吸顶灯（取代原 L10 + L14 两个筒灯） | 衣帽间 | W2-03-1 | 北 950 / 南 730 | 西 930 / 东 770 | 2700 | WL4 | S8 键 3 / S11 键 16 |
| SD1 | 烟感 · 烟雾报警器 Smoke alarm（楼梯平台天花；联网 / 电源按 BS 5839-6 由电工定） | 二楼走廊 | W2-07-1 | 北 4960 / 南 1210 | 西 590 / 东 2910 | 2700 | | |

| | |
|---|---|
| 项目 Project | 27PR 住宅改造 · 27 Penrith Road |
| 图名 Title | 二层天花灯位 / 其他点位定位表 |
| 图号 Sheet | SO-10 比例 — @A3 |
| 专业 Discipline | 电气定位 Setting out |
| 版次 Rev | C · 2026-10-14 · 施工图（待持证电工 / 水工复核） |