

点位定位尺寸图 说明 Setting-out notes

怎么读这套图

- 每个点位有编号：C 插座、D 专用电器 / FCU / 隔离开关、S 开关、L 灯、N 新增。编号前的 1 / 2 表示一层 / 二层（表里另列楼层）。
- 墙面名称按「站在房间里看这面墙」：北墙 / 南墙 / 西墙 / 东墙（前门朝西、后花园在东）。
- 水平尺寸：从这面墙「左端」量到点位中心（面对墙看的左边边），同时给出到右端的距离，两个数加起来 = 这面墙的净长，可用来核对。
左 / 右端是什么也写出来了：墙角（阴角） / 门洞边 / 窗洞边 / 墙端（阳角）。量的是完成墙面，抹灰 / 石膏板后的面。
- 高度：从该房间完成地面量到底盒中心（灯为天花高度）。二层前部完成面 3.208、后部（卧室 4 / 后卫 / 书房二）2.852，各自从本房间地面起量。
- 天花板上的灯：给出到两个方向最近墙面（或门窗洞）的距离。
- 立面图（SO-1x）：每面有点位的墙一张，平面图上的 1E05 / 2E12 等就是立面编号，箭头指向被看的那面墙。

高度标准（底盒中心，离本房间完成地面）

项	高度 mm	依据
开关（全部）	1200	原施工图 / 模型 v42；Part M 450–1200。叠放的开关（S5 在 S4 上方）中心再高 130
一般插座	300	业主原定，与模型一致
床头插座 / 床头开关	630 / 650 / 700	床头柜面（主卧 485、卧室 2 500，模型 v42）+ 约 150；主卧 S3 在床头柜上方 700
厨房台面插座 / FCU	1100	台面 902（模型）上方，底边离台面约 150；FCU 同高、装在可触及处
餐边柜 / 洗衣柜 / 书桌上方	1110 / 1200 / 970	柜面或桌面（907 / 1002 / 766）+ 200
电视柜上方插座	600	原位置被电视柜（高 452）挡住，抬到柜面上方
空调插座	2190 / 2540	在内机侧面，与机身中高齐平（内机底：卧室 3 2040、卧室 4 2390，模型 v42）
户外插座	600	户外 IP66 带盖
EV 充电桩 / 室内 40A 总控	1000 / 1200	按充电桩说明书；隔离开关 1200
壁灯	按模型	楼梯壁灯 F32 1930；后花园壁灯 1770–1800；投光灯 3350（模型 v42 灯具中心）

图例

插座

专用 / FCU

开关

灯

给排水点

新增

精度与误差（重要）

- 点位来源：照明 / 插座设计（网页工具 Rev J、PPT 标注）+ Blender 模型 v42 的墙体、门窗、家具。图上点位标在墙边，本稿已把每个点「推」到所属墙面，再从墙端量尺寸，取整到 10 mm。
- 估计误差：插座 / 开关 / 灯水平位置 ±30 mm（原标注是示意位置）；表中「原点离墙面 xxx」= 原图标记离墙较远，已按墙面定位，请重点确认这些点在哪一面墙。
- 高度为设计值，按本图施工；家具、洁具定版后若尺寸变化，床头 / 台面 / 洁具相关点位跟着调整。墙体以现场完成面为准，与图差 > 50 mm 时先停工联系业主。
- 「离墙角 / 洞口 < 100」的点：贴得太近，门框 / 踢脚线 / 墙角可能装不下底盒，现场定位时请移到 ≥ 150。


核对后的处理（业主 2026-10-08 定稿）

- 高度：开关 1200、普通插座 300（与原施工图 / 模型一致）；床头插座 = 床头柜面 + 150，台面插座离台面约 150；S5 叠在 S4 正上方（1330）。
- 智能马桶 / 电热毛巾架电源：西卫 N-WC1、N-TR1；北卫马桶 + 毛巾架共用 N-TR2 双联出线面板（毛巾架挪到马桶旁后墙）。FCU 13A 都装在卫生间门外开关旁。
- 一层 C02 / C15 / C21 / C25 / C27 / C28 / C34 / S3 按模型位置（业主 2026-10-01 现场定）。
- 二层 S3（主卧主灯，与门口 S4 双控）：放在 C19 一侧床头柜上方 700，避开床头板。
- 被家具挡住的插座已挪开：电视柜后抬到 600；沙发、衣架、床、梳妆台、矮柜后的挪到家具外侧 150。
- 一层客厅 / 起居室之间的沙发墙已按模型 v42 补齐。

项目 Project	27PR 住宅改造 · 27 Penrith Road
图名 Title	点位定位尺寸图 说明 Setting-out notes
图号 Sheet	SO-00 比例 — @A3
专业 Discipline	电气定位 Setting out
版次 Rev	A · 2026-10-08 · 施工图（待持证电工 / 水工复核）

一层点位定位总平面 Setting-out plan

0 2 m

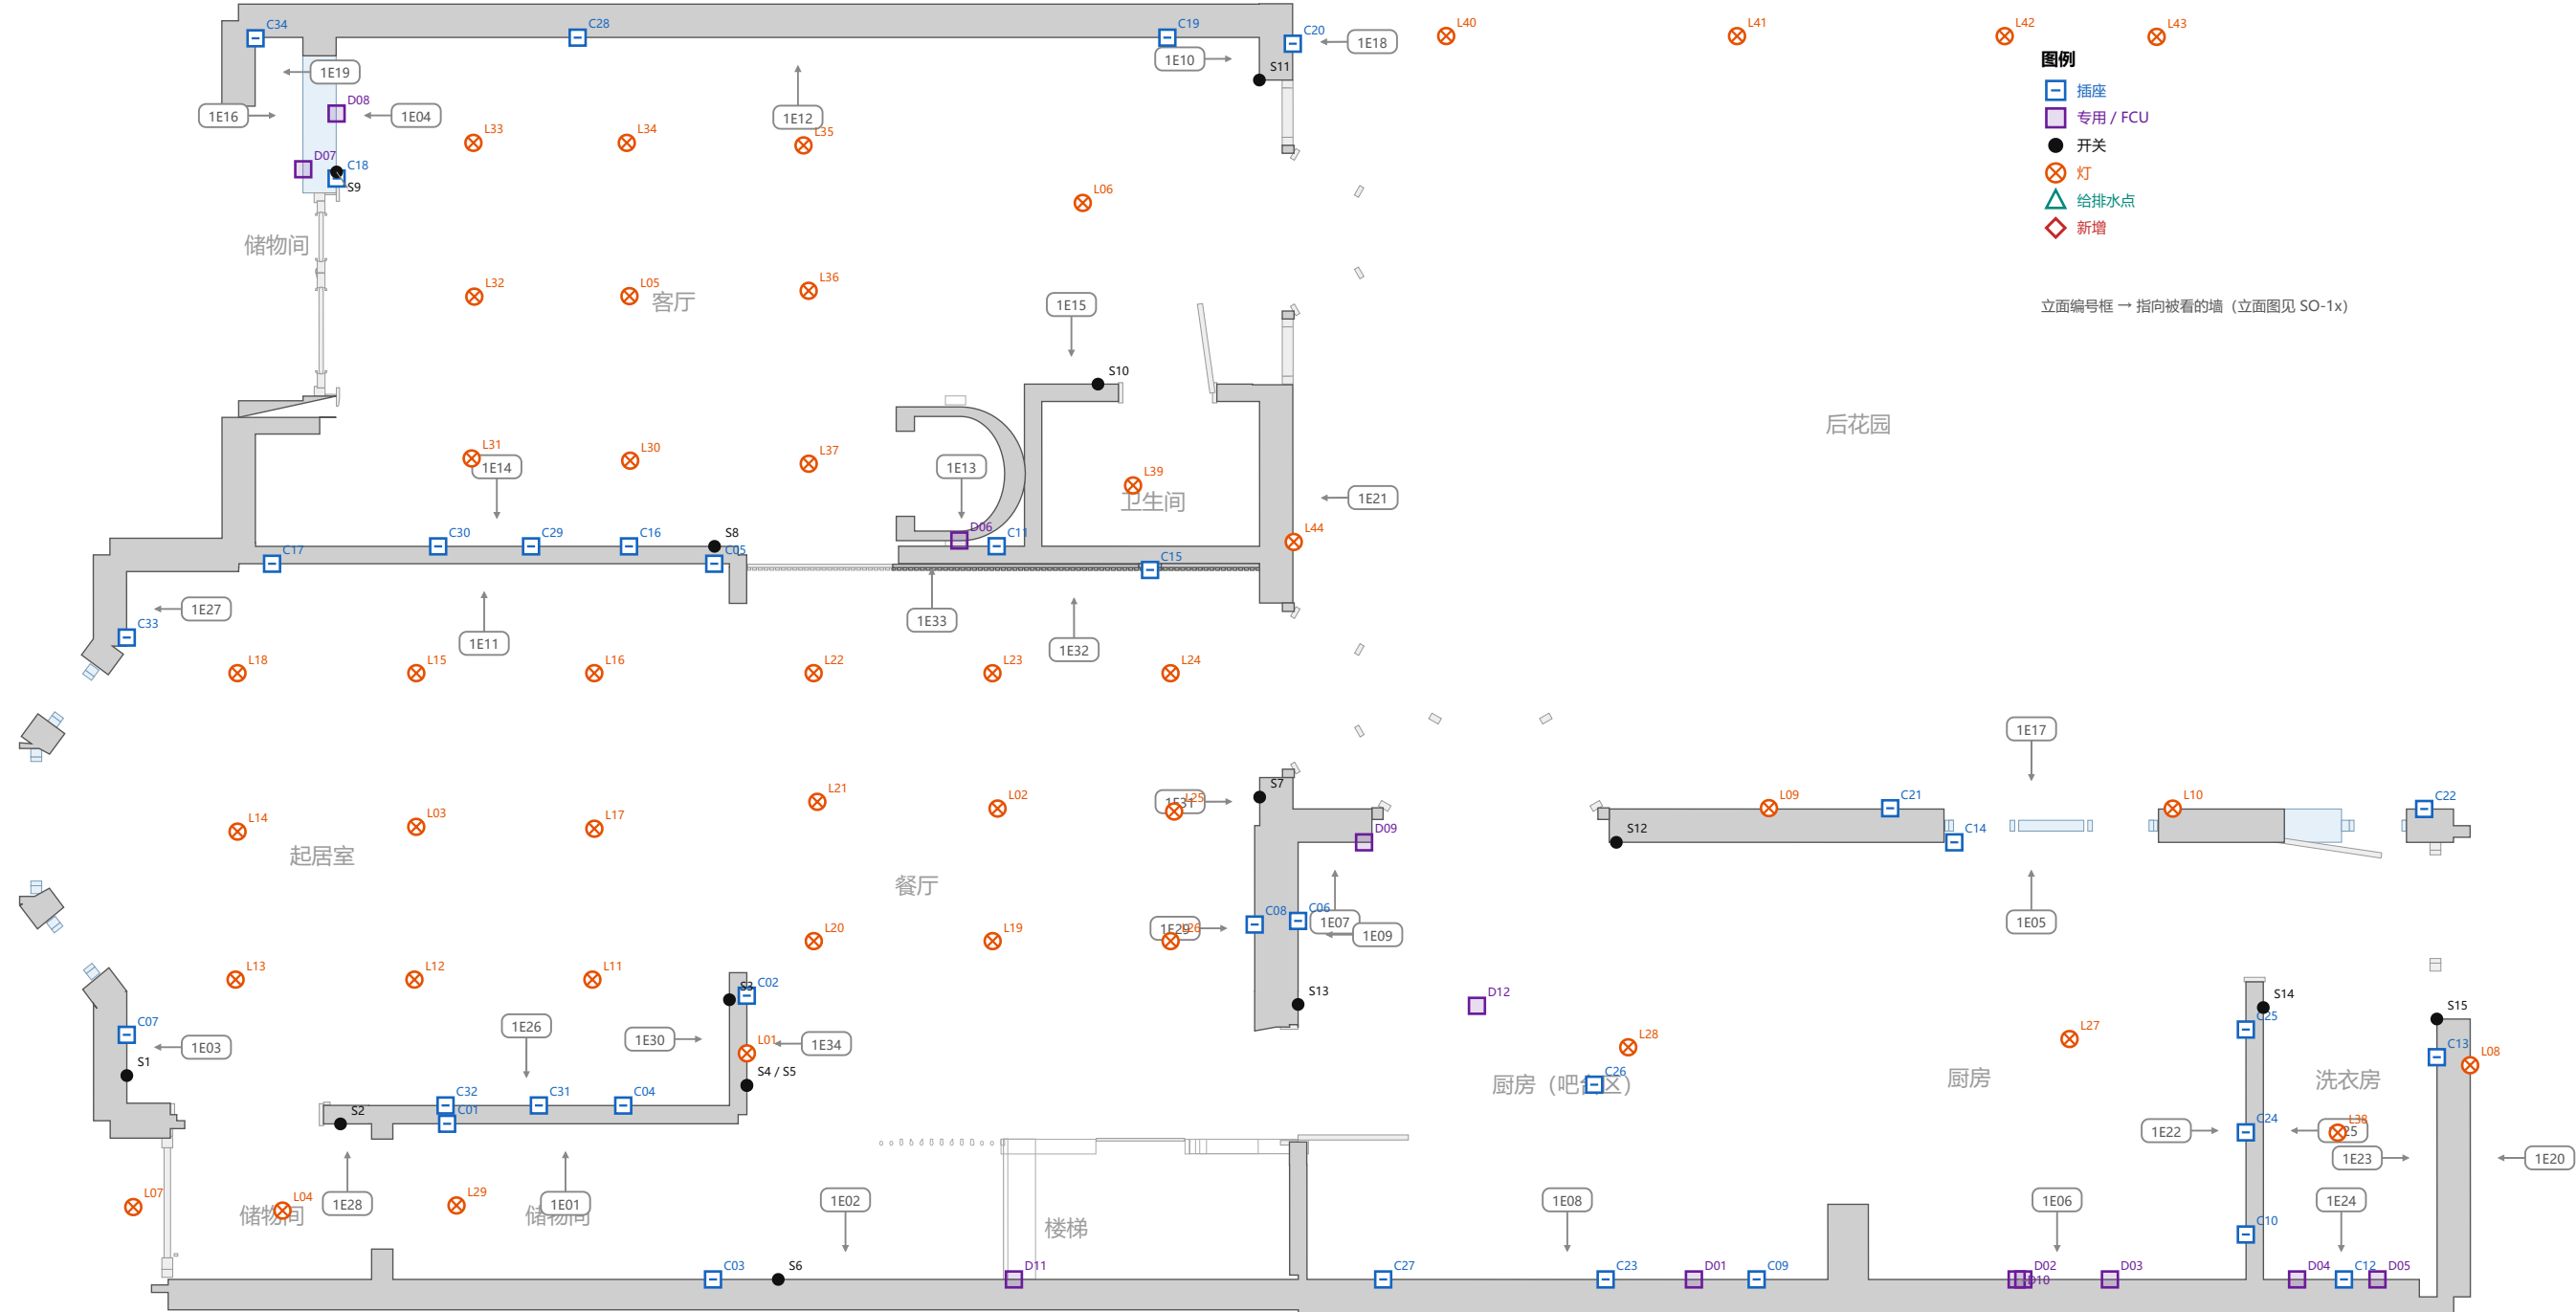

图例

- 插座
- 专用 / FCU
- 开关
- 灯
- 给排水点
- 新增



立面编号框 → 指向被看的墙 (立面图见 SO-1x)

说明 Notes

- 点位已推到所属墙面 (平面上的位置 = 墙面位置) ; 尺寸见定位表和立面图。
- 高度标准见 SO-00; 开关 1200、一般插座 300、床头 630 / 650、台面上方 1100。
- 给排水点位见给排水施工图。

项目 Project	27PR 住宅改造 · 27 Penrith Road
图名 Title	一层点位定位总平面 Setting-out plan
图号 Sheet	SO-01 比例 1:50 @A3
专业 Discipline	电气定位 Setting out
版次 Rev	A · 2026-10-08 · 施工图 (待持证电工 / 水工复核)

二层点位定位总平面 Setting-out plan

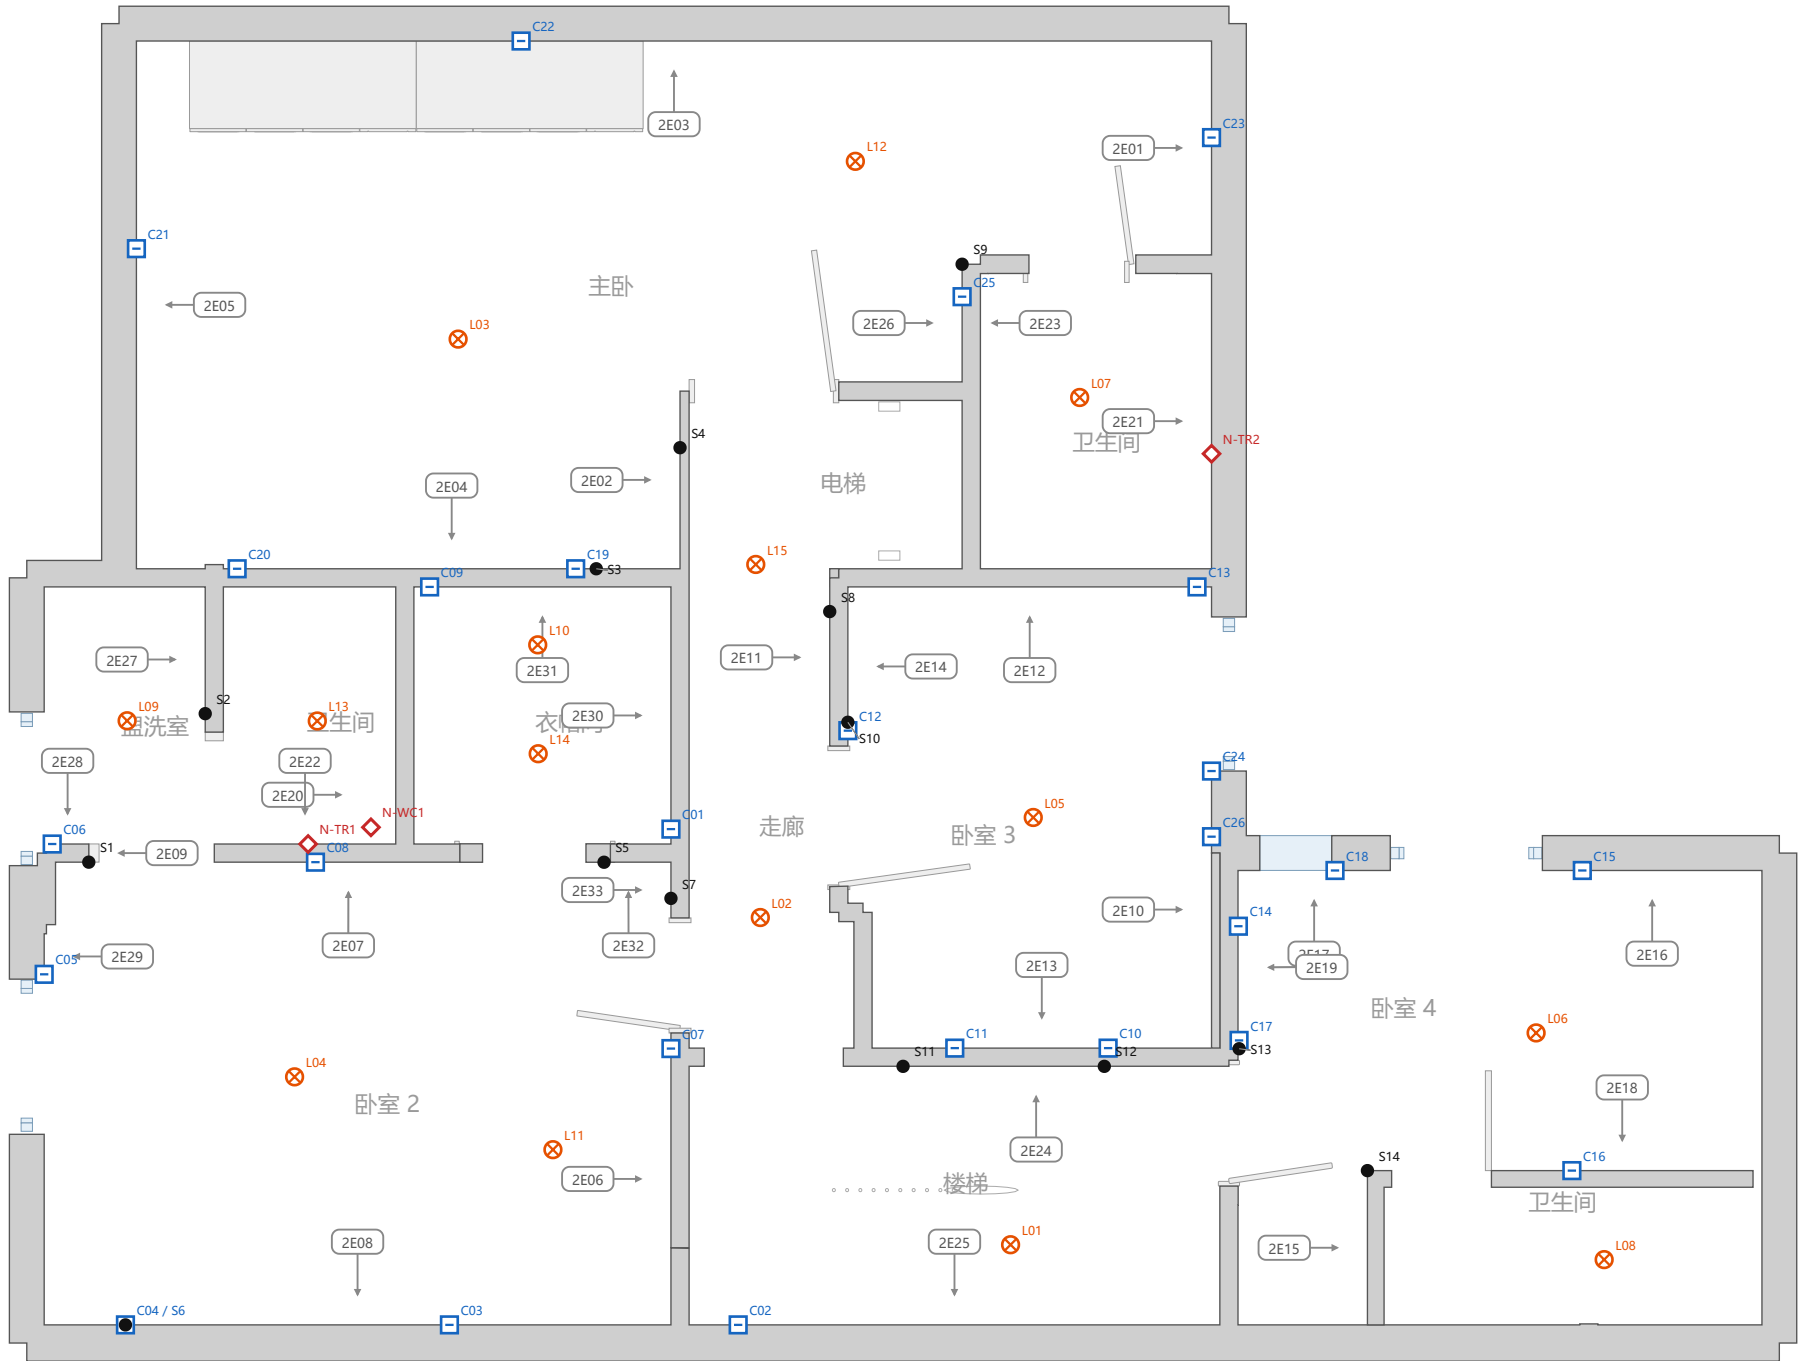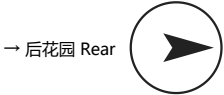

图例

- 插座
- 专用 / FCU
- 开关
- 灯
- 给排水点
- 新增

立面编号框 → 指向被看的墙（立面图见 SO-1x）

说明 Notes

- 点位已推到所属墙面（平面上的位置 = 墙面位置）；尺寸见定位表和立面图。
- 高度标准见 SO-00；开关 1200、一般插座 300、床头 630 / 650、台面上方 1100。
- 给排水点位见给排水施工图。

项目 Project	27PR 住宅改造 · 27 Penrith Road
图名 Title	二层点位定位总平面 Setting-out plan
图号 Sheet	SO-02 比例 1:50 @A3
专业 Discipline	电气定位 Setting out
版次 Rev	A · 2026-10-08 · 施工图（待持证电工 / 水工复核）

一层墙面点位定位表（插座 / 开关 / 专用 / 壁灯）

一层墙面点位定位表（插座 / 开关 / 专用 / 壁灯）（尺寸 mm；距左 / 右端 = 面对墙看的左 / 右；高度 = 底盒中心离本房间完成地面）

编号	类型 / 名称	房间	墙面（立面）	距左端 mm	距右端 mm	高度	依据 / 备注
S1	开关 · 4 联开关 · 键 3/4/5/6	门厅 · 前门内侧	西墙（1E03）	墙角 190	窗洞边 580	1200	开关中心 1100
S2	开关 · 2 联开关 · 键 1/2	门厅 · 前储物间旁	北墙（1E28）	门洞边 120	墙角 210	1200	开关中心 1100
S3	开关 · 3 联开关 · 键 23/24/25	起居室侧 · 拱门旁	东墙（1E30）	墙端 190	墙角 730	1200	开关中心 1100
S4	开关 · 4 联开关 · 键 18/19/20/21	楼梯口 · 拱门旁（与 S5 上下叠放，S4 在下）	西墙（1E34）	墙端 200	墙端 780	1200	开关中心 1100
S5	开关 · 3 联开关 · 键 7/8/9（叠在 S4 正上方）	G07 区侧 · 拱门旁（叠在 S4 正上方）	西墙（1E34）	墙端 200	墙端 780	1330	开关中心 1100
S6	开关 · 1 联开关 · 键 30	楼梯底	南墙（1E02）	墙角 3590	墙角 2660	1200	开关中心 1100
S7	开关 · 3 联开关 · 键 26/27/28	法式门框东侧（后花园门旁）	东墙（1E31）	墙端 130	墙角 200	1200	开关中心 1100
S8	开关 · 4 联开关 · 键 10/11/12/13	G15 区南门旁	南墙（1E14）	墙端 160	墙角 3170	1200	开关中心 1100；原点离离墙面 290，已按墙面定位
S9	开关 · 4 联开关 · 键 14/15/16/17	G15 区 · 储物间门旁	西墙（1E04）	门洞边 150	墙角 930	1200	开关中心 1100
S10	开关 · 1 联开关 · 键 22	卫生间门外	南墙（1E15）	门洞边 140	墙端 510	1200	开关中心 1100
S11	开关 · 3 联开关 · 键 26/27/28	G15 区 · 通后花园门旁	东墙（1E10）	墙角 290	墙端 0	1200	开关中心 1100；离墙角 / 洞口 < 100，现场确认
S12	开关 · 3 联开关 · 键 26/27/28	厨房后门旁（吧台区）	北墙（1E05）	墙端 50	门洞边 5790	1200	开关中心 1100；原点离离墙面 250，已按墙面定位；离墙角 / 洞口 < 100，现场确认
S13	开关 · 2 联开关 · 键 31/32	厨房入口	西墙（1E09）	门洞边 160	墙角 1120	1200	开关中心 1100；原点离离墙面 290，已按墙面定位
S14	开关 · 1 联开关 · 键 38	洗衣房门旁	西墙（1E25）	墙角 1880	门洞边 180	1200	开关中心 1100
S15	开关 · 1 联开关 · 键 40	洗衣房后门旁	东墙（1E23）	墙端 0	墙角 1920	1200	开关中心 1100；原点离离墙面 250，已按墙面定位；离墙角 / 洞口 < 100，现场确认
C01	插座 · 单联插座	储物间	北墙（1E01）	墙角 380	墙端 2010	300	300（业主原定，与模型一致）
C02	插座 · 单联插座	餐厅	西墙（1E34）	墙端 820	墙端 160	300	300（业主原定，与模型一致）；位置按模型（业主现场定）
C03	插座 · 双联插座	储物间	南墙（1E02）	墙角 4040	墙角 2210	300	300（业主原定，与模型一致）
C04	插座 · 双联插座	起居室	南墙（1E26）	墙角 730	门洞边 2070	600	电视柜上方 600（原位置被电视柜挡住）
C05	插座 · 双联插座	客厅	北墙（1E11）	墙角 3290	墙角 100	300	300（业主原定，与模型一致）；已挪到家具外侧（原位置被家具挡住）；在 G09（高 900）后面会被挡住，建议移到侧边或抬高
C06	插座 · 双联插座	厨房（吧台区）	西墙（1E09）	门洞边 730	墙角 540	300	300（业主原定，与模型一致）；原点离离墙面 320，已按墙面定位
C07	插座 · 双联插座	储物间	西墙（1E03）	墙角 470	窗洞边 300	300	300（业主原定，与模型一致）
C08	插座 · 双联插座	餐厅	东墙（1E29）	墙端 680	墙端 740	300	300（业主原定，与模型一致）；原点离离墙面 350，已按墙面定位
C09	插座 · 双联插座	厨房（吧台区）	南墙（1E08）	墙角 490	墙角 3110	1100	台面 900 上方（底边离台面约 150）
C10	插座 · 双联插座	洗衣房	东墙（1E22）	门洞边 1750	墙角 310	1100	台面 900 上方（底边离台面约 150）
C11	插座 · 单联插座	客厅	南墙（1E13）	墙角 190	墙端 680	300	300（业主原定，与模型一致）
C12	插座 · 双联插座	洗衣房	南墙（1E24）	墙端 520	墙角 560	1200	台面 1000 上方（底边离台面约 150）
C13	插座 · 双联插座	洗衣房	东墙（1E23）	墙端 260	墙角 1660	300	300（业主原定，与模型一致）
C14	插座 · 双联插座	厨房	北墙（1E05）	墙端 2390	门洞边 3450	300	300（业主原定，与模型一致）
C15	插座 · 双联插座	餐厅	北墙（1E32）	门洞边 1780	墙端 730	300	300（业主原定，与模型一致）；位置按模型（业主现场定）
C16	插座 · 双联插座	客厅	南墙（1E14）	墙端 750	墙角 2580	600	电视柜上方 600（原位置被电视柜挡住）
C17	插座 · 双联插座	起居室	北墙（1E11）	墙角 230	墙角 3160	1110	台面 910 上方（底边离台面约 150）
C18	插座 · 双联插座	储物间	西墙（1E04）	门洞边 100	墙角 970	300	300（业主原定，与模型一致）；已挪到家具外侧（原位置被家具挡住）
C19	插座 · 双联插座	客厅	北墙（1E12）	墙角 5740	墙角 640	300	300（业主原定，与模型一致）
C20	插座 · 户外防水插座 IP66	户外	西墙（1E18）	门洞边 250	墙端 280	600	户外 600，防水盖朝下；原点离离墙面 330，已按墙面定位
C21	插座 · 户外防水插座 IP66	户外	南墙（1E17）	墙端 3890	门洞边 1940	600	户外 600，防水盖朝下；位置按模型（业主现场定）
C22	插座 · 户外防水插座 IP66	户外	南墙（1E17）	墙端 200	门洞边 5630	600	户外 600，防水盖朝下
C23	插座 · 双联插座	厨房（吧台区）	南墙（1E08）	墙角 1530	墙角 2060	1100	台面 900 上方（底边离台面约 150）
C24	插座 · 双联插座	洗衣房	东墙（1E22）	门洞边 1040	墙角 1020	1100	台面 900 上方（底边离台面约 150）
C25	插座 · 双联插座	洗衣房	东墙（1E22）	门洞边 330	墙角 1730	300	300（业主原定，与模型一致）；位置按模型（业主现场定）
C27	插座 · 双联插座	厨房（吧台区）	南墙（1E08）	墙角 3070	墙角 530	300	300（业主原定，与模型一致）；位置按模型（业主现场定）
C28	插座 · 双联插座	客厅	北墙（1E12）	墙角 1670	墙角 4710	300	300（业主原定，与模型一致）；位置按模型（业主现场定）；在 G14（高 850）后面会被挡住，建议移到侧边或抬高
C29	插座 · 双联插座	客厅	南墙（1E14）	墙端 1430	墙角 1900	600	电视柜上方 600（原位置被电视柜挡住）
C30	插座 · 双联插座	储物间	南墙（1E14）	墙端 2070	墙角 1260	600	电视柜上方 600（原位置被电视柜挡住）
C31	插座 · 双联插座	起居室	南墙（1E26）	墙角 1320	门洞边 1490	600	电视柜上方 600（原位置被电视柜挡住）
C32	插座 · 双联插座	起居室	南墙（1E26）	墙角 1960	门洞边 840	600	电视柜上方 600（原位置被电视柜挡住）
C33	插座 · 双联插座	起居室	西墙（1E27）	窗洞边 60	墙角 450	1110	台面 910 上方（底边离台面约 150）；离墙角 / 洞口 < 100，现场确认
C34	插座 · 户外防水插座 IP66	户外	西墙（1E19）	墙端 470	墙角 0	600	户外 600，防水盖朝下；位置按模型（业主现场定）；离墙角 / 洞口 < 100，现场确认
D01	专用 / FCU · FCU 13A · 洗碗机	厨房（吧台区）	南墙（1E08）	墙角 920	墙端 2670	1100	FCU 装在台面上方 / 相邻柜内可触及处
D02	专用 / FCU · FCU 13A · 烤箱	厨房	南墙（1E06）	墙角 1540	墙角 1070	1100	FCU 装在台面上方 / 相邻柜内可触及处
D03	专用 / FCU · FCU 13A · 冰箱	厨房	南墙（1E06）	墙角 940	墙角 1670	1100	FCU 装在台面上方 / 相邻柜内可触及处
D04	专用 / FCU · FCU 13A · 洗衣机	洗衣房	南墙（1E24）	墙端 840	墙角 230	1100	FCU 装在台面上方 / 相邻柜内可触及处
D05	专用 / FCU · FCU 13A · 烘干机	洗衣房	南墙（1E24）	墙端 290	墙角 790	1100	FCU 装在台面上方 / 相邻柜内可触及处
D06	专用 / FCU · DP · 电梯	餐厅	北墙（1E33）	墙端 440	墙端 50	1200	电梯隔离开关，位置 / 高度以厂家为准；位置按模型（业主现场定）

项目 Project	27PR 住宅改造 · 27 Penrith Road
图名 Title	一层墙面点位定位表（插座 / 开关 / 专用 / 壁灯）
图号 Sheet	SO-03 比例 — @A3
专业 Discipline	电气定位 Setting out
版次 Rev	A · 2026-10-08 · 施工图（待持证电工 / 水工复核）

一层墙面点位定位表（插座 / 开关 / 专用 / 壁灯）

一层墙面点位定位表（插座 / 开关 / 专用 / 壁灯）（尺寸 mm；距左 / 右端 = 面对墙看的左 / 右；高度 = 底盒中心离本房间完成地面）

编号	类型 / 名称	房间	墙面（立面）	距左端 mm	距右端 mm	高度	依据 / 备注
D07	专用 / FCU · EV 充电桩（外墙）	户外	东墙（1E16）	墙角 910	门洞边 170	1000	充电桩底座约 1000（按产品说明书）
D08	专用 / FCU · DP 40A · 充电桩总控	客厅	西墙（1E04）	门洞边 550	墙角 520	1200	40A 双极隔离开关（充电桩室内总控）；位置按模型（业主现场定）
D09	专用 / FCU · FCU 13A · 锅炉 + 软水机	厨房（吧台区）	北墙（1E07）	墙角 460	墙端 50	1100	FCU 装在台面上方 / 相邻柜内可触及处
D10	专用 / FCU · FCU 13A · 抽油烟机高位插座	厨房	南墙（1E06）	墙角 1580	墙角 1020	1100	FCU 装在台面上方 / 相邻柜内可触及处
D11	专用 / FCU · FCU 13A · 地暖分水器 UF1 接线中心 + 混水泵	楼梯	南墙（1E02）	墙角 1960	墙角 4290	1100	FCU 装在台面上方 / 相邻柜内可触及处；原点位离墙面 590，已按墙面定位
D12	专用 / FCU · DP · 电梯	厨房（吧台区）	—			1200	电梯隔离开关，位置 / 高度以厂家为准；离墙 > 0.6 m，现场确认
L01	灯 · 壁灯 F32	餐厅	西墙（1E34）	墙端 420	墙端 560	1930	模型 v42 灯具中心高度（F32.001）
L08	灯 · 壁灯 G26_1（户外）	户外	西墙（1E20）	墙端 1600	墙端 320	1770	模型 v42 灯具中心高度（G26_1）；原点位离墙面 440，已按墙面定位
L09	灯 · 壁灯 G26_2（户外）	户外	南墙（1E17）	墙端 4730	门洞边 1100	1800	模型 v42 灯具中心高度（G26_2）
L10	灯 · 壁灯 G26_3（户外）	户外	南墙（1E17）	墙端 1940	门洞边 3890	1800	模型 v42 灯具中心高度（G26_3）
L44	灯 · 壁灯 G26_4（户外）	户外	西墙（1E21）	门洞边 480	门洞边 1090	3350	模型 v42 灯具中心高度（G26_4_FloodLight_SOLLA）

项目 Project	27PR 住宅改造 · 27 Penrith Road
图名 Title	一层墙面点位定位表（插座 / 开关 / 专用 / 壁灯）
图号 Sheet	SO-04 比例 — @A3
专业 Discipline	电气定位 Setting out
版次 Rev	A · 2026-10-08 · 施工图（待持证电工 / 水工复核）

一层天花灯位 / 地面点位定位表

一层天花灯位 / 地面点位定位表 (尺寸 mm; 距左 / 右端 = 面对墙看的左 / 右; 高度 = 底盒中心离本房间完成地面)

编号	类型 / 名称	房间	位置	南北向: 距墙	东西向: 距墙	高度	备注
C26	插座·单联插座	厨房 (吧台区)	岛台	南墙 1350	东墙 4500	800	岛台端板插座 h 800 (或改台面弹起插座)
L02	灯·主灯 G07	餐厅	天花	北墙 1650	东墙 1810	2600	天花安装 (吸顶 / 吊灯线盒)
L03	灯·主灯 G06	起居室	天花	北墙 1820	东墙 5790	2600	天花安装 (吸顶 / 吊灯线盒)
L04	灯·主灯 G08	储物间	天花	南墙 480	东墙 6960	2600	天花安装 (吸顶 / 吊灯线盒)
L05	灯·主灯 G15	客厅	天花	南墙 1730	西门窗洞 2000	2600	天花安装 (吸顶 / 吊灯线盒)
L06	灯·主灯 G16	客厅	天花	北墙 1140	西门窗洞 5140	2600	天花安装 (吸顶 / 吊灯线盒)
L07	灯·门廊吊灯 G25 (户外)	户外	天花	南墙 470	东门窗洞 200	2600	吊在门廊顶 (模型 v42 顶高 2600)
L11	灯·GU10 筒灯	起居室	天花	南墙 870	东墙 950	2600	天花安装 (吸顶 / 吊灯线盒)
L12	灯·GU10 筒灯	起居室	天花	南墙 870	东墙 2180	2600	天花安装 (吸顶 / 吊灯线盒)
L13	灯·GU10 筒灯	起居室	天花	南墙 2070	东墙 3410	2600	天花安装 (吸顶 / 吊灯线盒)
L14	灯·GU10 筒灯	起居室	天花	北墙 1800	东墙 7030	2600	天花安装 (吸顶 / 吊灯线盒)
L15	灯·GU10 筒灯	起居室	天花	北墙 760	西门窗洞 2060	2600	天花安装 (吸顶 / 吊灯线盒)
L16	灯·GU10 筒灯	起居室	天花	北墙 760	西门窗洞 3290	2600	天花安装 (吸顶 / 吊灯线盒)
L17	灯·GU10 筒灯	起居室	天花	北墙 1830	东墙 4560	2600	天花安装 (吸顶 / 吊灯线盒)
L18	灯·GU10 筒灯	起居室	天花	北墙 700	西门窗洞 820	2600	天花安装 (吸顶 / 吊灯线盒)
L19	灯·GU10 筒灯	餐厅	天花	南墙 2340	东墙 1810	2600	天花安装 (吸顶 / 吊灯线盒)
L20	灯·GU10 筒灯	餐厅	天花	南墙 2340	东墙 3050	2600	天花安装 (吸顶 / 吊灯线盒)
L21	灯·GU10 筒灯	餐厅	天花	南墙 3300	东墙 3060	2600	天花安装 (吸顶 / 吊灯线盒)
L22	灯·GU10 筒灯	餐厅	天花	南墙 4190	西门窗洞 4800	2600	天花安装 (吸顶 / 吊灯线盒)
L23	灯·GU10 筒灯	餐厅	天花	北墙 710	西门窗洞 6040	2600	天花安装 (吸顶 / 吊灯线盒)
L24	灯·GU10 筒灯	餐厅	天花	北墙 710	西门窗洞 7270	2600	天花安装 (吸顶 / 吊灯线盒)
L25	灯·GU10 筒灯	餐厅	天花	北墙 1670	东墙 590	2600	天花安装 (吸顶 / 吊灯线盒)
L26	灯·GU10 筒灯	餐厅	天花	北墙 2560	东墙 580	2600	天花安装 (吸顶 / 吊灯线盒)
L27	灯·主灯位 (灯具待选)	厨房	天花	南墙 1660	东墙 1220	2600	天花安装 (吸顶 / 吊灯线盒)
L28	灯·主灯位 (灯具待选)	厨房 (吧台区)	天花	北墙 1420	东墙 4270	2600	天花安装 (吸顶 / 吊灯线盒)
L29	灯·GU10 筒灯	储物间	天花	南墙 510	东墙 5760	2600	天花安装 (吸顶 / 吊灯线盒)
L30	灯·GU10 筒灯	客厅	天花	南墙 590	东墙 2580	2600	天花安装 (吸顶 / 吊灯线盒)
L31	灯·GU10 筒灯	客厅	天花	南墙 610	西墙 1490	2600	天花安装 (吸顶 / 吊灯线盒)
L32	灯·GU10 筒灯	客厅	天花	南墙 1730	西门窗洞 930	2600	天花安装 (吸顶 / 吊灯线盒)
L33	灯·GU10 筒灯	客厅	天花	北墙 730	西墙 950	2600	天花安装 (吸顶 / 吊灯线盒)
L34	灯·GU10 筒灯	客厅	天花	北墙 730	西墙 2010	2600	天花安装 (吸顶 / 吊灯线盒)
L35	灯·GU10 筒灯	客厅	天花	北墙 740	西墙 3230	2600	天花安装 (吸顶 / 吊灯线盒)
L36	灯·GU10 筒灯	客厅	天花	北墙 1750	西门窗洞 3240	2600	天花安装 (吸顶 / 吊灯线盒)
L37	灯·GU10 筒灯	客厅	天花	北墙 2940	东墙 1350	2600	天花安装 (吸顶 / 吊灯线盒)
L38	灯·GU10 筒灯	洗衣房	天花	南墙 1010	西墙 510	2600	天花安装 (吸顶 / 吊灯线盒)
L39	灯·GU10 筒灯	卫生间	天花	南墙 420	西墙 630	2600	天花安装 (吸顶 / 吊灯线盒)
L40	灯·围栏地灯 (户外)	户外	室外地面	南墙 8590	西墙 1060	0	地面安装, SWA 埋地 ≥ 450
L41	灯·围栏地灯 (户外)	户外	室外地面	南墙 5340	西墙 3070	0	地面安装, SWA 埋地 ≥ 450
L42	灯·围栏地灯 (户外)	户外	室外地面	南墙 5340	西墙 4920	0	地面安装, SWA 埋地 ≥ 450
L43	灯·围栏地灯 (户外)	户外	室外地面	南墙 5340	西墙 5970	0	地面安装, SWA 埋地 ≥ 450

项目 Project	27PR 住宅改造 · 27 Penrith Road
图名 Title	一层天花灯位 / 地面点位定位表
图号 Sheet	SO-05 比例 — @A3
专业 Discipline	电气定位 Setting out
版次 Rev	A · 2026-10-08 · 施工图 (待持证电工 / 木工复核)

二层墙面点位定位表（插座 / 开关 / 专用 / 壁灯）

二层墙面点位定位表（插座 / 开关 / 专用 / 壁灯）（尺寸 mm；距左 / 右端 = 面对墙看的左 / 右；高度 = 底盒中心离本房间完成地面）

编号	类型 / 名称	房间	墙面（立面）	距左端 mm	距右端 mm	高度	依据 / 备注
S1	开关 · 1 联开关 · 键 6	盥洗室门旁	西墙（2E09）	门洞边 0	门洞边 120	1200	开关中心 1100；离墙角 / 洞口 < 100，现场确认
S2	开关 · 1 联开关 · 键 6+	西卫生间门外	东墙（2E27）	墙角 840	门洞边 120	1200	开关中心 1100
S3	开关 · 1 联开关 · 键 2	主卧床头柜上方（C19 一侧，离地 700，与门口 S4 双控）	南墙（2E04）	墙角 550	墙角 2470	700	开关中心 1100
S4	开关 · 2 联开关 · 键 10/11	主卧东墙 · 床头侧	东墙（2E02）	门洞边 370	墙角 800	1200	开关中心 1100
S5	开关 · 1 联开关 · 键 5	衣帽间门旁	北墙（2E32）	墙端 120	墙角 440	1200	开关中心 1100
S6	开关 · 2 联开关 · 键 12/13	卧室2 床头侧（东墙）	南墙（2E08）	墙角 3600	墙角 550	1200	开关中心 1100
S7	开关 · 2 联开关 · 键 14/15	卧室2 门旁（门西侧短墙，卧室2 一侧，锁侧）	东墙（2E33）	墙角 240	门洞边 130	1200	开关中心 1100
S8	开关 · 1 联开关 · 键 3	走廊北端	东墙（2E11）	墙端 280	门洞边 890	1200	开关中心 1100
S9	开关 · 1 联开关 · 键 1	北卫生间门外	西墙（2E23）	墙端 780	墙角 0	1200	开关中心 1100；原点离墙面 260，已按墙面定位；离墙角 / 洞口 < 100，现场确认
S10	开关 · 1 联开关 · 键 4	卧室3 门旁	西墙（2E14）	门洞边 160	墙角 900	1200	开关中心 1100
S11	开关 · 2 联开关 · 键 16/17	走廊南端 · 楼梯口	北墙（2E24）	墙端 400	门洞边 2150	1200	开关中心 1100
S12	开关 · 1 联开关 · 键 7	楼梯顶	北墙（2E24）	墙端 1730	门洞边 820	1200	开关中心 1100
S13	开关 · 1 联开关 · 键 8	卧室 4 门旁	西墙（2E19）	门洞边 100	墙角 1180	1200	开关中心 1100
S14	开关 · 1 联开关 · 键 9	卧室 4 内 · 卫生间门南侧（隔墙短墙）	东墙（2E15）	墙端 0	墙角 1020	1200	开关中心 1100；离墙角 / 洞口 < 100，现场确认
C01	插座 · 单联插座	衣帽间	东墙（2E30）	墙角 1600	墙角 100	300	300（业主原定，与模型一致）；已挪到家具外侧（原位置被家具挡住）；离墙角 / 洞口 < 100，现场确认；在 F15（高 2100）后面会被挡住，建议移到侧边或抬高
C02	插座 · 双联插座	楼梯	南墙（2E25）	墙角 3190	墙角 320	300	300（业主原定，与模型一致）
C03	插座 · 双联插座	卧室 2	南墙（2E08）	墙角 1460	墙角 2680	650	床头柜面 500 + 150（略高于柜面）
C04	插座 · 双联插座	卧室 2	南墙（2E08）	墙角 3610	墙角 540	650	床头柜面 500 + 150（略高于柜面）
C05	插座 · 双联插座	盥洗室	西墙（2E29）	窗洞边 30	墙角 270	300	300（业主原定，与模型一致）；离墙角 / 洞口 < 100，现场确认
C06	插座 · 双联插座	盥洗室	南墙（2E28）	门洞边 240	窗洞边 40	300	300（业主原定，与模型一致）；离墙角 / 洞口 < 100，现场确认
C07	插座 · 双联插座	卧室 2	东墙（2E06）	门洞边 100	墙角 1830	300	300（业主原定，与模型一致）；已挪到家具外侧（原位置被家具挡住）
C08	插座 · 双联插座	卧室 2	北墙（2E07）	墙端 670	墙端 1100	300	300（业主原定，与模型一致）
C09	插座 · 单联插座	衣帽间	北墙（2E31）	墙角 100	墙角 1600	300	300（业主原定，与模型一致）；已挪到家具外侧（原位置被家具挡住）；在 F15（高 2100）后面会被挡住，建议移到侧边或抬高
C10	插座 · 双联插座	卧室 3	南墙（2E13）	门洞边 680	墙角 1560	970	台面 770 上方（底边离台面约 150）
C11	插座 · 双联插座	卧室 3	南墙（2E13）	门洞边 1700	墙角 550	970	台面 770 上方（底边离台面约 150）
C12	插座 · 单联插座	卧室 3	西墙（2E14）	门洞边 100	墙角 950	300	300（业主原定，与模型一致）；已挪到家具外侧（原位置被家具挡住）
C13	插座 · 双联插座	卧室 3	北墙（2E12）	墙角 2310	墙角 100	300	300（业主原定，与模型一致）；已挪到家具外侧（原位置被家具挡住）；离墙角 / 洞口 < 100，现场确认
C14	插座 · 空调插座	卧室 4	西墙（2E19）	门洞边 910	墙角 370	2540	空调内机侧面，与机身中高齐平（内机底 2390）
C15	插座 · 双联插座	卧室 4	北墙（2E16）	窗洞边 260	墙角 1190	300	300（业主原定，与模型一致）
C16	插座 · 双联插座	卧室 4	南墙（2E18）	墙端 1200	门洞边 530	300	300（业主原定，与模型一致）
C17	插座 · 双联插座	卧室 4	西墙（2E19）	门洞边 160	墙角 1120	300	300（业主原定，与模型一致）
C18	插座 · 双联插座	卧室 4	北墙（2E17）	墙角 640	窗洞边 370	300	300（业主原定，与模型一致）
C19	插座 · 双联插座	主卧	南墙（2E04）	墙角 690	墙角 2330	630	床头柜面 480 + 150（略高于柜面）；数据里房间为「衣帽间」，按位置是主卧床头
C20	插座 · 双联插座	主卧	南墙（2E04）	墙角 2930	墙角 90	630	床头柜面 480 + 150（略高于柜面）；离墙角 / 洞口 < 100，现场确认
C21	插座 · 双联插座	主卧	西墙（2E05）	墙角 2120	墙角 1370	300	300（业主原定，与模型一致）
C22	插座 · 双联插座	主卧	北墙（2E03）	墙角 2540	墙角 4570	300	300（业主原定，与模型一致）
C23	插座 · 双联插座	主卧	东墙（2E01）	墙角 640	墙角 780	300	300（业主原定，与模型一致）
C24	插座 · 空调插座	卧室 3	东墙（2E10）	窗洞边 0	门洞边 1830	2190	空调内机侧面，与机身中高齐平（内机底 2040）；离墙角 / 洞口 < 100，现场确认
C25	插座 · 单联插座	电梯	东墙（2E26）	墙端 210	墙角 560	300	300（业主原定，与模型一致）
C26	插座 · 双联插座	卧室 3	东墙（2E10）	窗洞边 430	门洞边 1400	300	300（业主原定，与模型一致）
N-TR1	新增 · 西卫电热毛巾架出线面板（新增）	卫生间	南墙（2E22）	墙角 580	墙端 620	1100	毛巾架下沿旁出线面板（模型位置），FCU 13A 装在卫生间外 h 1100
N-TR2	新增 · 北卫智能马桶 + 电热毛巾架出线面板（双联，新增）	卫生间	东墙（2E21）	窗洞边 1190	墙角 760	300	马桶与毛巾架之间的双联出线面板 h 300（毛巾架挪到马桶旁后墙，离马桶约 200）；两个 FCU 13A 装在卫生间门外 h 1100
N-WC1	新增 · 西卫智能马桶电源出线面板（新增）	卫生间	东墙（2E20）	墙端 500	墙端 70	300	马桶侧后方出线面板 h 300，FCU 13A 装在卫生间外开关旁 h 1100

项目 Project	27PR 住宅改造 · 27 Penrith Road
图名 Title	二层墙面点位定位表（插座 / 开关 / 专用 / 壁灯）
图号 Sheet	SO-06 比例 — @A3
专业 Discipline	电气定位 Setting out
版次 Rev	A · 2026-10-08 · 施工图（待持证电工 / 水工复核）

二层天花灯位 / 地面点位定位表


二层天花灯位 / 地面点位定位表 (尺寸 mm; 距左 / 右端 = 面对墙看的左 / 右; 高度 = 底盒中心离本房间完成地面)

编号	类型 / 名称	房间	位置	南北向: 距墙	东西向: 距墙	高度	备注
L01	灯 · 主灯 F06	楼梯	天花	南墙 530	东墙 1380	2500	天花安装 (吸顶 / 吊灯线盒)
L02	灯 · 主灯 F11	走廊	天花	南墙 2690	西墙 470	2500	天花安装 (吸顶 / 吊灯线盒)
L03	灯 · 主灯 F19	主卧	天花	南墙 1520	西墙 2130	2500	天花安装 (吸顶 / 吊灯线盒)
L04	灯 · 主灯 F20	卧室 2	天花	北墙 1420	东墙 2490	2500	天花安装 (吸顶 / 吊灯线盒)
L05	灯 · 主灯 F22	卧室 3	天花	北墙 1520	东墙 1180	2500	天花安装 (吸顶 / 吊灯线盒)
L06	灯 · 主灯 F23	卧室 4	天花	南墙 910	东墙 1490	2856	天花安装 (吸顶 / 吊灯线盒)
L07	灯 · GU10 筒灯	卫生间	天花	南墙 1130	西墙 660	2500	天花安装 (吸顶 / 吊灯线盒)
L08	灯 · GU10 筒灯	卫生间	天花	南墙 430	东墙 1040	2856	天花安装 (吸顶 / 吊灯线盒)
L09	灯 · GU10 筒灯	盥洗室	天花	北墙 880	东墙 520	2500	天花安装 (吸顶 / 吊灯线盒)
L10	灯 · GU10 筒灯	衣帽间	天花	北墙 380	西墙 820	2500	天花安装 (吸顶 / 吊灯线盒)
L11	灯 · GU10 筒灯	卧室 2	天花	南墙 1160	西墙 3360	2500	天花安装 (吸顶 / 吊灯线盒)
L12	灯 · 主灯位 (灯具待选)	主卧	天花	北墙 800	东墙 2360	2500	天花安装 (吸顶 / 吊灯线盒)
L13	灯 · GU10 筒灯	卫生间	天花	南墙 810	东墙 490	2500	天花安装 (吸顶 / 吊灯线盒)
L14	灯 · GU10 筒灯	衣帽间	天花	北墙 1100	西墙 820	2500	天花安装 (吸顶 / 吊灯线盒)
L15	灯 · 主灯 F11#2	电梯	天花	北墙 3460	西墙 440	2500	天花安装 (吸顶 / 吊灯线盒)


项目 Project	27PR 住宅改造 · 27 Penrith Road
图名 Title	二层天花灯位 / 地面点位定位表
图号 Sheet	SO-07 比例 — @A3
专业 Discipline	电气定位 Setting out
版次 Rev	A · 2026-10-08 · 施工图 (待持证电工 / 水工复核)

一层墙面立面 Wall elevations 1:50


1E01 • 储物间 • 北墙

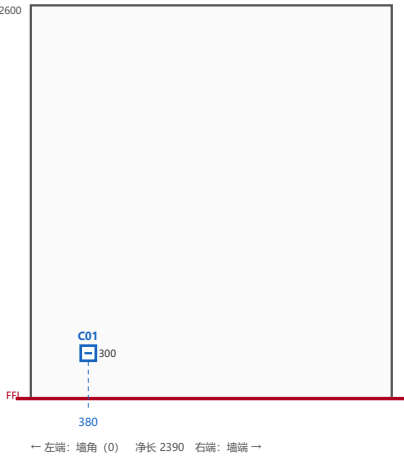


1E02 • 储物间 • 南墙

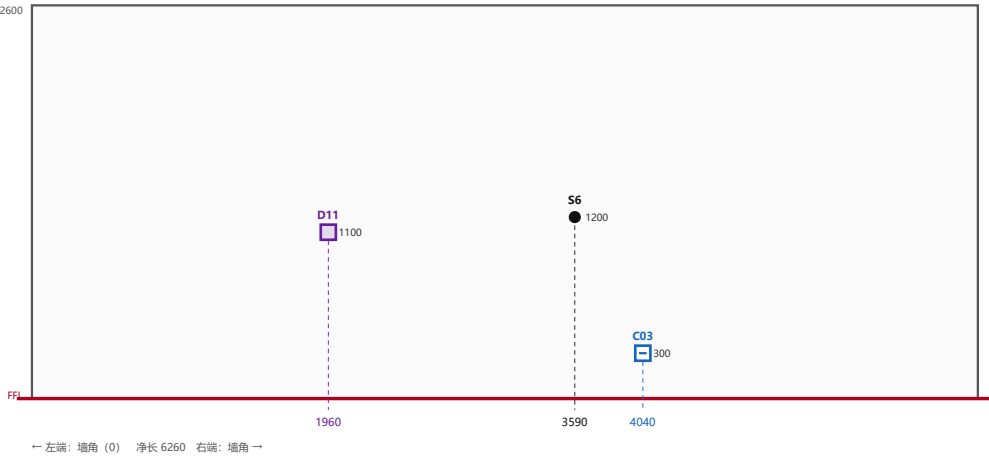


1E03 • 储物间 • 西墙

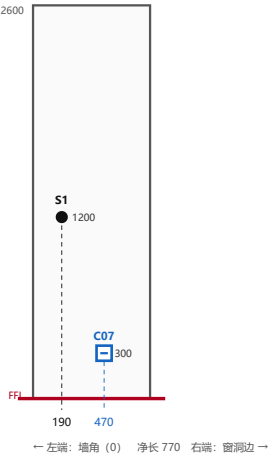


1E04 • 储物间 • 东墙

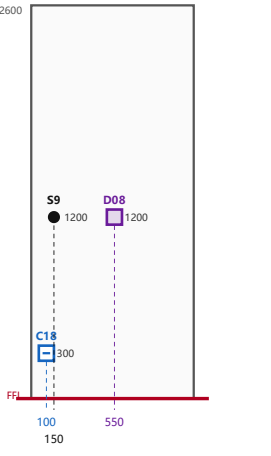


1E05 • 厨房 • 北墙

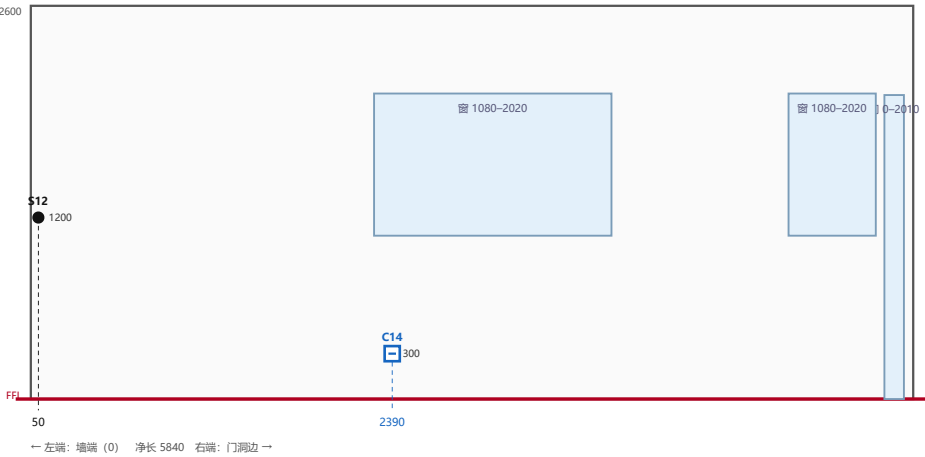


1E06 • 厨房 • 南墙

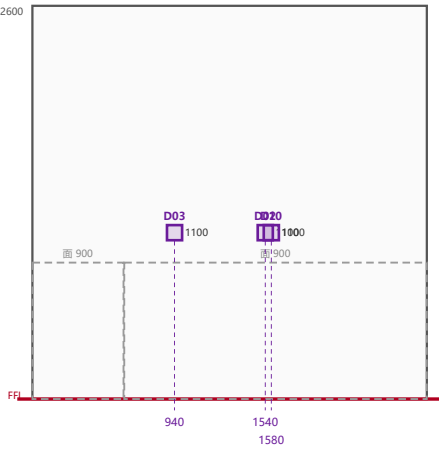

1E07 • 厨房（吧台区）• 北墙

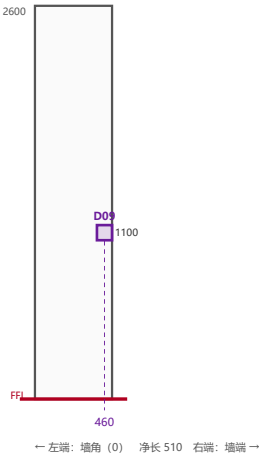


1E08 • 厨房（吧台区）• 南墙

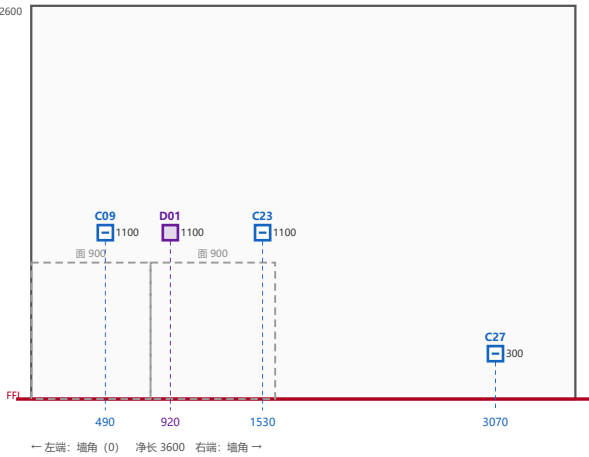


项目 Project	27PR 住宅改造 · 27 Penrith Road
图名 Title	一层墙面立面 Wall elevations 1:50
图号 Sheet	SO-10 比例 1:50 立面 @A3
专业 Discipline	电气定位 Setting out
版次 Rev	A · 2026-10-08 · 施工图 (待持证电工 / 水工复核)

一层墙面立面 Wall elevations 1:50


1E09 • 厨房（吧台区）• 西墙

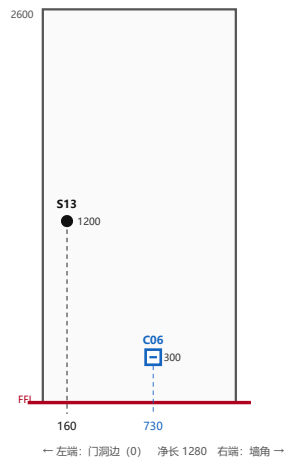


1E10 • G15 区 • 通后花园门旁 • 东墙

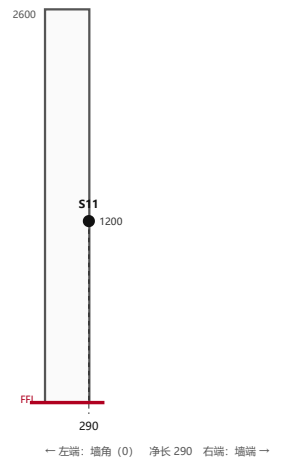


1E11 • 客厅 • 北墙

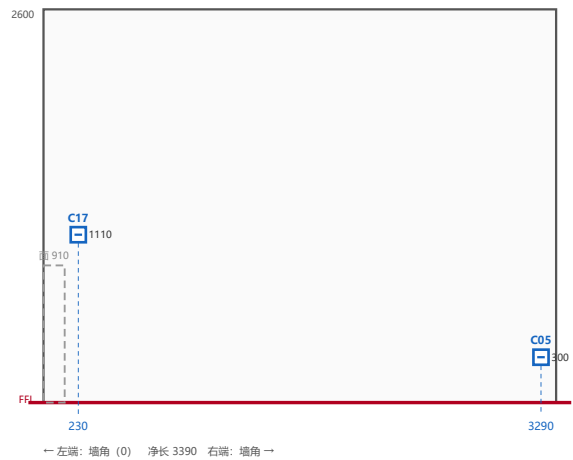


1E12 • 客厅 • 北墙

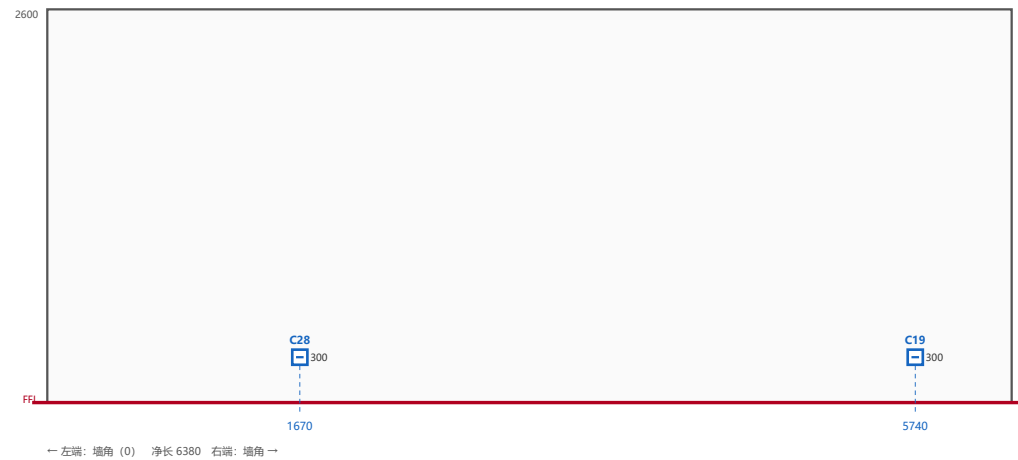


1E13 • 客厅 • 南墙

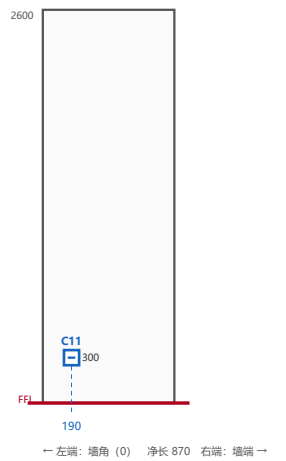


1E14 • 客厅 • 南墙

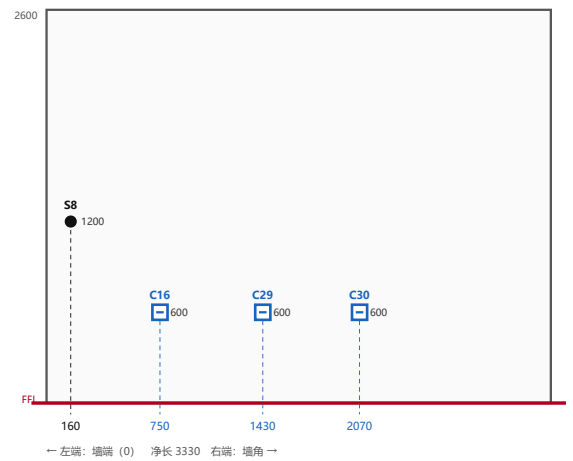

1E15 • 卫生间门外 • 南墙

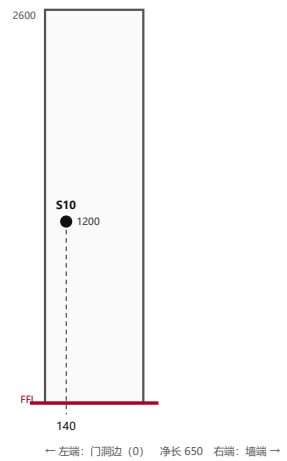


1E16 • 户外 • 东墙

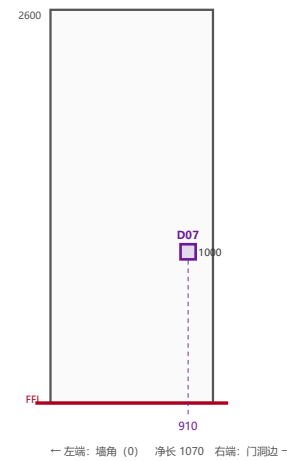


项目 Project	27PR 住宅改造 · 27 Penrith Road
图名 Title	一层墙面立面 Wall elevations 1:50
图号 Sheet	SO-11 比例 1:50 立面 @A3
专业 Discipline	电气定位 Setting out
版次 Rev	A · 2026-10-08 · 施工图 (待持证电工 / 水工复核)

一层墙面立面 Wall elevations 1:50


1E17 • 户外 • 南墙

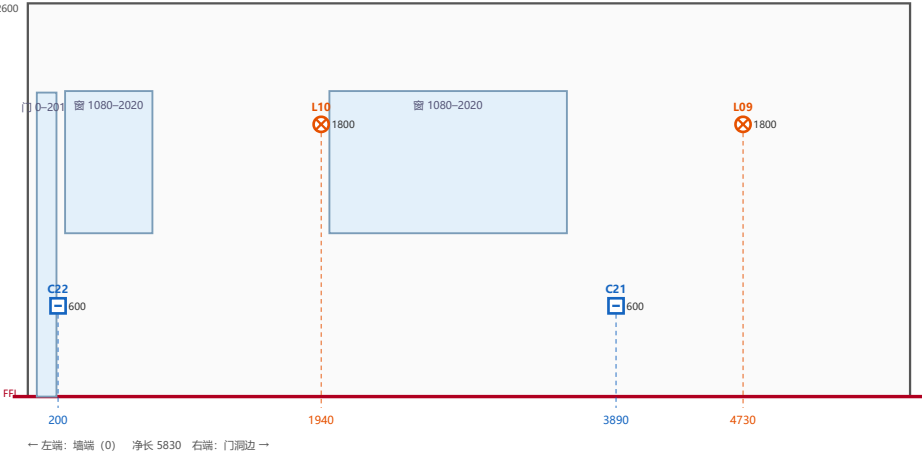


1E18 • 户外 • 西墙

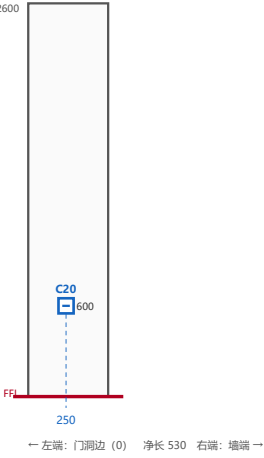


1E19 • 户外 • 西墙

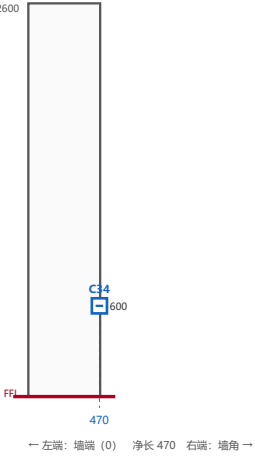


1E20 • 户外 • 西墙

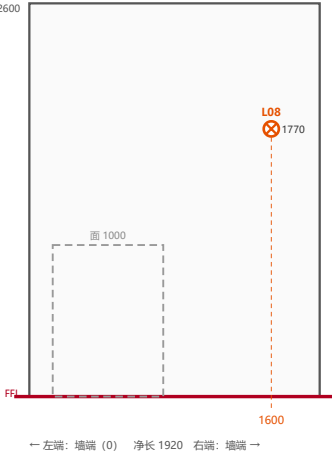


1E21 • 户外 • 西墙

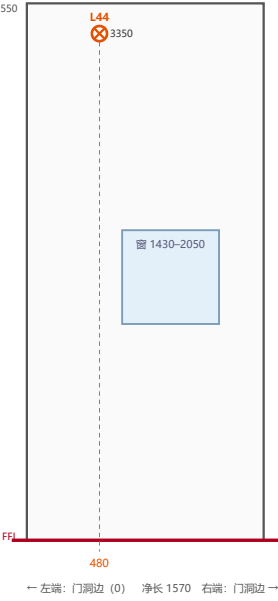


1E22 • 洗衣房 • 东墙

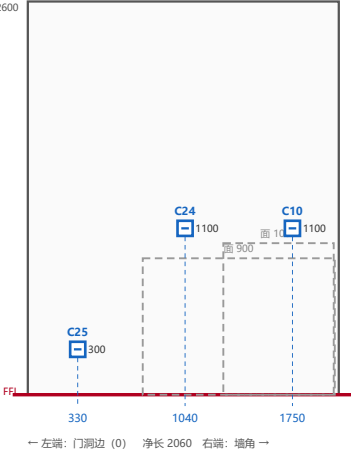


1E23 • 洗衣房 • 东墙

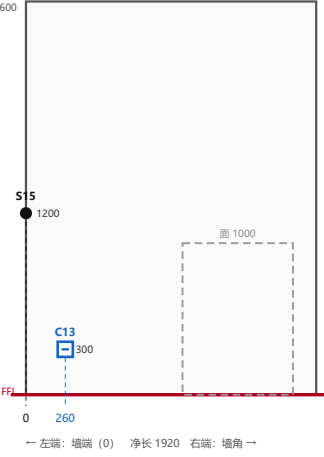


1E24 • 洗衣房 • 南墙

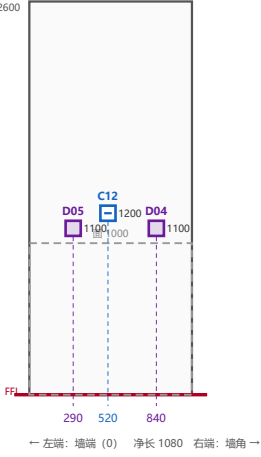

1E25 • 洗衣房门旁 • 西墙

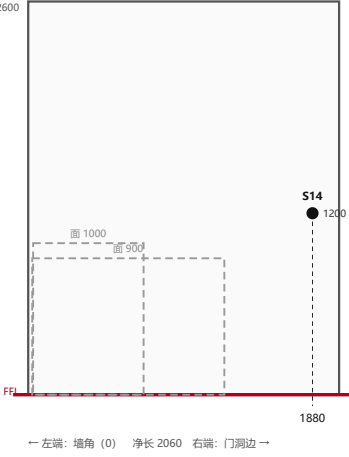


1E26 • 起居室 • 南墙

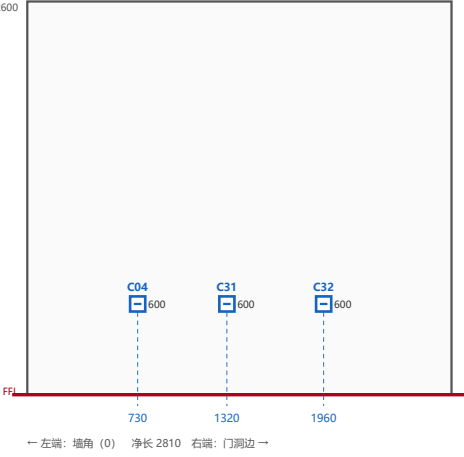


项目 Project	27PR 住宅改造 · 27 Penrith Road
图名 Title	一层墙面立面 Wall elevations 1:50
图号 Sheet	SO-12 比例 1:50 立面 @A3
专业 Discipline	电气定位 Setting out
版次 Rev	A · 2026-10-08 · 施工图 (待持证电工 / 木工复核)

一层墙面立面 Wall elevations 1:50

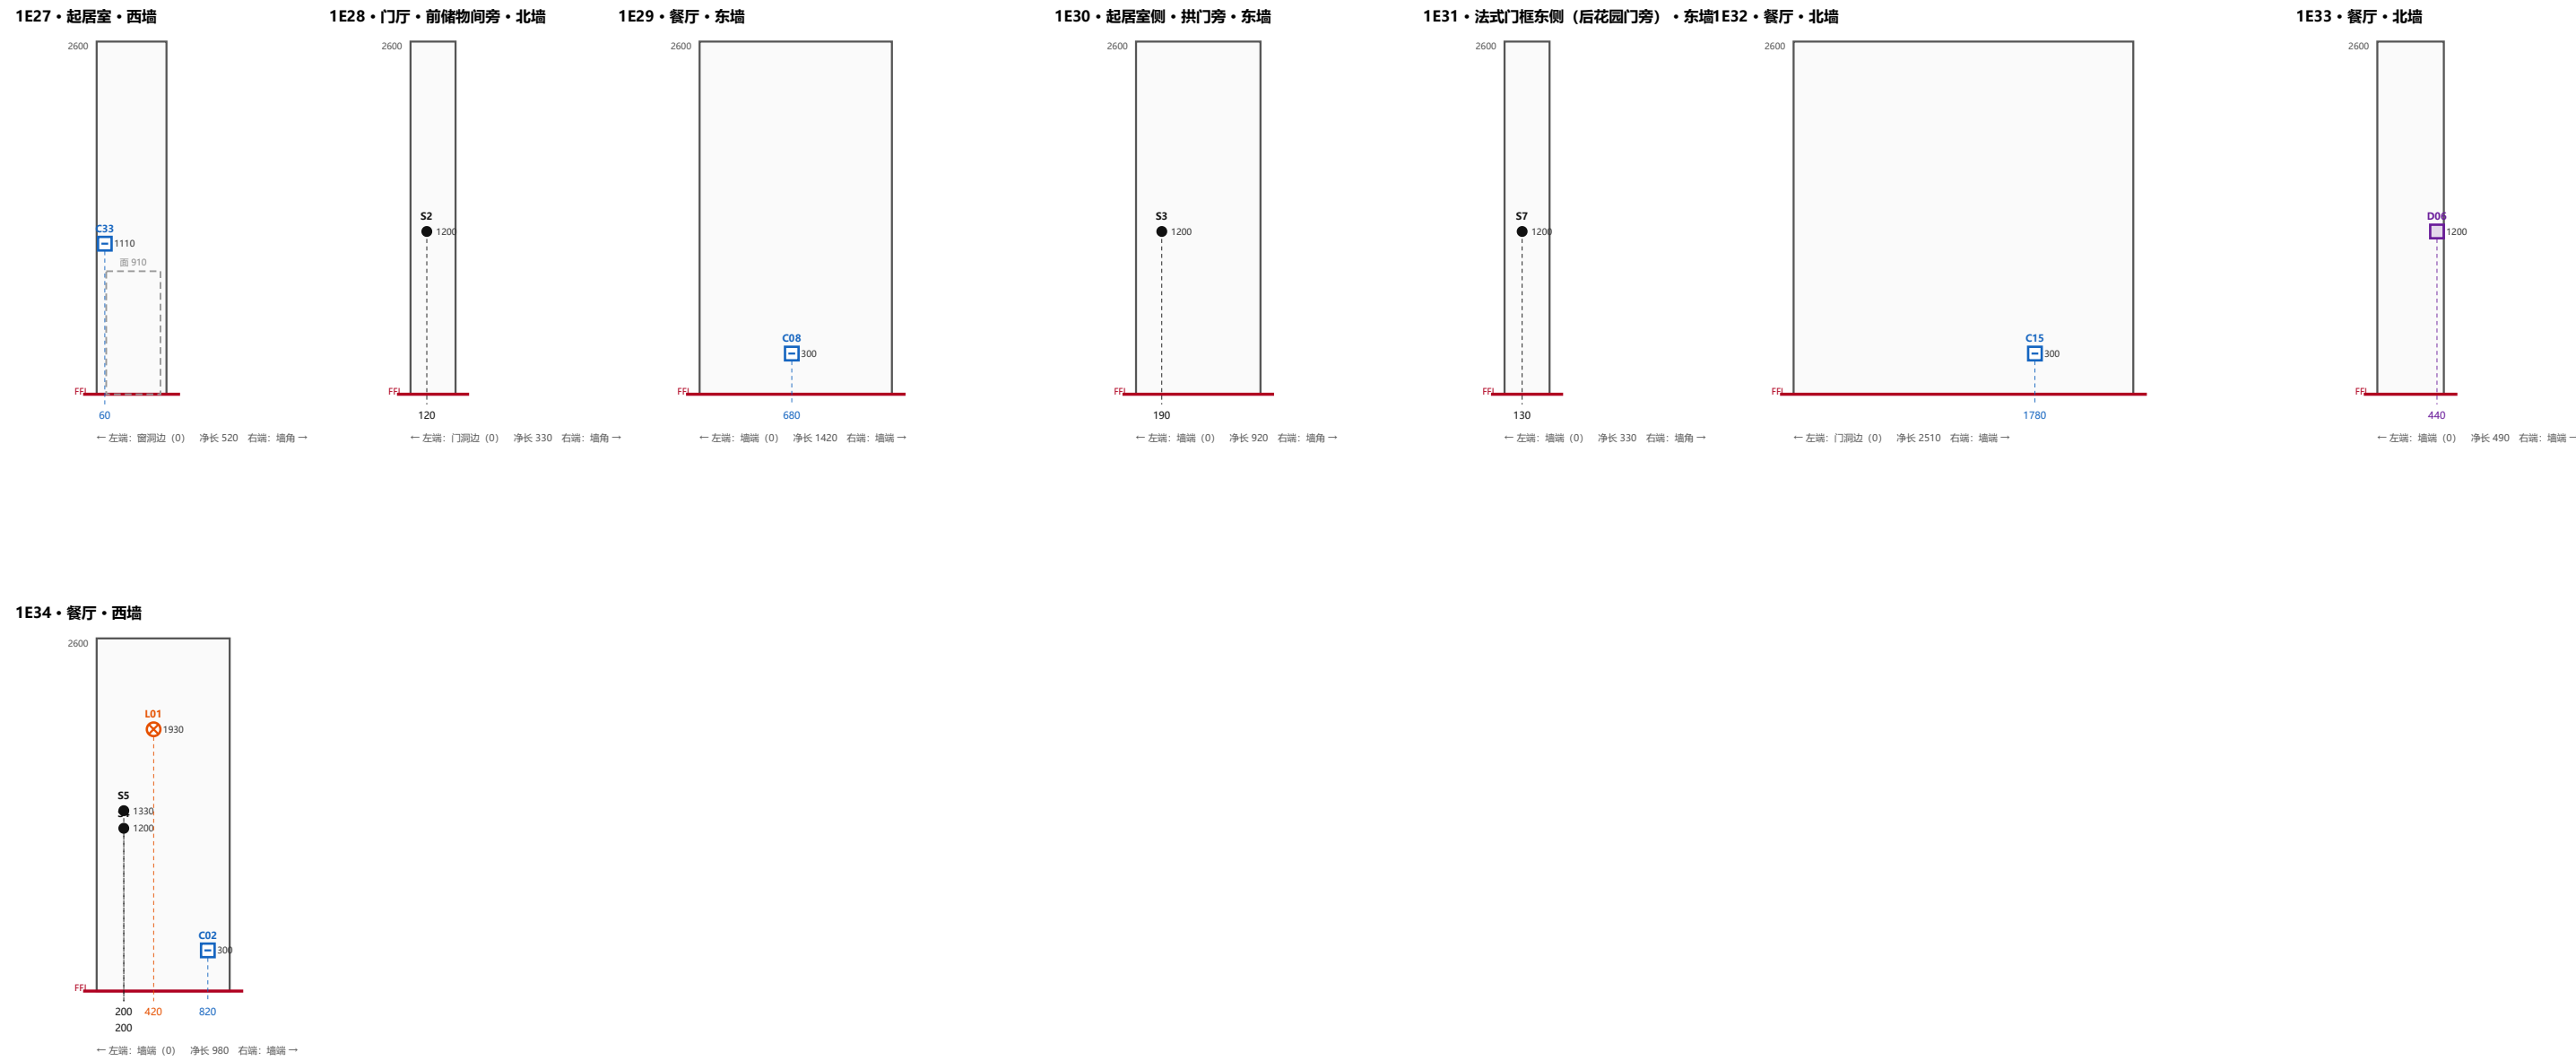

项目 Project	27PR 住宅改造 · 27 Penrith Road
图名 Title	一层墙面立面 Wall elevations 1:50
图号 Sheet	SO-13 比例 1:50 立面 @A3
专业 Discipline	电气定位 Setting out
版次 Rev	A · 2026-10-08 · 施工图 (待持证电工 / 水工复核)


二层墙面立面 Wall elevations 1:50

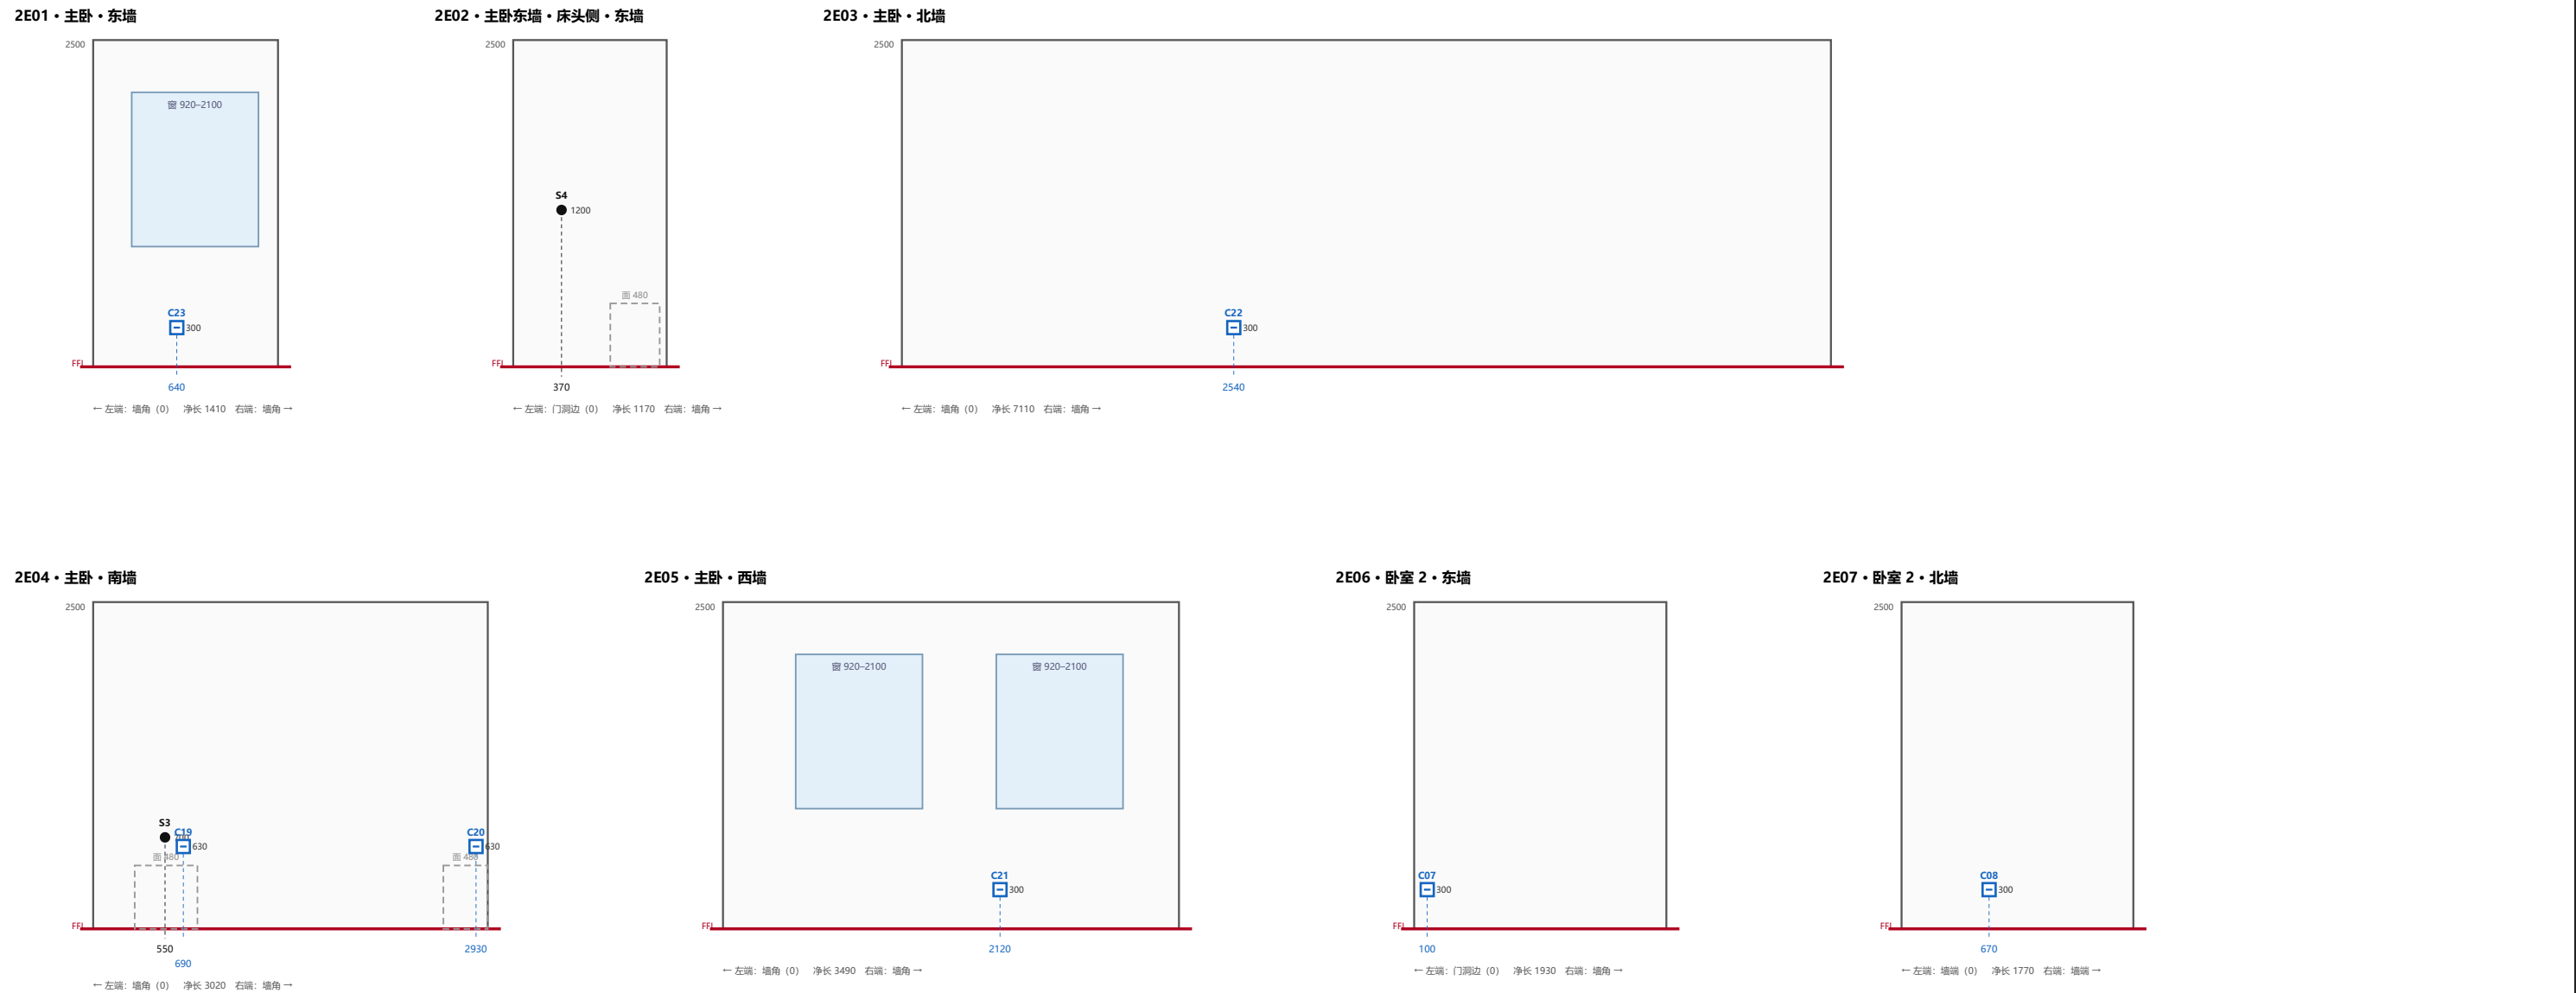


项目 Project	27PR 住宅改造 · 27 Penrith Road
图名 Title	二层墙面立面 Wall elevations 1:50
图号 Sheet	SO-14 比例 1:50 立面 @A3
专业 Discipline	电气定位 Setting out
版次 Rev	A · 2026-10-08 · 施工图 (待持证电工 / 水工复核)

二层墙面立面 Wall elevations 1:50


2E08 • 卧室 2 • 南墙

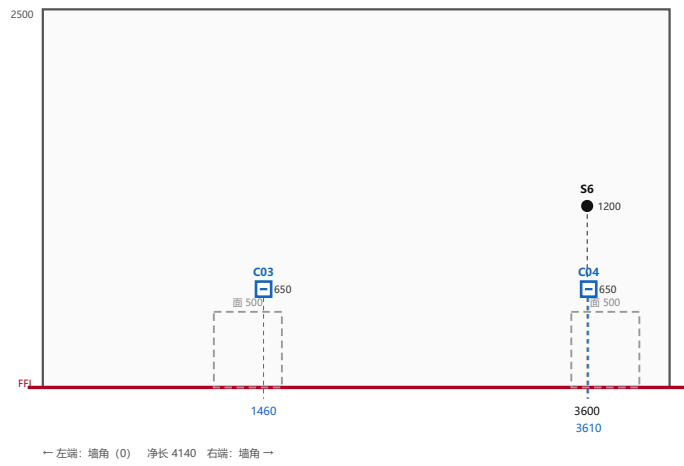


2E09 • 盥洗室门旁 • 西墙

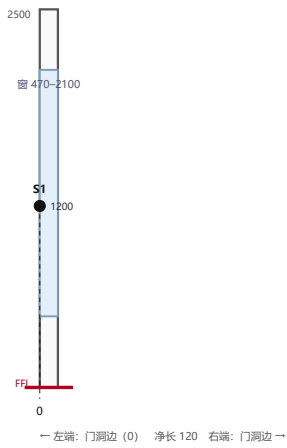


2E10 • 卧室 3 • 东墙

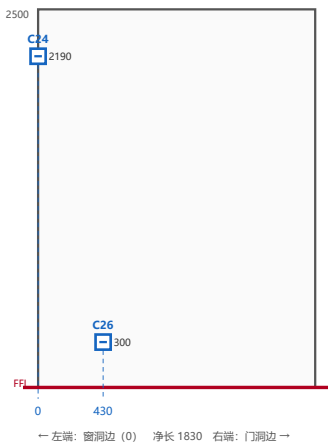


2E11 • 走廊北端 • 东墙

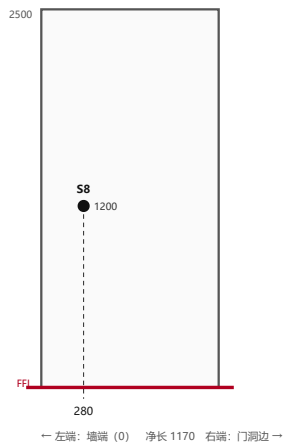


2E12 • 卧室 3 • 北墙

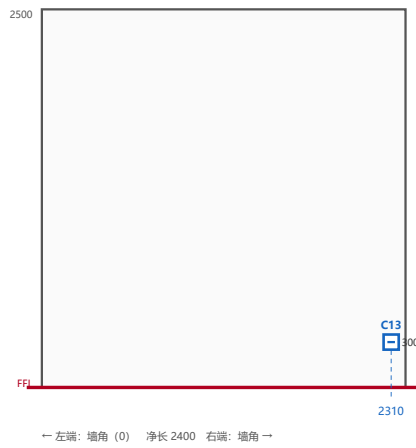


2E13 • 卧室 3 • 南墙

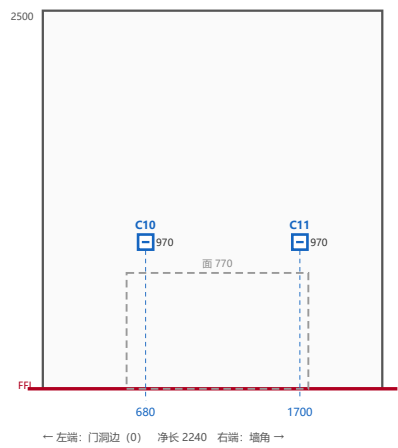


2E14 • 卧室 3 • 西墙

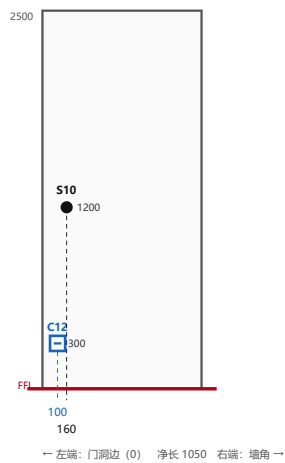


2E15 • 卧室 4 内 • 卫生间门南侧 (隔墙短墙) • 东墙

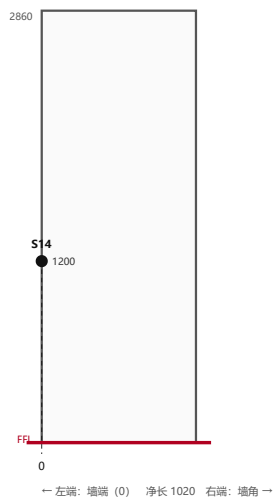


2E16 • 卧室 4 • 北墙

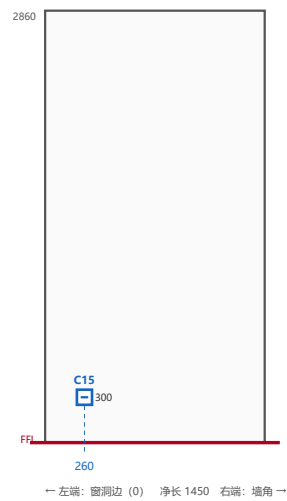

2E17 • 卧室 4 • 北墙

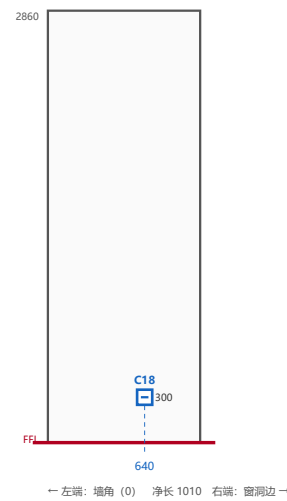


2E18 • 卧室 4 • 南墙

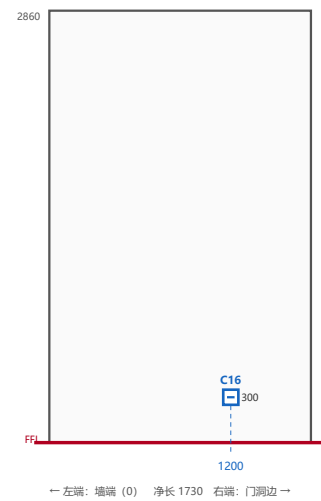


项目 Project	27PR 住宅改造 · 27 Penrith Road
图名 Title	二层墙面立面 Wall elevations 1:50
图号 Sheet	SO-15 比例 1:50 立面 @A3
专业 Discipline	电气定位 Setting out
版次 Rev	A · 2026-10-08 · 施工图 (待持证电工 / 水工复核)

二层墙面立面 Wall elevations 1:50


2E19 • 卧室 4 • 西墙

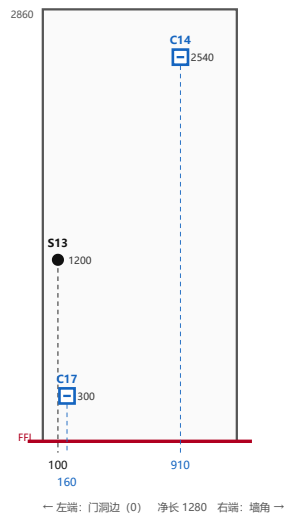


2E20 • 卫生间 • 东墙

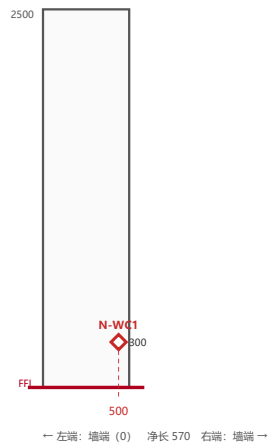


2E21 • 卫生间 • 东墙

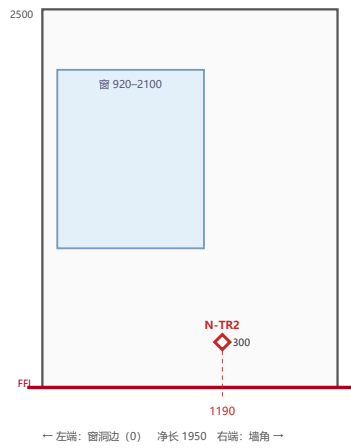


2E22 • 卫生间 • 南墙

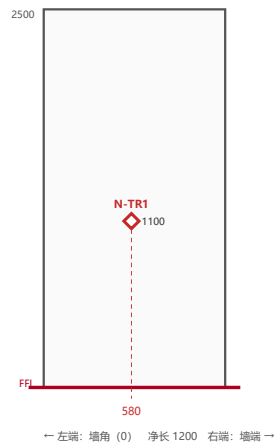


2E23 • 北卫生间门外 • 西墙

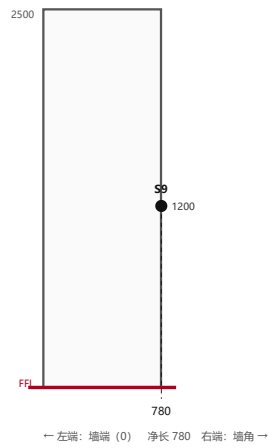


2E24 • 走廊南端 • 楼梯口 • 北墙

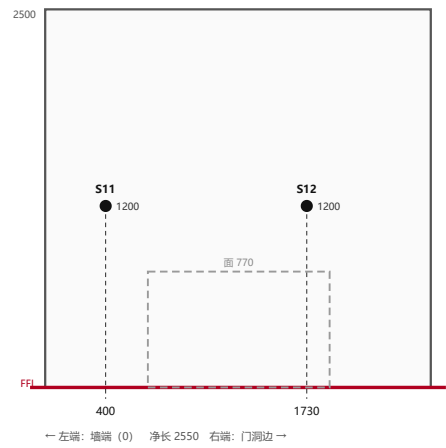


2E25 • 楼梯 • 南墙

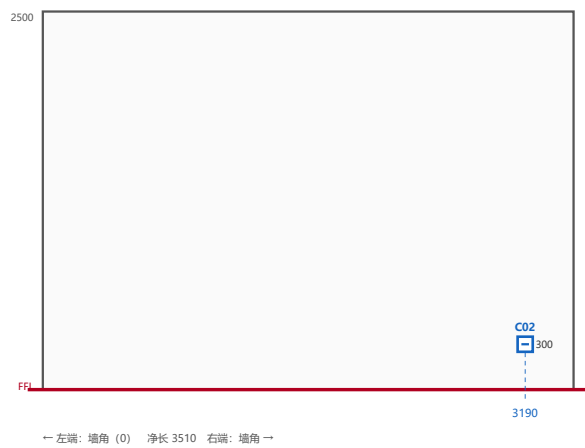


2E26 • 电梯 • 东墙

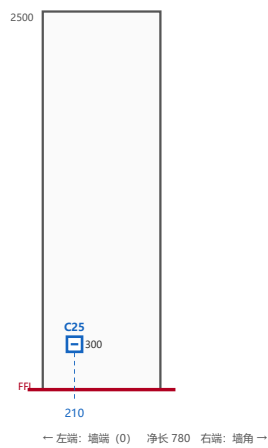


2E27 • 西卫生间门外 • 东墙

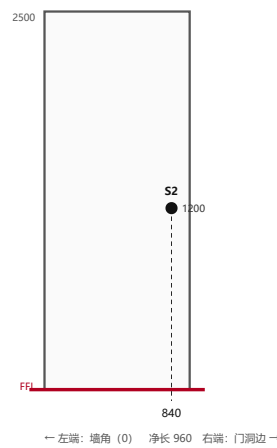


2E28 • 盥洗室 • 南墙

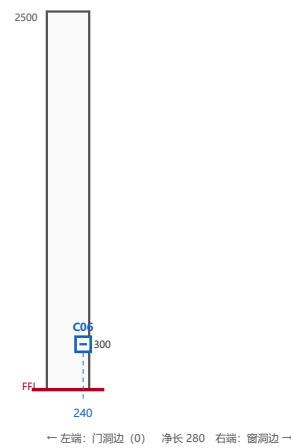

2E29 • 盥洗室 • 西墙

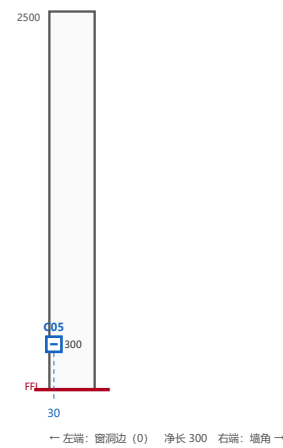


2E30 • 衣帽间 • 东墙

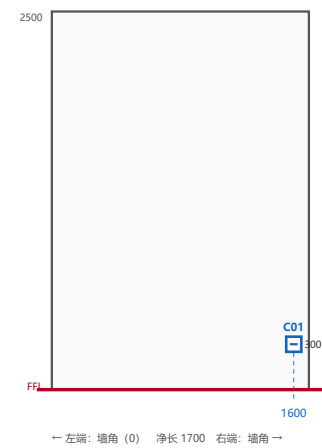


项目 Project	27PR 住宅改造 · 27 Penrith Road
图名 Title	二层墙面立面 Wall elevations 1:50
图号 Sheet	SO-16 比例 1:50 立面 @A3
专业 Discipline	电气定位 Setting out
版次 Rev	A · 2026-10-08 · 施工图 (待持证电工 / 水工复核)

二层墙面立面 Wall elevations 1:50


2E31 · 衣帽间 · 北墙

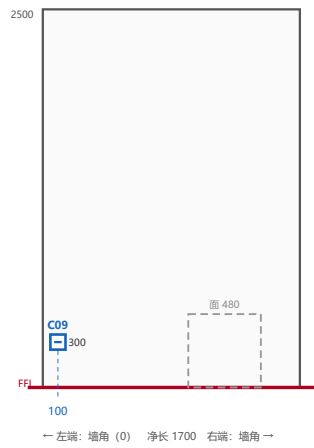

2E32 · 衣帽间门旁 · 北墙

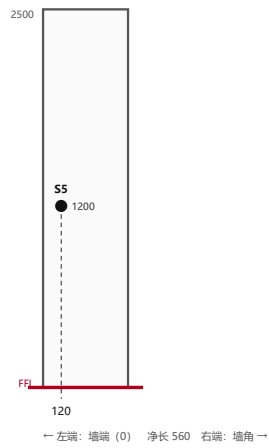

2E33 · 卧室2 门旁 (门西侧短墙, 卧室2 一侧, 锁侧) · 东墙

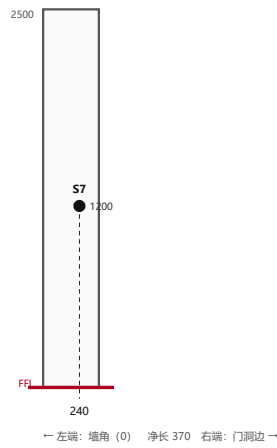

项目 Project	27PR 住宅改造 · 27 Penrith Road
图名 Title	二层墙面立面 Wall elevations 1:50
图号 Sheet	SO-17 比例 1:50 立面 @A3
专业 Discipline	电气定位 Setting out
版次 Rev	A · 2026-10-08 · 施工图 (待持证电工 / 水工复核)