

点位定位尺寸图 说明 Setting-out notes

怎么读这套图

- 每个点位有编号：C 插座、D 专用电器 / FCU / 隔离开关、S 开关、L 灯、N 新增。编号前的 1 / 2 表示一层 / 二层（表里另列楼层）。
- 墙面名称按「站在房间里看这面墙」：北墙 / 南墙 / 西墙 / 东墙（前门朝西、后花园在东）。
- 水平尺寸：从这面墙「左端」量到点位中心（面对墙看的左边边），同时给出到右端的距离，两个数加起来 = 这面墙的净长，可用来核对。  
左 / 右端是什么也写出来了：墙角（阴角） / 门洞边 / 窗洞边 / 墙端（阳角）。量的是完成墙面，抹灰 / 石膏板后的面。
- 高度：从该房间完成地面量到底盒中心（灯为天花高度）。二层前部完成面 3.208、后部（卧室 4 / 后卫 / 书房二）2.852，各自从本房间地面起量。
- 天花板上的灯：给出到两个方向最近墙面（或门窗洞）的距离。
- 立面图（SO-1x）：每面有点位的墙一张，平面图上的 1E05 / 2E12 等就是立面编号，箭头指向被看的那面墙。

高度标准（底盒中心，离本房间完成地面）

| 项                  | 高度 mm             | 依据                                                      |
|--------------------|-------------------|---------------------------------------------------------|
| 开关（全部）             | 1200              | 原施工图 / 模型 v42；Part M 450–1200。叠放的开关（S5 在 S4 上方）中心再高 130 |
| 一般插座               | 300               | 业主原定，与模型一致                                              |
| 床头插座 / 床头开关        | 630 / 650 / 700   | 床头柜面（主卧 485、卧室 2 500，模型 v42）+ 约 150；主卧 S3 在床头柜上方 700    |
| 厨房台面插座 / FCU       | 1100              | 台面 902（模型）上方，底边离台面约 150；FCU 同高、装在可触及处                   |
| 餐边柜 / 洗衣柜 / 书桌上方   | 1110 / 1200 / 970 | 柜面或桌面（907 / 1002 / 766）+ 200                            |
| 电视柜上方插座            | 600               | 原位置被电视柜（高 452）挡住，抬到柜面上方                                 |
| 空调插座               | 2190 / 2540       | 在内机侧面，与机身中高齐平（内机底：卧室 3 2040、卧室 4 2390，模型 v42）           |
| 户外插座               | 600               | 户外 IP66 带盖                                              |
| EV 充电桩 / 室内 40A 总控 | 1000 / 1200       | 按充电桩说明书；隔离开关 1200                                       |
| 壁灯                 | 按模型               | 楼梯壁灯 F32 1930；后花园壁灯 1770–1800；投光灯 3350（模型 v42 灯具中心）     |

图例

插座

专用 / FCU

开关

灯

给排水点

新增

精度与误差（重要）

- 点位来源：照明 / 插座设计（网页工具 Rev J、PPT 标注）+ Blender 模型 v42 的墙体、门窗、家具。图上点位标在墙边，本稿已把每个点「推」到所属墙面，再从墙端量尺寸，取整到 10 mm。
- 估计误差：插座 / 开关 / 灯水平位置 ±30 mm（原标注是示意位置）；表中「原点离墙面 xxx」= 原图标记离墙较远，已按墙面定位，请重点确认这些点在哪一面墙。
- 高度为设计值，按本图施工；家具、洁具定版后若尺寸变化，床头 / 台面 / 洁具相关点位跟着调整。墙体以现场完成面为准，与图差 > 50 mm 时先停工联系业主。
- 「离墙角 / 洞口 < 100」的点：贴得太近，门框 / 踢脚线 / 墙角可能装不下底盒，现场定位时请移到 ≥ 150。



核对后的处理（业主 2026-10-08 定稿）

- 高度：开关 1200、普通插座 300（与原施工图 / 模型一致）；床头插座 = 床头柜面 + 150，台面插座离台面约 150；S5 叠在 S4 正上方（1330）。
- 智能马桶 / 电热毛巾架电源：西卫 N-WC1、N-TR1；北卫马桶 + 毛巾架共用 N-TR2 双联出线面板（毛巾架挪到马桶旁后墙）。FCU 13A 都装在卫生间门外开关旁。
- 一层 C02 / C15 / C21 / C25 / C27 / C28 / C34 / S3 按模型位置（业主 2026-10-01 现场定）。
- 二层 S3（主卧主灯，与门口 S4 双控）：放在 C19 一侧床头柜上方 700，避开床头板。
- 被家具挡住的插座已挪开：电视柜后抬到 600；沙发、衣架、床、梳妆台、矮柜后的挪到家具外侧 150。
- 一层客厅 / 起居室之间的沙发墙已按模型 v42 补齐。

|               |                                    |
|---------------|------------------------------------|
| 项目 Project    | 27PR 住宅改造 · 27 Penrith Road        |
| 图名 Title      | 点位定位尺寸图 说明 Setting-out notes       |
| 图号 Sheet      | SO-00 比例 — @A3                     |
| 专业 Discipline | 电气定位 Setting out                   |
| 版次 Rev        | A · 2026-10-08 · 施工图（待持证电工 / 水工复核） |

一层点位定位总平面 Setting-out plan

0 2 m

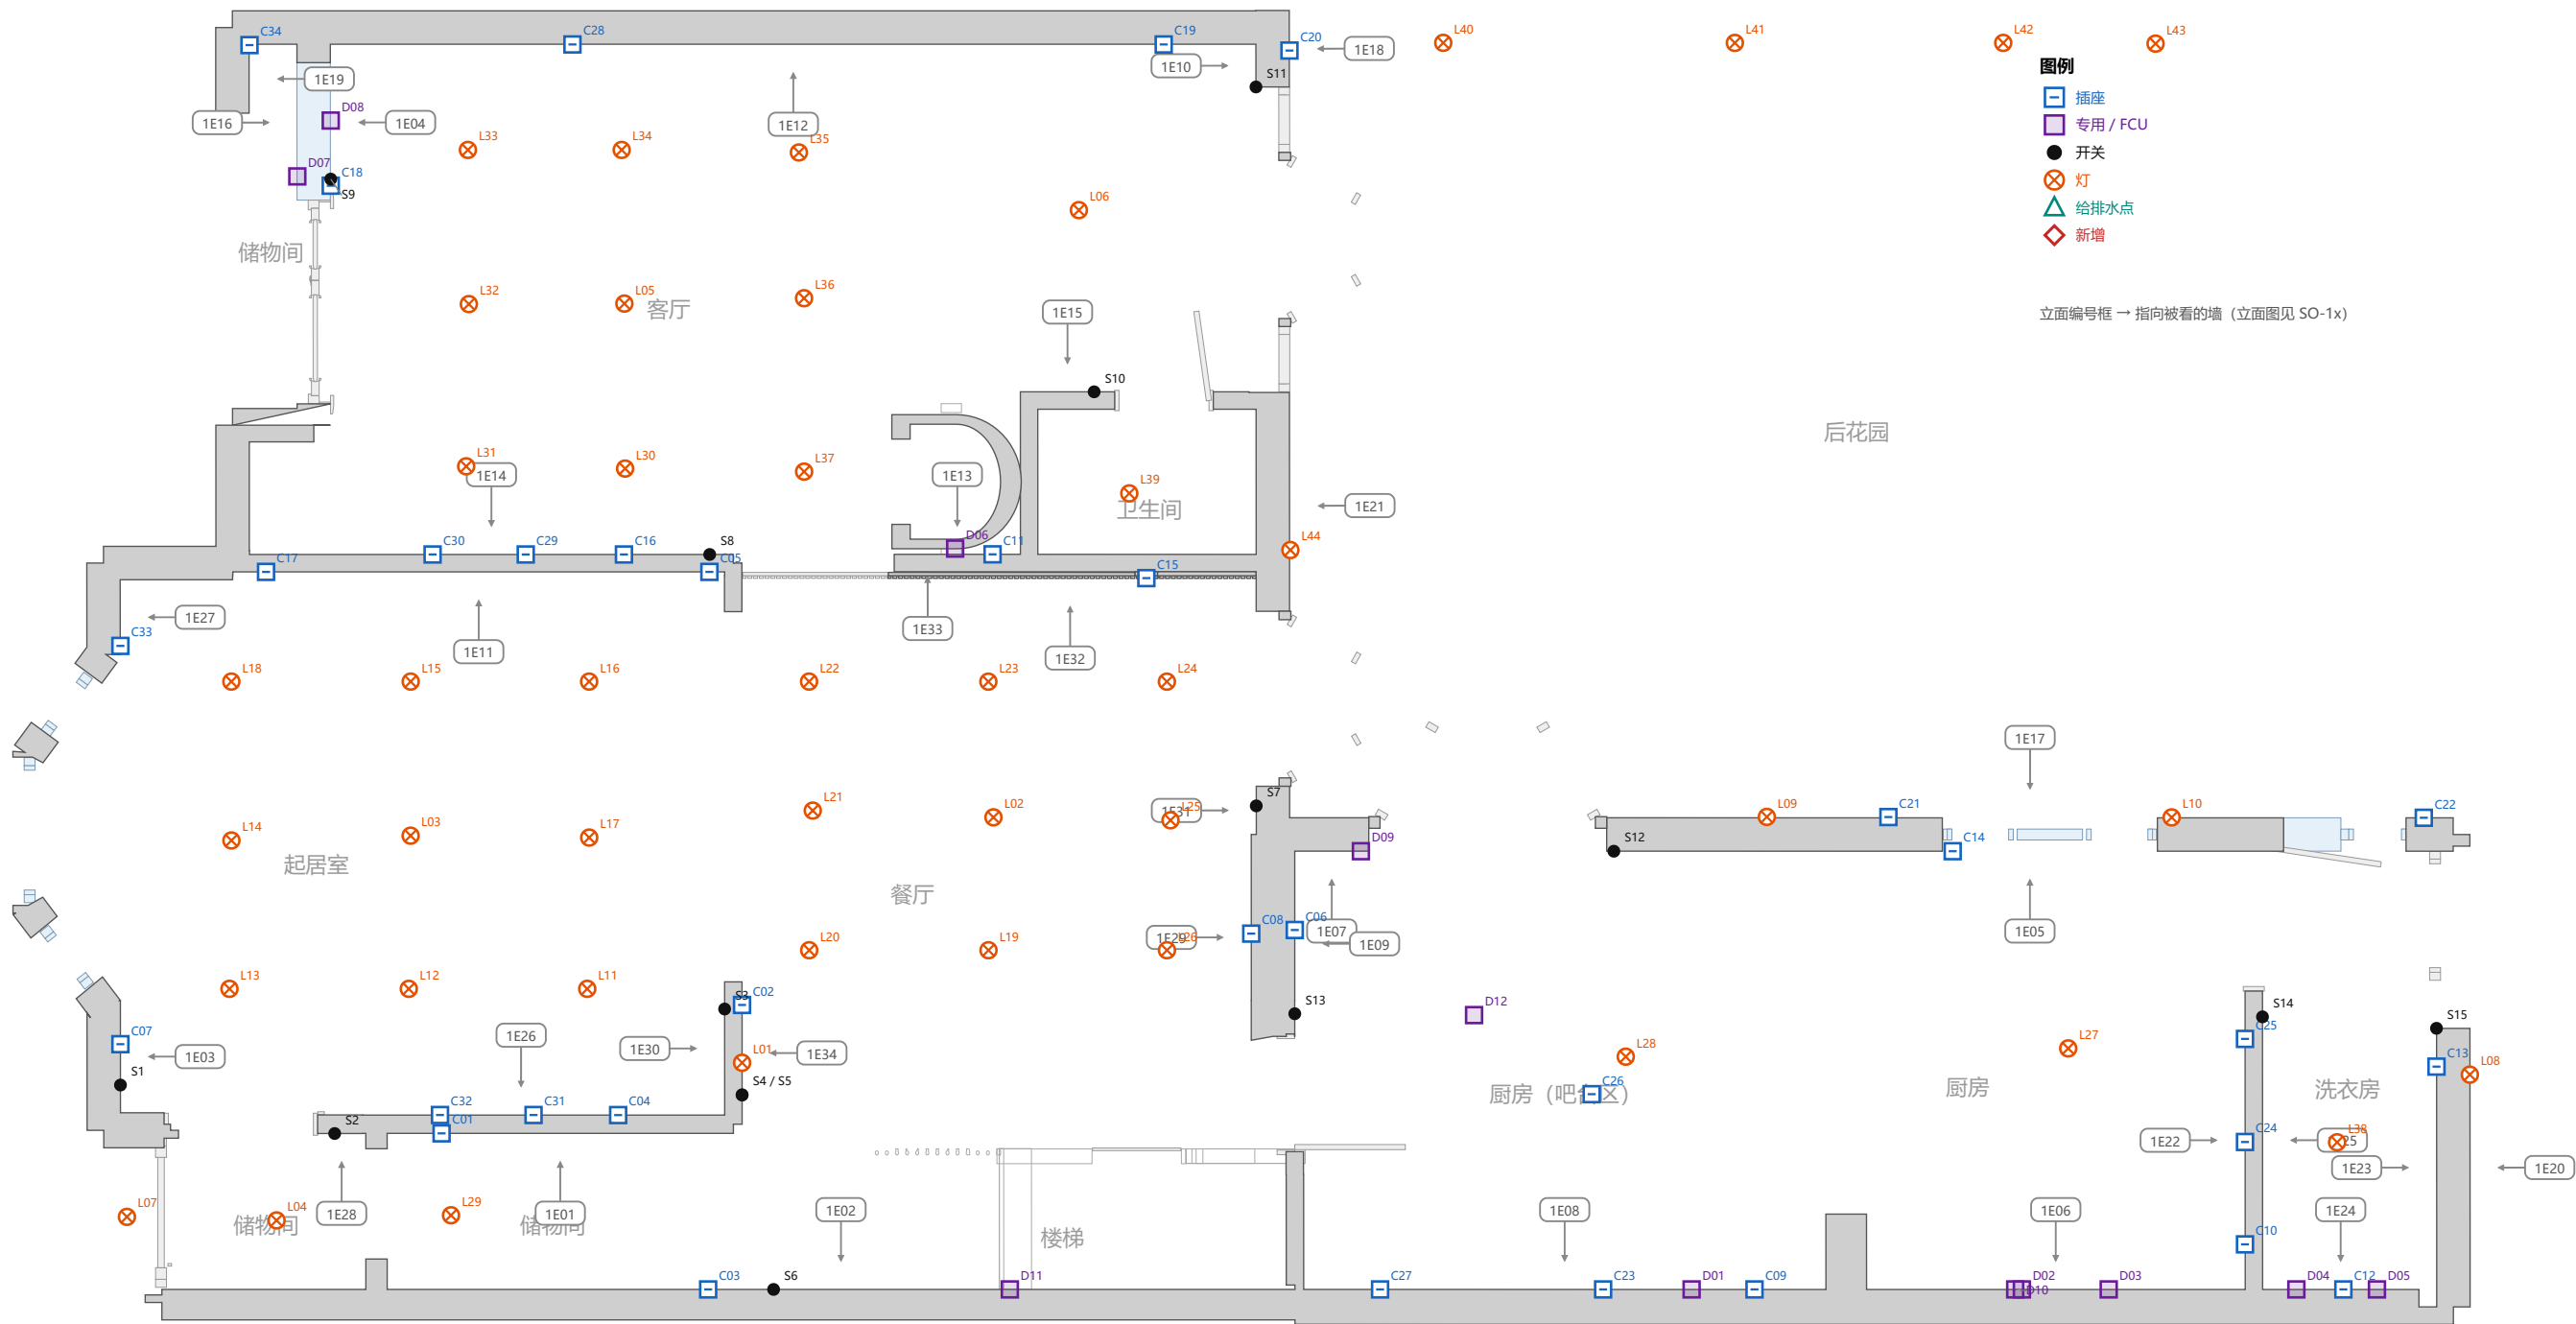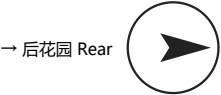

图例

- 插座
- 专用 / FCU
- 开关
- 灯
- 给排水点
- 新增



立面编号框 → 指向被看的墙 (立面图见 SO-1x)

说明 Notes

- 点位已推到所属墙面 (平面上的位置 = 墙面位置) ; 尺寸见定位表和立面图。
- 高度标准见 SO-00; 开关 1200、一般插座 300、床头 630 / 650、台面上方 1100。
- 给排水点位见给排水施工图。

|               |                                     |
|---------------|-------------------------------------|
| 项目 Project    | 27PR 住宅改造 · 27 Penrith Road         |
| 图名 Title      | 一层点位定位总平面 Setting-out plan          |
| 图号 Sheet      | SO-01 比例 1:50 @A3                   |
| 专业 Discipline | 电气定位 Setting out                    |
| 版次 Rev        | A · 2026-10-08 · 施工图 (待持证电工 / 水工复核) |

二层点位定位总平面 Setting-out plan

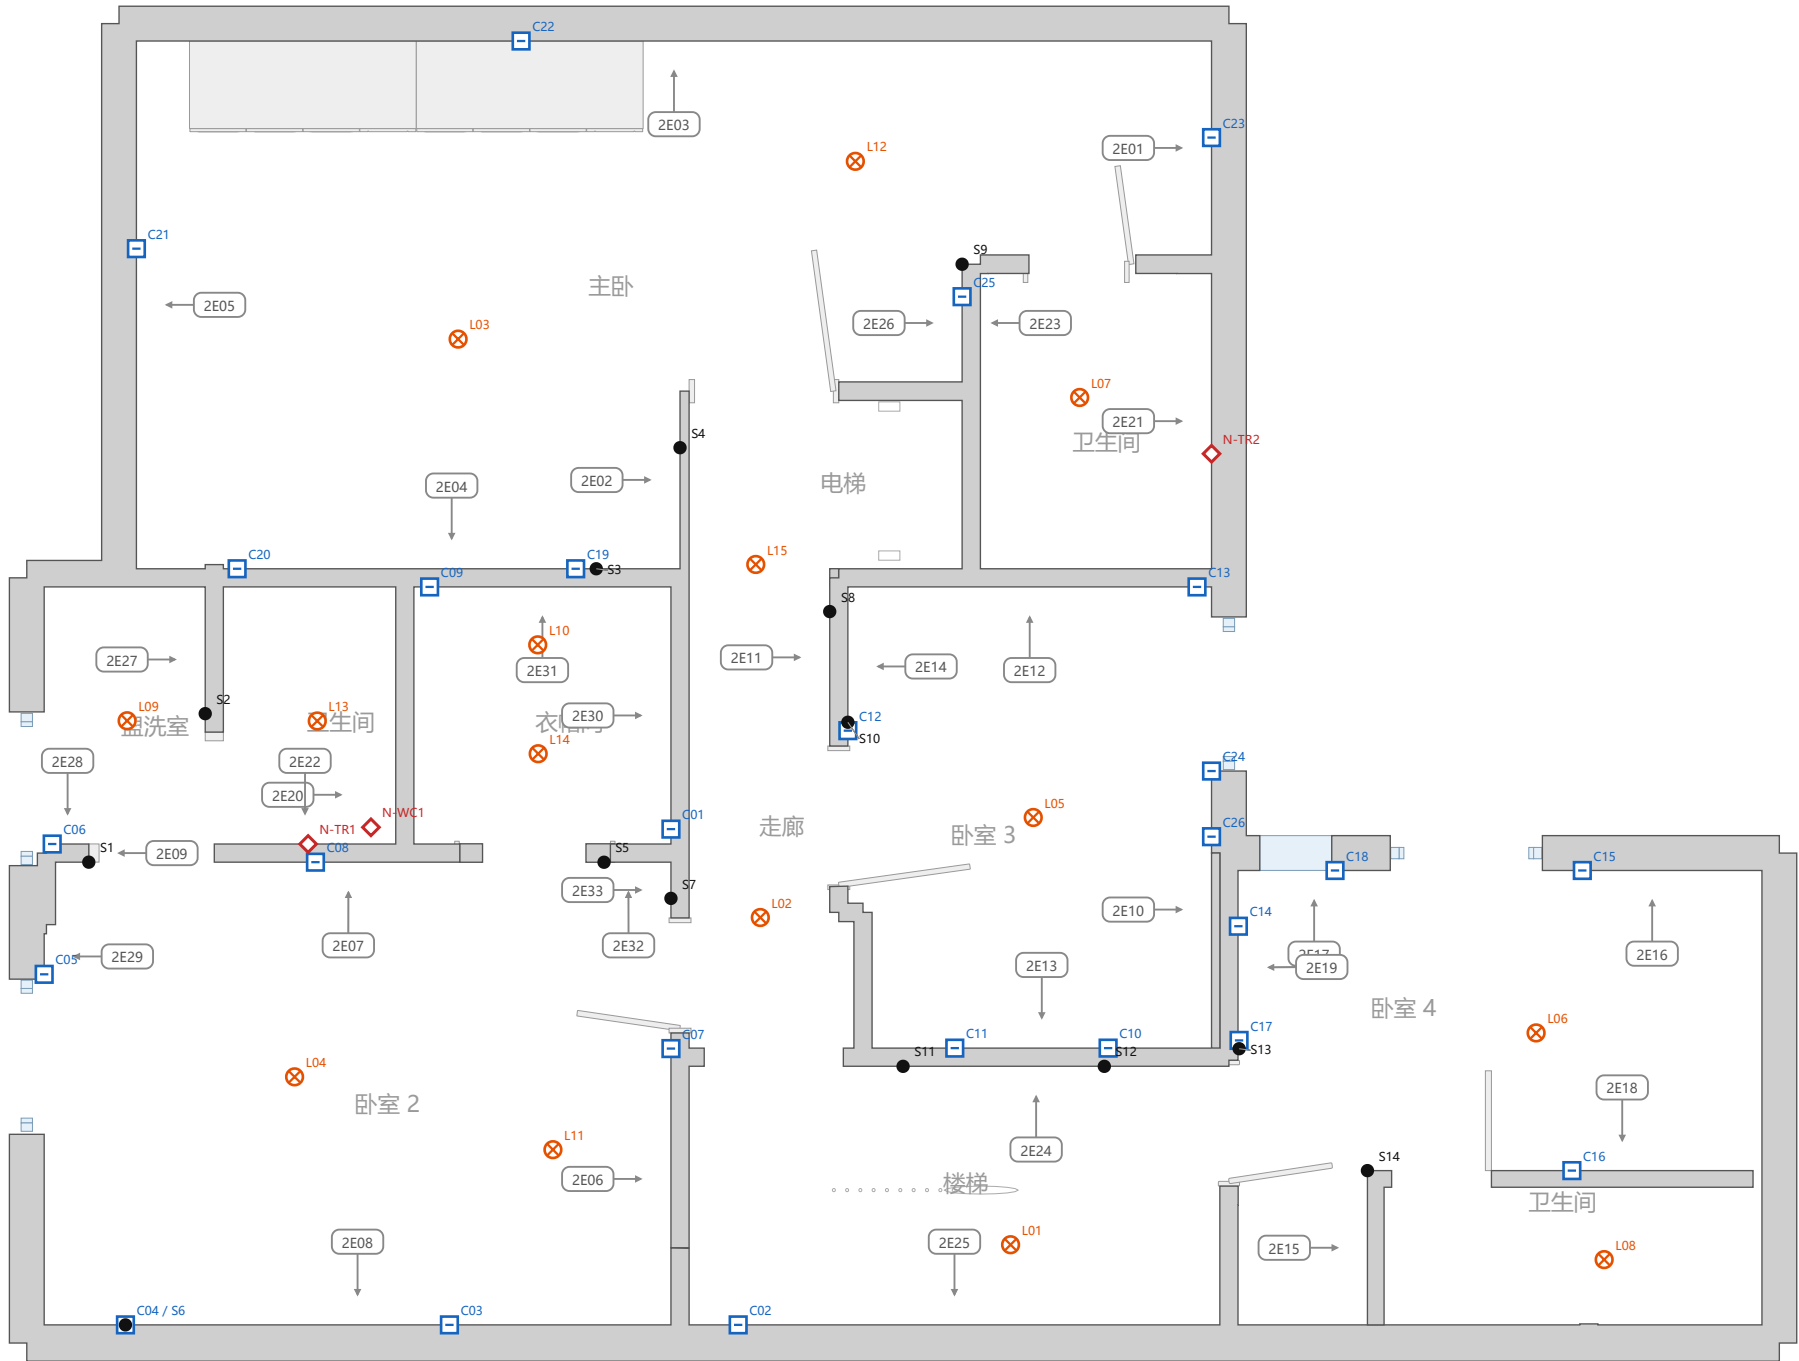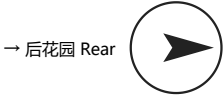

图例

- 插座
- 专用 / FCU
- 开关
- 灯
- 给排水点
- 新增

立面编号框 → 指向被看的墙 (立面图见 SO-1x)

说明 Notes

- 点位已推到所属墙面 (平面上的位置 = 墙面位置) ; 尺寸见定位表和立面图。
- 高度标准见 SO-00; 开关 1200、一般插座 300、床头 630 / 650、台面上方 1100。
- 给排水点位见给排水施工图。

|               |                                     |
|---------------|-------------------------------------|
| 项目 Project    | 27PR 住宅改造 · 27 Penrith Road         |
| 图名 Title      | 二层点位定位总平面 Setting-out plan          |
| 图号 Sheet      | SO-02 比例 1:50 @A3                   |
| 专业 Discipline | 电气定位 Setting out                    |
| 版次 Rev        | A · 2026-10-08 · 施工图 (待持证电工 / 水工复核) |

一层墙面点位定位表（插座 / 开关 / 专用 / 壁灯）

一层墙面点位定位表（插座 / 开关 / 专用 / 壁灯）（尺寸 mm；距左 / 右端 = 面对墙看的左 / 右；高度 = 底盒中心离本房间完成地面）

| 编号  | 类型 / 名称                         | 房间                         | 墙面（立面）   | 距左端 mm   | 距右端 mm   | 高度   | 依据 / 备注                                                        |
|-----|---------------------------------|----------------------------|----------|----------|----------|------|----------------------------------------------------------------|
| S1  | 开关 · 4 联开关 · 键 3/4/5/6          | 门厅 · 前门内侧                  | 西墙（1E03） | 墙角 190   | 窗洞边 580  | 1200 | 开关中心 1100                                                      |
| S2  | 开关 · 2 联开关 · 键 1/2              | 门厅 · 前储物间旁                 | 北墙（1E28） | 门洞边 120  | 墙角 210   | 1200 | 开关中心 1100                                                      |
| S3  | 开关 · 3 联开关 · 键 23/24/25         | 起居室侧 · 拱门旁                 | 东墙（1E30） | 墙端 190   | 墙角 730   | 1200 | 开关中心 1100                                                      |
| S4  | 开关 · 4 联开关 · 键 18/19/20/21      | 楼梯口 · 拱门旁（与 S5 上下叠放，S4 在下） | 西墙（1E34） | 墙端 200   | 墙端 780   | 1200 | 开关中心 1100                                                      |
| S5  | 开关 · 3 联开关 · 键 7/8/9（叠在 S4 正上方） | G07 区侧 · 拱门旁（叠在 S4 正上方）    | 西墙（1E34） | 墙端 200   | 墙端 780   | 1330 | 开关中心 1100                                                      |
| S6  | 开关 · 1 联开关 · 键 30               | 楼梯底                        | 南墙（1E02） | 墙角 3590  | 墙角 2660  | 1200 | 开关中心 1100                                                      |
| S7  | 开关 · 3 联开关 · 键 26/27/28         | 法式门框东侧（后花园门旁）              | 东墙（1E31） | 墙端 130   | 墙角 200   | 1200 | 开关中心 1100                                                      |
| S8  | 开关 · 4 联开关 · 键 10/11/12/13      | G15 区南门旁                   | 南墙（1E14） | 墙端 160   | 墙角 3170  | 1200 | 开关中心 1100；原点离离墙面 290，已按墙面定位                                    |
| S9  | 开关 · 4 联开关 · 键 14/15/16/17      | G15 区 · 储物间门旁              | 西墙（1E04） | 门洞边 150  | 墙角 930   | 1200 | 开关中心 1100                                                      |
| S10 | 开关 · 1 联开关 · 键 22               | 卫生间门外                      | 南墙（1E15） | 门洞边 140  | 墙端 510   | 1200 | 开关中心 1100                                                      |
| S11 | 开关 · 3 联开关 · 键 26/27/28         | G15 区 · 通后花园门旁             | 东墙（1E10） | 墙角 290   | 墙端 0     | 1200 | 开关中心 1100；离墙角 / 洞口 < 100，现场确认                                  |
| S12 | 开关 · 3 联开关 · 键 26/27/28         | 厨房后门旁（吧台区）                 | 北墙（1E05） | 墙端 50    | 门洞边 5790 | 1200 | 开关中心 1100；原点离离墙面 250，已按墙面定位；离墙角 / 洞口 < 100，现场确认                |
| S13 | 开关 · 2 联开关 · 键 31/32            | 厨房入口                       | 西墙（1E09） | 门洞边 160  | 墙角 1120  | 1200 | 开关中心 1100；原点离离墙面 290，已按墙面定位                                    |
| S14 | 开关 · 1 联开关 · 键 38               | 洗衣房门旁                      | 西墙（1E25） | 墙角 1880  | 门洞边 180  | 1200 | 开关中心 1100                                                      |
| S15 | 开关 · 1 联开关 · 键 40               | 洗衣房后门旁                     | 东墙（1E23） | 墙端 0     | 墙角 1920  | 1200 | 开关中心 1100；原点离离墙面 250，已按墙面定位；离墙角 / 洞口 < 100，现场确认                |
| C01 | 插座 · 单联插座                       | 储物间                        | 北墙（1E01） | 墙角 380   | 墙端 2010  | 300  | 300（业主原定，与模型一致）                                                |
| C02 | 插座 · 单联插座                       | 餐厅                         | 西墙（1E34） | 墙端 820   | 墙端 160   | 300  | 300（业主原定，与模型一致）；位置按模型（业主现场定）                                   |
| C03 | 插座 · 双联插座                       | 储物间                        | 南墙（1E02） | 墙角 4040  | 墙角 2210  | 300  | 300（业主原定，与模型一致）                                                |
| C04 | 插座 · 双联插座                       | 起居室                        | 南墙（1E26） | 墙角 730   | 门洞边 2070 | 600  | 电视柜上方 600（原位置被电视柜挡住）                                           |
| C05 | 插座 · 双联插座                       | 客厅                         | 北墙（1E11） | 墙角 3290  | 墙角 100   | 300  | 300（业主原定，与模型一致）；已挪到家具外侧（原位置被家具挡住）；在 G09（高 900）后面会被挡住，建议移到侧边或抬高 |
| C06 | 插座 · 双联插座                       | 厨房（吧台区）                    | 西墙（1E09） | 门洞边 730  | 墙角 540   | 300  | 300（业主原定，与模型一致）；原点离离墙面 320，已按墙面定位                              |
| C07 | 插座 · 双联插座                       | 储物间                        | 西墙（1E03） | 墙角 470   | 窗洞边 300  | 300  | 300（业主原定，与模型一致）                                                |
| C08 | 插座 · 双联插座                       | 餐厅                         | 东墙（1E29） | 墙端 680   | 墙端 740   | 300  | 300（业主原定，与模型一致）；原点离离墙面 350，已按墙面定位                              |
| C09 | 插座 · 双联插座                       | 厨房（吧台区）                    | 南墙（1E08） | 南墙 490   | 墙角 3110  | 1100 | 台面 900 上方（底边离台面约 150）                                          |
| C10 | 插座 · 双联插座                       | 洗衣房                        | 东墙（1E22） | 门洞边 1750 | 墙角 310   | 1100 | 台面 900 上方（底边离台面约 150）                                          |
| C11 | 插座 · 单联插座                       | 客厅                         | 南墙（1E13） | 墙角 190   | 墙端 680   | 300  | 300（业主原定，与模型一致）                                                |
| C12 | 插座 · 双联插座                       | 洗衣房                        | 南墙（1E24） | 墙端 520   | 墙角 560   | 1200 | 台面 1000 上方（底边离台面约 150）                                         |
| C13 | 插座 · 双联插座                       | 洗衣房                        | 东墙（1E23） | 墙端 260   | 墙角 1660  | 300  | 300（业主原定，与模型一致）                                                |
| C14 | 插座 · 双联插座                       | 厨房                         | 北墙（1E05） | 墙端 2390  | 门洞边 3450 | 300  | 300（业主原定，与模型一致）                                                |
| C15 | 插座 · 双联插座                       | 餐厅                         | 北墙（1E32） | 门洞边 1780 | 墙端 730   | 300  | 300（业主原定，与模型一致）；位置按模型（业主现场定）                                   |
| C16 | 插座 · 双联插座                       | 客厅                         | 南墙（1E14） | 墙端 750   | 墙角 2580  | 600  | 电视柜上方 600（原位置被电视柜挡住）                                           |
| C17 | 插座 · 双联插座                       | 起居室                        | 北墙（1E11） | 墙角 230   | 墙角 3160  | 1110 | 台面 910 上方（底边离台面约 150）                                          |
| C18 | 插座 · 双联插座                       | 储物间                        | 西墙（1E04） | 门洞边 100  | 墙角 970   | 300  | 300（业主原定，与模型一致）；已挪到家具外侧（原位置被家具挡住）                              |
| C19 | 插座 · 双联插座                       | 客厅                         | 北墙（1E12） | 墙角 5740  | 墙角 640   | 300  | 300（业主原定，与模型一致）                                                |
| C20 | 插座 · 户外防水插座 IP66                | 户外                         | 西墙（1E18） | 门洞边 250  | 墙端 280   | 600  | 户外 600，防水盖朝下；原点离离墙面 330，已按墙面定位                                 |
| C21 | 插座 · 户外防水插座 IP66                | 户外                         | 南墙（1E17） | 墙端 3890  | 门洞边 1940 | 600  | 户外 600，防水盖朝下；位置按模型（业主现场定）                                      |
| C22 | 插座 · 户外防水插座 IP66                | 户外                         | 南墙（1E17） | 墙端 200   | 门洞边 5630 | 600  | 户外 600，防水盖朝下                                                   |
| C23 | 插座 · 双联插座                       | 厨房（吧台区）                    | 南墙（1E08） | 墙角 1530  | 墙角 2060  | 1100 | 台面 900 上方（底边离台面约 150）                                          |
| C24 | 插座 · 双联插座                       | 洗衣房                        | 东墙（1E22） | 门洞边 1040 | 墙角 1020  | 1100 | 台面 900 上方（底边离台面约 150）                                          |
| C25 | 插座 · 双联插座                       | 洗衣房                        | 东墙（1E22） | 门洞边 330  | 墙角 1730  | 300  | 300（业主原定，与模型一致）；位置按模型（业主现场定）                                   |
| C27 | 插座 · 双联插座                       | 厨房（吧台区）                    | 南墙（1E08） | 墙角 3070  | 墙角 530   | 300  | 300（业主原定，与模型一致）；位置按模型（业主现场定）                                   |
| C28 | 插座 · 双联插座                       | 客厅                         | 北墙（1E12） | 墙角 1670  | 墙角 4710  | 300  | 300（业主原定，与模型一致）；位置按模型（业主现场定）；在 G14（高 850）后面会被挡住，建议移到侧边或抬高      |
| C29 | 插座 · 双联插座                       | 客厅                         | 南墙（1E14） | 墙端 1430  | 墙角 1900  | 600  | 电视柜上方 600（原位置被电视柜挡住）                                           |
| C30 | 插座 · 双联插座                       | 储物间                        | 南墙（1E14） | 墙端 2070  | 墙角 1260  | 600  | 电视柜上方 600（原位置被电视柜挡住）                                           |
| C31 | 插座 · 双联插座                       | 起居室                        | 南墙（1E26） | 墙角 1320  | 门洞边 1490 | 600  | 电视柜上方 600（原位置被电视柜挡住）                                           |
| C32 | 插座 · 双联插座                       | 起居室                        | 南墙（1E26） | 墙角 1960  | 门洞边 840  | 600  | 电视柜上方 600（原位置被电视柜挡住）                                           |
| C33 | 插座 · 双联插座                       | 起居室                        | 西墙（1E27） | 窗洞边 60   | 墙角 450   | 1110 | 台面 910 上方（底边离台面约 150）；离墙角 / 洞口 < 100，现场确认                      |
| C34 | 插座 · 户外防水插座 IP66                | 户外                         | 西墙（1E19） | 墙端 470   | 墙角 0     | 600  | 户外 600，防水盖朝下；位置按模型（业主现场定）；离墙角 / 洞口 < 100，现场确认                  |
| D01 | 专用 / FCU · FCU 13A · 洗碗机        | 厨房（吧台区）                    | 南墙（1E08） | 墙角 920   | 墙端 2670  | 1100 | FCU 装在台面上方 / 相邻柜内可触及处                                          |
| D02 | 专用 / FCU · FCU 13A · 烤箱         | 厨房                         | 南墙（1E06） | 墙角 1540  | 墙角 1070  | 1100 | FCU 装在台面上方 / 相邻柜内可触及处                                          |
| D03 | 专用 / FCU · FCU 13A · 冰箱         | 厨房                         | 南墙（1E06） | 墙角 940   | 墙角 1670  | 1100 | FCU 装在台面上方 / 相邻柜内可触及处                                          |
| D04 | 专用 / FCU · FCU 13A · 洗衣机        | 洗衣房                        | 南墙（1E24） | 墙端 840   | 墙角 230   | 1100 | FCU 装在台面上方 / 相邻柜内可触及处                                          |
| D05 | 专用 / FCU · FCU 13A · 烘干机        | 洗衣房                        | 南墙（1E24） | 墙端 290   | 墙角 790   | 1100 | FCU 装在台面上方 / 相邻柜内可触及处                                          |
| D06 | 专用 / FCU · DP · 电梯              | 餐厅                         | 北墙（1E33） | 墙端 440   | 墙端 50    | 1200 | 电梯隔离开关：挪到 C11 旁直墙上（原位置在电梯旁 120 宽墙头）；高度以厂家为准                    |

|               |                                    |
|---------------|------------------------------------|
| 项目 Project    | 27PR 住宅改造 · 27 Penrith Road        |
| 图名 Title      | 一层墙面点位定位表（插座 / 开关 / 专用 / 壁灯）       |
| 图号 Sheet      | SO-03 比例 — @A3                     |
| 专业 Discipline | 电气定位 Setting out                   |
| 版次 Rev        | A · 2026-10-08 · 施工图（待持证电工 / 水工复核） |

# 一层墙面点位定位表（插座 / 开关 / 专用 / 壁灯）

一层墙面点位定位表（插座 / 开关 / 专用 / 壁灯）（尺寸 mm；距左 / 右端 = 面对墙看的左 / 右；高度 = 底盒中心离本房间完成地面）

| 编号  | 类型 / 名称                          | 房间      | 墙面（立面）   | 距左端 mm  | 距右端 mm   | 高度   | 依据 / 备注                                 |
|-----|----------------------------------|---------|----------|---------|----------|------|-----------------------------------------|
| D07 | 专用 / FCU · EV 充电桩（外墙）            | 户外      | 东墙（1E16） | 墙角 910  | 门洞边 170  | 1000 | 充电桩底座约 1000（按产品说明书）                     |
| D08 | 专用 / FCU · DP 40A · 充电桩总控        | 客厅      | 西墙（1E04） | 门洞边 550 | 墙角 520   | 1200 | 40A 双极隔离开关（充电桩室内总控）；离门洞边 550，与 S9 错开    |
| D09 | 专用 / FCU · 锅炉 FCU 3A + 软水机插座（双联） | 厨房（吧台区） | 北墙（1E07） | 墙角 460  | 墙端 50    | 700  | 软水机旁，一块双联面板：锅炉 FCU 3A（固定接线）+ 软水机 13A 插座 |
| D10 | 专用 / FCU · 抽油烟机高位插座              | 厨房      | 南墙（1E06） | 墙角 1580 | 墙角 1020  | 2200 | 烟机罩内高位插座                                |
| D11 | 专用 / FCU · FCU 3A · 地暖分水器 UF1    | 楼梯      | 南墙（1E02） | 墙角 1960 | 墙角 4290  | 1100 | 分水器旁，给接线中心 + 混水泵供电；原点位离墙面 590，已按墙面定位    |
| L01 | 灯 · 壁灯 F32                       | 餐厅      | 西墙（1E34） | 墙端 420  | 墙端 560   | 1930 | 模型 v42 灯具中心高度（F32.001）                  |
| L08 | 灯 · 壁灯 G26_1（户外）                 | 户外      | 西墙（1E20） | 墙端 1600 | 墙端 320   | 1770 | 模型 v42 灯具中心高度（G26_1）；原点位离墙面 440，已按墙面定位  |
| L09 | 灯 · 壁灯 G26_2（户外）                 | 户外      | 南墙（1E17） | 墙端 4730 | 门洞边 1100 | 1800 | 模型 v42 灯具中心高度（G26_2）                    |
| L10 | 灯 · 壁灯 G26_3（户外）                 | 户外      | 南墙（1E17） | 墙端 1940 | 门洞边 3890 | 1800 | 模型 v42 灯具中心高度（G26_3）                    |
| L44 | 灯 · 壁灯 G26_4（户外）                 | 户外      | 西墙（1E21） | 门洞边 480 | 门洞边 1090 | 3350 | 模型 v42 灯具中心高度（G26_4 FloodLight_SOLLA）   |

|               |                                    |
|---------------|------------------------------------|
| 项目 Project    | 27PR 住宅改造 · 27 Penrith Road        |
| 图名 Title      | 一层墙面点位定位表（插座 / 开关 / 专用 / 壁灯）       |
| 图号 Sheet      | SO-04 比例 — @A3                     |
| 专业 Discipline | 电气定位 Setting out                   |
| 版次 Rev        | A · 2026-10-08 · 施工图（待持证电工 / 木工复核） |

一层天花灯位 / 地面点位定位表

一层天花灯位 / 地面点位定位表 (尺寸 mm; 距左 / 右端 = 面对墙看的左 / 右; 高度 = 底盒中心离本房间完成地面)

| 编号  | 类型 / 名称                 | 房间       | 位置   | 南北向: 距墙 | 东西向: 距墙   | 高度   | 备注                             |
|-----|-------------------------|----------|------|---------|-----------|------|--------------------------------|
| C26 | 插座 · 单联插座               | 厨房 (吧台区) | 岛台   | 南墙 1350 | 东墙 4500   | 800  | 岛台端板插座 h 800 (或改台面弹起插座)        |
| D12 | 专用 / FCU · 温感 + 一氧化碳报警器 | 厨房 (吧台区) | 天花   | 南墙 1890 | 西墙 1240   | 2600 | 厨房天花, 市电, 接一层照明回路; 距锅炉水平 1~3 m |
| L02 | 灯 · 主灯 G07              | 餐厅       | 天花   | 北墙 1650 | 东墙 1810   | 2600 | 天花安装 (吸顶 / 吊灯线盒)               |
| L03 | 灯 · 主灯 G06              | 起居室      | 天花   | 北墙 1820 | 东墙 5790   | 2600 | 天花安装 (吸顶 / 吊灯线盒)               |
| L04 | 灯 · 主灯 G08              | 储物间      | 天花   | 南墙 480  | 东墙 6960   | 2600 | 天花安装 (吸顶 / 吊灯线盒)               |
| L05 | 灯 · 主灯 G15              | 客厅       | 天花   | 南墙 1730 | 西门窗洞 2000 | 2600 | 天花安装 (吸顶 / 吊灯线盒)               |
| L06 | 灯 · 主灯 G16              | 客厅       | 天花   | 北墙 1140 | 西门窗洞 5140 | 2600 | 天花安装 (吸顶 / 吊灯线盒)               |
| L07 | 灯 · 门廊吊灯 G25 (户外)       | 户外       | 天花   | 南墙 470  | 东门窗洞 200  | 2600 | 吊在门廊顶 (模型 v42 顶高 2600)         |
| L11 | 灯 · GU10 筒灯             | 起居室      | 天花   | 南墙 870  | 东墙 950    | 2600 | 天花安装 (吸顶 / 吊灯线盒)               |
| L12 | 灯 · GU10 筒灯             | 起居室      | 天花   | 南墙 870  | 东墙 2180   | 2600 | 天花安装 (吸顶 / 吊灯线盒)               |
| L13 | 灯 · GU10 筒灯             | 起居室      | 天花   | 南墙 2070 | 东墙 3410   | 2600 | 天花安装 (吸顶 / 吊灯线盒)               |
| L14 | 灯 · GU10 筒灯             | 起居室      | 天花   | 北墙 1800 | 东墙 7030   | 2600 | 天花安装 (吸顶 / 吊灯线盒)               |
| L15 | 灯 · GU10 筒灯             | 起居室      | 天花   | 北墙 760  | 西门窗洞 2060 | 2600 | 天花安装 (吸顶 / 吊灯线盒)               |
| L16 | 灯 · GU10 筒灯             | 起居室      | 天花   | 北墙 760  | 西门窗洞 3290 | 2600 | 天花安装 (吸顶 / 吊灯线盒)               |
| L17 | 灯 · GU10 筒灯             | 起居室      | 天花   | 北墙 1830 | 东墙 4560   | 2600 | 天花安装 (吸顶 / 吊灯线盒)               |
| L18 | 灯 · GU10 筒灯             | 起居室      | 天花   | 北墙 700  | 西门窗洞 820  | 2600 | 天花安装 (吸顶 / 吊灯线盒)               |
| L19 | 灯 · GU10 筒灯             | 餐厅       | 天花   | 南墙 2340 | 东墙 1810   | 2600 | 天花安装 (吸顶 / 吊灯线盒)               |
| L20 | 灯 · GU10 筒灯             | 餐厅       | 天花   | 南墙 2340 | 东墙 3050   | 2600 | 天花安装 (吸顶 / 吊灯线盒)               |
| L21 | 灯 · GU10 筒灯             | 餐厅       | 天花   | 南墙 3300 | 东墙 3060   | 2600 | 天花安装 (吸顶 / 吊灯线盒)               |
| L22 | 灯 · GU10 筒灯             | 餐厅       | 天花   | 南墙 4190 | 西门窗洞 4800 | 2600 | 天花安装 (吸顶 / 吊灯线盒)               |
| L23 | 灯 · GU10 筒灯             | 餐厅       | 天花   | 北墙 710  | 西门窗洞 6040 | 2600 | 天花安装 (吸顶 / 吊灯线盒)               |
| L24 | 灯 · GU10 筒灯             | 餐厅       | 天花   | 北墙 710  | 西门窗洞 7270 | 2600 | 天花安装 (吸顶 / 吊灯线盒)               |
| L25 | 灯 · GU10 筒灯             | 餐厅       | 天花   | 北墙 1670 | 东墙 590    | 2600 | 天花安装 (吸顶 / 吊灯线盒)               |
| L26 | 灯 · GU10 筒灯             | 餐厅       | 天花   | 北墙 2560 | 东墙 580    | 2600 | 天花安装 (吸顶 / 吊灯线盒)               |
| L27 | 灯 · 主灯位 (灯具待选)          | 厨房       | 天花   | 南墙 1660 | 东墙 1220   | 2600 | 天花安装 (吸顶 / 吊灯线盒)               |
| L28 | 灯 · 主灯位 (灯具待选)          | 厨房 (吧台区) | 天花   | 北墙 1420 | 东墙 4270   | 2600 | 天花安装 (吸顶 / 吊灯线盒)               |
| L29 | 灯 · GU10 筒灯             | 储物间      | 天花   | 南墙 510  | 东墙 5760   | 2600 | 天花安装 (吸顶 / 吊灯线盒)               |
| L30 | 灯 · GU10 筒灯             | 客厅       | 天花   | 南墙 590  | 东墙 2580   | 2600 | 天花安装 (吸顶 / 吊灯线盒)               |
| L31 | 灯 · GU10 筒灯             | 客厅       | 天花   | 南墙 610  | 西墙 1490   | 2600 | 天花安装 (吸顶 / 吊灯线盒)               |
| L32 | 灯 · GU10 筒灯             | 客厅       | 天花   | 南墙 1730 | 西门窗洞 930  | 2600 | 天花安装 (吸顶 / 吊灯线盒)               |
| L33 | 灯 · GU10 筒灯             | 客厅       | 天花   | 北墙 730  | 西墙 950    | 2600 | 天花安装 (吸顶 / 吊灯线盒)               |
| L34 | 灯 · GU10 筒灯             | 客厅       | 天花   | 北墙 730  | 西墙 2010   | 2600 | 天花安装 (吸顶 / 吊灯线盒)               |
| L35 | 灯 · GU10 筒灯             | 客厅       | 天花   | 北墙 740  | 西墙 3230   | 2600 | 天花安装 (吸顶 / 吊灯线盒)               |
| L36 | 灯 · GU10 筒灯             | 客厅       | 天花   | 北墙 1750 | 西门窗洞 3240 | 2600 | 天花安装 (吸顶 / 吊灯线盒)               |
| L37 | 灯 · GU10 筒灯             | 客厅       | 天花   | 北墙 2940 | 东墙 1350   | 2600 | 天花安装 (吸顶 / 吊灯线盒)               |
| L38 | 灯 · GU10 筒灯             | 洗衣房      | 天花   | 南墙 1010 | 西墙 510    | 2600 | 天花安装 (吸顶 / 吊灯线盒)               |
| L39 | 灯 · GU10 筒灯             | 卫生间      | 天花   | 南墙 420  | 西墙 630    | 2600 | 天花安装 (吸顶 / 吊灯线盒)               |
| L40 | 灯 · 围栏地灯 (户外)           | 户外       | 室外地面 | 南墙 8590 | 西墙 1060   | 0    | 地面安装, SWA 埋地 ≥ 450             |
| L41 | 灯 · 围栏地灯 (户外)           | 户外       | 室外地面 | 南墙 5340 | 西墙 3070   | 0    | 地面安装, SWA 埋地 ≥ 450             |
| L42 | 灯 · 围栏地灯 (户外)           | 户外       | 室外地面 | 南墙 5340 | 西墙 4920   | 0    | 地面安装, SWA 埋地 ≥ 450             |
| L43 | 灯 · 围栏地灯 (户外)           | 户外       | 室外地面 | 南墙 5340 | 西墙 5970   | 0    | 地面安装, SWA 埋地 ≥ 450             |

|               |                                     |
|---------------|-------------------------------------|
| 项目 Project    | 27PR 住宅改造 · 27 Penrith Road         |
| 图名 Title      | 一层天花灯位 / 地面点位定位表                    |
| 图号 Sheet      | SO-05 比例 — @A3                      |
| 专业 Discipline | 电气定位 Setting out                    |
| 版次 Rev        | A · 2026-10-08 · 施工图 (待持证电工 / 木工复核) |

二层墙面点位定位表（插座 / 开关 / 专用 / 壁灯）

二层墙面点位定位表（插座 / 开关 / 专用 / 壁灯）（尺寸 mm；距左 / 右端 = 面对墙看的左 / 右；高度 = 底盒中心离本房间完成地面）

| 编号    | 类型 / 名称                        | 房间                               | 墙面（立面）   | 距左端 mm   | 距右端 mm   | 高度   | 依据 / 备注                                                                             |
|-------|--------------------------------|----------------------------------|----------|----------|----------|------|-------------------------------------------------------------------------------------|
| S1    | 开关 · 1 联开关 · 键 6               | 盥洗室门旁                            | 西墙（2E09） | 门洞边 0    | 门洞边 120  | 1200 | 开关中心 1100；离墙角 / 洞口 < 100，现场确认                                                       |
| S2    | 开关 · 1 联开关 · 键 6+              | 西卫生间门外                           | 东墙（2E27） | 墙角 840   | 门洞边 120  | 1200 | 开关中心 1100                                                                           |
| S3    | 开关 · 1 联开关 · 键 2               | 主卧床头柜上方（C19 一侧，离地 700，与门口 S4 双控） | 南墙（2E04） | 墙角 550   | 墙角 2470  | 700  | 开关中心 1100                                                                           |
| S4    | 开关 · 2 联开关 · 键 10/11           | 主卧东墙 · 床头侧                       | 东墙（2E02） | 门洞边 370  | 墙角 800   | 1200 | 开关中心 1100                                                                           |
| S5    | 开关 · 1 联开关 · 键 5               | 衣帽间门旁                            | 北墙（2E32） | 墙端 120   | 墙角 440   | 1200 | 开关中心 1100                                                                           |
| S6    | 开关 · 2 联开关 · 键 12/13           | 卧室2 床头侧（东墙）                      | 南墙（2E08） | 墙角 3600  | 墙角 550   | 1200 | 开关中心 1100                                                                           |
| S7    | 开关 · 2 联开关 · 键 14/15           | 卧室2 门旁（门西侧短墙，卧室2 一侧，锁侧）          | 东墙（2E33） | 墙角 240   | 门洞边 130  | 1200 | 开关中心 1100                                                                           |
| S8    | 开关 · 1 联开关 · 键 3               | 走廊北端                             | 东墙（2E11） | 墙端 280   | 门洞边 890  | 1200 | 开关中心 1100                                                                           |
| S9    | 开关 · 1 联开关 · 键 1               | 北卫生间门外                           | 西墙（2E23） | 墙端 780   | 墙角 0     | 1200 | 开关中心 1100；原点离墙面 260，已按墙面定位；离墙角 / 洞口 < 100，现场确认                                      |
| S10   | 开关 · 1 联开关 · 键 4               | 卧室3 门旁                           | 西墙（2E14） | 门洞边 160  | 墙角 900   | 1200 | 开关中心 1100                                                                           |
| S11   | 开关 · 2 联开关 · 键 16/17           | 走廊南端 · 楼梯口                       | 北墙（2E24） | 墙端 400   | 门洞边 2150 | 1200 | 开关中心 1100                                                                           |
| S12   | 开关 · 1 联开关 · 键 7               | 楼梯顶                              | 北墙（2E24） | 墙端 1730  | 门洞边 820  | 1200 | 开关中心 1100                                                                           |
| S13   | 开关 · 1 联开关 · 键 8               | 卧室 4 门旁                          | 西墙（2E19） | 门洞边 100  | 墙角 1180  | 1200 | 开关中心 1100                                                                           |
| S14   | 开关 · 1 联开关 · 键 9               | 卧室 4 内 · 卫生间门南侧（隔墙短墙）            | 东墙（2E15） | 墙端 0     | 墙角 1020  | 1200 | 开关中心 1100；离墙角 / 洞口 < 100，现场确认                                                       |
| C01   | 插座 · 单联插座                      | 衣帽间                              | 东墙（2E30） | 墙角 1600  | 墙角 100   | 300  | 300（业主原定，与模型一致）；已挪到家具外侧（原位置被家具挡住）；离墙角 / 洞口 < 100，现场确认；在 F15（高 2100）后面会被挡住，建议移到侧边或抬高 |
| C02   | 插座 · 双联插座                      | 楼梯                               | 南墙（2E25） | 墙角 3190  | 墙角 320   | 300  | 300（业主原定，与模型一致）                                                                     |
| C03   | 插座 · 双联插座                      | 卧室 2                             | 南墙（2E08） | 墙角 1460  | 墙角 2680  | 650  | 床头柜面 500 + 150（略高于柜面）                                                               |
| C04   | 插座 · 双联插座                      | 卧室 2                             | 南墙（2E08） | 墙角 3610  | 墙角 540   | 650  | 床头柜面 500 + 150（略高于柜面）                                                               |
| C05   | 插座 · 双联插座                      | 盥洗室                              | 西墙（2E29） | 窗洞边 30   | 墙角 270   | 300  | 300（业主原定，与模型一致）；离墙角 / 洞口 < 100，现场确认                                                 |
| C06   | 插座 · 双联插座                      | 盥洗室                              | 南墙（2E28） | 门洞边 240  | 窗洞边 40   | 300  | 300（业主原定，与模型一致）；离墙角 / 洞口 < 100，现场确认                                                 |
| C07   | 插座 · 双联插座                      | 卧室 2                             | 东墙（2E06） | 门洞边 100  | 墙角 1830  | 300  | 300（业主原定，与模型一致）；已挪到家具外侧（原位置被家具挡住）                                                   |
| C08   | 插座 · 双联插座                      | 卧室 2                             | 北墙（2E07） | 墙端 670   | 墙端 1100  | 300  | 300（业主原定，与模型一致）                                                                     |
| C09   | 插座 · 单联插座                      | 衣帽间                              | 北墙（2E31） | 墙角 100   | 墙角 1600  | 300  | 300（业主原定，与模型一致）；已挪到家具外侧（原位置被家具挡住）；在 F15（高 2100）后面会被挡住，建议移到侧边或抬高                     |
| C10   | 插座 · 双联插座                      | 卧室 3                             | 南墙（2E13） | 门洞边 680  | 墙角 1560  | 970  | 台面 770 上方（底边离台面约 150）                                                               |
| C11   | 插座 · 双联插座                      | 卧室 3                             | 南墙（2E13） | 门洞边 1700 | 墙角 550   | 970  | 台面 770 上方（底边离台面约 150）                                                               |
| C12   | 插座 · 单联插座                      | 卧室 3                             | 西墙（2E14） | 门洞边 100  | 墙角 950   | 300  | 300（业主原定，与模型一致）；已挪到家具外侧（原位置被家具挡住）                                                   |
| C13   | 插座 · 双联插座                      | 卧室 3                             | 北墙（2E12） | 墙角 2310  | 墙角 100   | 300  | 300（业主原定，与模型一致）；已挪到家具外侧（原位置被家具挡住）；离墙角 / 洞口 < 100，现场确认                               |
| C14   | 插座 · 空调插座                      | 卧室 4                             | 西墙（2E19） | 门洞边 910  | 墙角 370   | 2540 | 空调内机侧面，与机身中高齐平（内机底 2390）                                                            |
| C15   | 插座 · 双联插座                      | 卧室 4                             | 北墙（2E16） | 窗洞边 260  | 墙角 1190  | 300  | 300（业主原定，与模型一致）                                                                     |
| C16   | 插座 · 双联插座                      | 卧室 4                             | 南墙（2E18） | 墙端 1200  | 门洞边 530  | 300  | 300（业主原定，与模型一致）                                                                     |
| C17   | 插座 · 双联插座                      | 卧室 4                             | 西墙（2E19） | 门洞边 160  | 墙角 1120  | 300  | 300（业主原定，与模型一致）                                                                     |
| C18   | 插座 · 双联插座                      | 卧室 4                             | 北墙（2E17） | 墙角 640   | 窗洞边 370  | 300  | 300（业主原定，与模型一致）                                                                     |
| C19   | 插座 · 双联插座                      | 主卧                               | 南墙（2E04） | 墙角 690   | 墙角 2330  | 630  | 床头柜面 480 + 150（略高于柜面）；数据里房间为「衣帽间」，按位置是主卧床头                                          |
| C20   | 插座 · 双联插座                      | 主卧                               | 南墙（2E04） | 墙角 2930  | 墙角 90    | 630  | 床头柜面 480 + 150（略高于柜面）；离墙角 / 洞口 < 100，现场确认                                           |
| C21   | 插座 · 双联插座                      | 主卧                               | 西墙（2E05） | 墙角 2120  | 墙角 1370  | 300  | 300（业主原定，与模型一致）                                                                     |
| C22   | 插座 · 双联插座                      | 主卧                               | 北墙（2E03） | 墙角 2540  | 墙角 4570  | 300  | 300（业主原定，与模型一致）                                                                     |
| C23   | 插座 · 双联插座                      | 主卧                               | 东墙（2E01） | 墙角 640   | 墙角 780   | 300  | 300（业主原定，与模型一致）                                                                     |
| C24   | 插座 · 空调插座                      | 卧室 3                             | 东墙（2E10） | 窗洞边 0    | 门洞边 1830 | 2190 | 空调内机侧面，与机身中高齐平（内机底 2040）；离墙角 / 洞口 < 100，现场确认                                        |
| C25   | 插座 · 单联插座                      | 电梯                               | 东墙（2E26） | 墙端 210   | 墙角 560   | 300  | 300（业主原定，与模型一致）                                                                     |
| C26   | 插座 · 双联插座                      | 卧室 3                             | 东墙（2E10） | 窗洞边 430  | 门洞边 1400 | 300  | 300（业主原定，与模型一致）                                                                     |
| N-TR1 | 新增 · 西卫电热毛巾架出线面板（新增）           | 卫生间                              | 南墙（2E22） | 墙角 580   | 墙端 620   | 1100 | 毛巾架下沿旁出线面板（模型位置），FCU 13A 装在卫生间外 h 1100                                              |
| N-TR2 | 新增 · 北卫智能马桶 + 电热毛巾架出线面板（双联，新增） | 卫生间                              | 东墙（2E21） | 窗洞边 1190 | 墙角 760   | 300  | 马桶与毛巾架之间的双联出线面板 h 300（毛巾架挪到马桶旁后墙，离马桶约 200）；两个 FCU 13A 装在卫生间门外 h 1100                |
| N-WC1 | 新增 · 西卫智能马桶电源出线面板（新增）          | 卫生间                              | 东墙（2E20） | 墙端 500   | 墙端 70    | 300  | 马桶侧后方出线面板 h 300，FCU 13A 装在卫生间外开关旁 h 1100                                            |

|               |                                    |
|---------------|------------------------------------|
| 项目 Project    | 27PR 住宅改造 · 27 Penrith Road        |
| 图名 Title      | 二层墙面点位定位表（插座 / 开关 / 专用 / 壁灯）       |
| 图号 Sheet      | SO-06 比例 — @A3                     |
| 专业 Discipline | 电气定位 Setting out                   |
| 版次 Rev        | A · 2026-10-08 · 施工图（待持证电工 / 水工复核） |

## 二层天花灯位 / 地面点位定位表


二层天花灯位 / 地面点位定位表 (尺寸 mm; 距左 / 右端 = 面对墙看的左 / 右; 高度 = 底盒中心离本房间完成地面)

| 编号  | 类型 / 名称        | 房间   | 位置 | 南北向: 距墙 | 东西向: 距墙 | 高度   | 备注               |
|-----|----------------|------|----|---------|---------|------|------------------|
| L01 | 灯 · 主灯 F06     | 楼梯   | 天花 | 南墙 530  | 东墙 1380 | 2500 | 天花安装 (吸顶 / 吊灯线盒) |
| L02 | 灯 · 主灯 F11     | 走廊   | 天花 | 南墙 2690 | 西墙 470  | 2500 | 天花安装 (吸顶 / 吊灯线盒) |
| L03 | 灯 · 主灯 F19     | 主卧   | 天花 | 南墙 1520 | 西墙 2130 | 2500 | 天花安装 (吸顶 / 吊灯线盒) |
| L04 | 灯 · 主灯 F20     | 卧室 2 | 天花 | 北墙 1420 | 东墙 2490 | 2500 | 天花安装 (吸顶 / 吊灯线盒) |
| L05 | 灯 · 主灯 F22     | 卧室 3 | 天花 | 北墙 1520 | 东墙 1180 | 2500 | 天花安装 (吸顶 / 吊灯线盒) |
| L06 | 灯 · 主灯 F23     | 卧室 4 | 天花 | 南墙 910  | 东墙 1490 | 2856 | 天花安装 (吸顶 / 吊灯线盒) |
| L07 | 灯 · GU10 筒灯    | 卫生间  | 天花 | 南墙 1130 | 西墙 660  | 2500 | 天花安装 (吸顶 / 吊灯线盒) |
| L08 | 灯 · GU10 筒灯    | 卫生间  | 天花 | 南墙 430  | 东墙 1040 | 2856 | 天花安装 (吸顶 / 吊灯线盒) |
| L09 | 灯 · GU10 筒灯    | 盥洗室  | 天花 | 北墙 880  | 东墙 520  | 2500 | 天花安装 (吸顶 / 吊灯线盒) |
| L10 | 灯 · GU10 筒灯    | 衣帽间  | 天花 | 北墙 380  | 西墙 820  | 2500 | 天花安装 (吸顶 / 吊灯线盒) |
| L11 | 灯 · GU10 筒灯    | 卧室 2 | 天花 | 南墙 1160 | 西墙 3360 | 2500 | 天花安装 (吸顶 / 吊灯线盒) |
| L12 | 灯 · 主灯位 (灯具待选) | 主卧   | 天花 | 北墙 800  | 东墙 2360 | 2500 | 天花安装 (吸顶 / 吊灯线盒) |
| L13 | 灯 · GU10 筒灯    | 卫生间  | 天花 | 南墙 810  | 东墙 490  | 2500 | 天花安装 (吸顶 / 吊灯线盒) |
| L14 | 灯 · GU10 筒灯    | 衣帽间  | 天花 | 北墙 1100 | 西墙 820  | 2500 | 天花安装 (吸顶 / 吊灯线盒) |
| L15 | 灯 · 主灯 F11#2   | 电梯   | 天花 | 北墙 3460 | 西墙 440  | 2500 | 天花安装 (吸顶 / 吊灯线盒) |


|               |                                     |
|---------------|-------------------------------------|
| 项目 Project    | 27PR 住宅改造 · 27 Penrith Road         |
| 图名 Title      | 二层天花灯位 / 地面点位定位表                    |
| 图号 Sheet      | SO-07 比例 — @A3                      |
| 专业 Discipline | 电气定位 Setting out                    |
| 版次 Rev        | A · 2026-10-08 · 施工图 (待持证电工 / 水工复核) |

一层墙面立面 Wall elevations 1:50


1E01 • 储物间 • 北墙

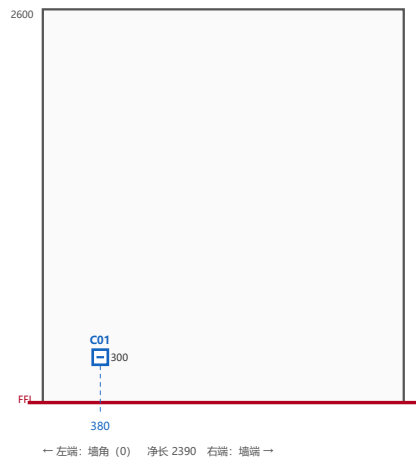


1E02 • 储物间 • 南墙

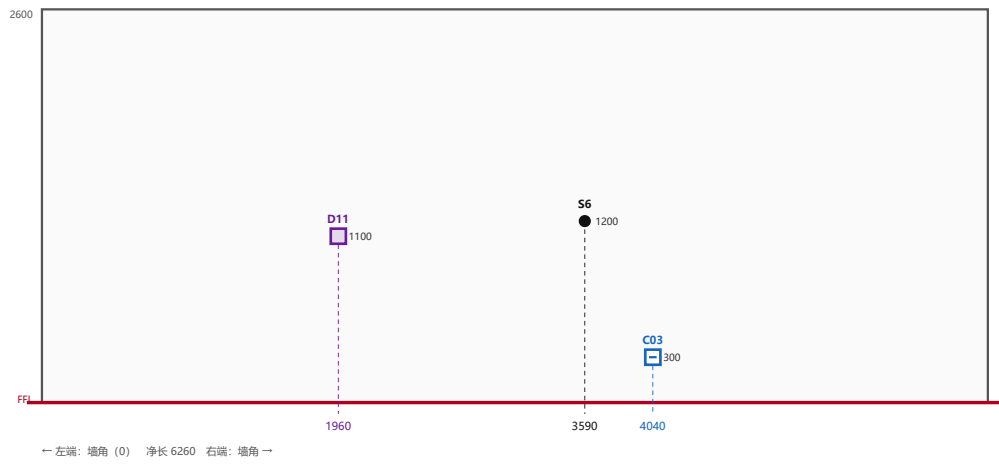


1E03 • 储物间 • 西墙

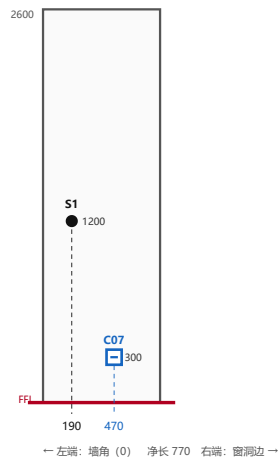


1E04 • 储物间 • 东墙

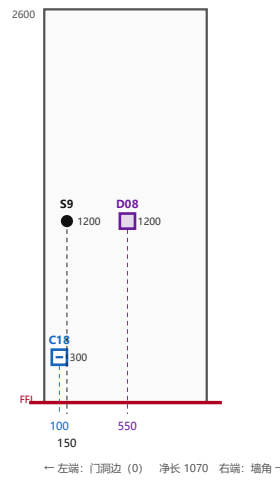


1E05 • 厨房 • 北墙

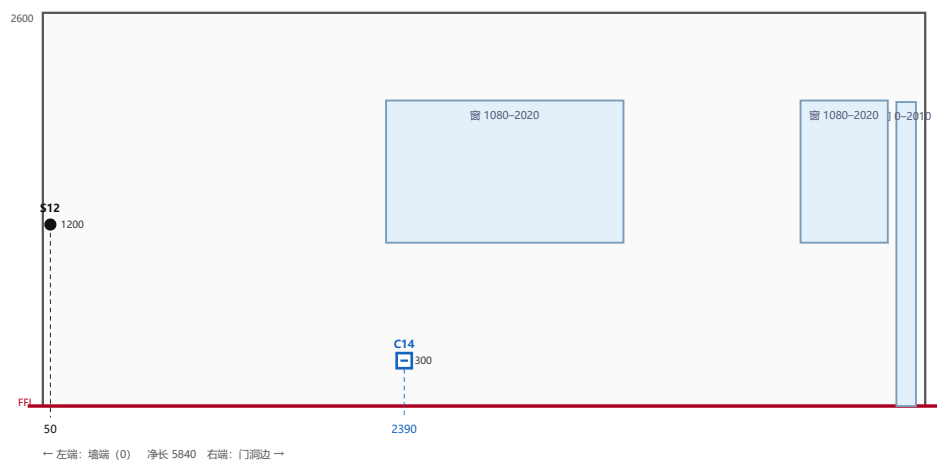


1E06 • 厨房 • 南墙

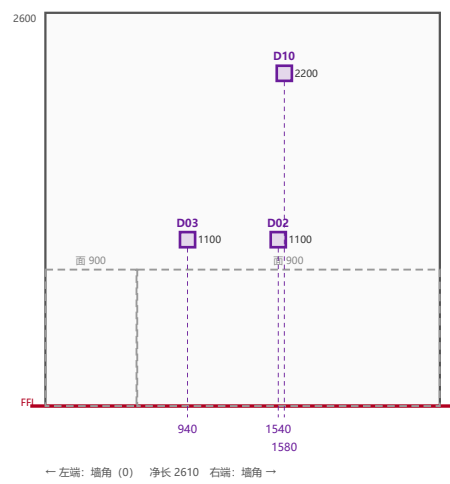

1E07 • 厨房 (吧台区) • 北墙

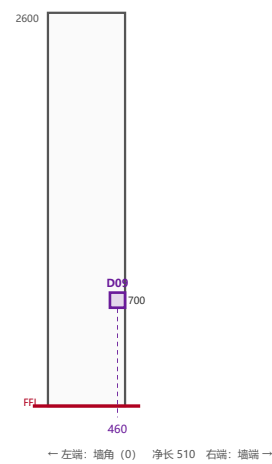


1E08 • 厨房 (吧台区) • 南墙

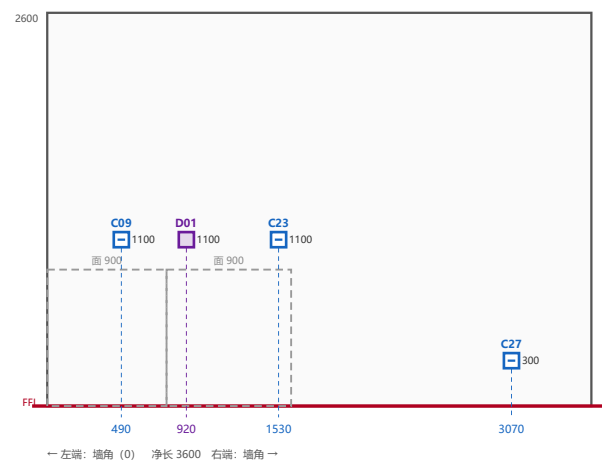


|               |                                     |
|---------------|-------------------------------------|
| 项目 Project    | 27PR 住宅改造 · 27 Penrith Road         |
| 图名 Title      | 一层墙面立面 Wall elevations 1:50         |
| 图号 Sheet      | SO-10 比例 1:50 立面 @A3                |
| 专业 Discipline | 电气定位 Setting out                    |
| 版次 Rev        | A · 2026-10-08 · 施工图 (待持证电工 / 水工复核) |

一层墙面立面 Wall elevations 1:50


1E09 • 厨房（吧台区）• 西墙

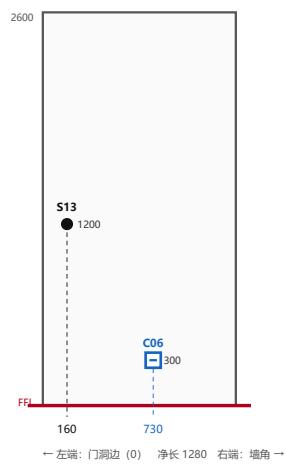


1E10 • G15 区 • 通后花园门旁 • 东墙

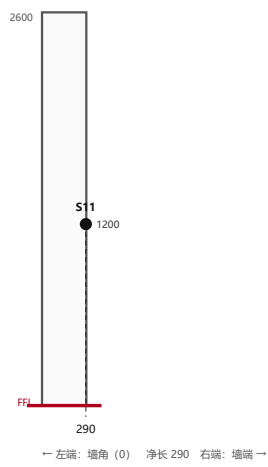


1E11 • 客厅 • 北墙

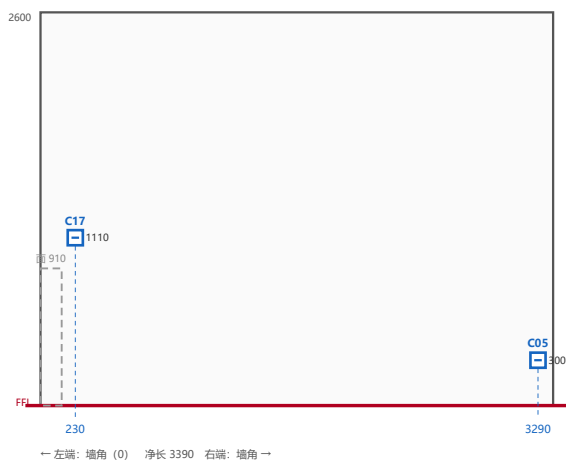


1E12 • 客厅 • 北墙

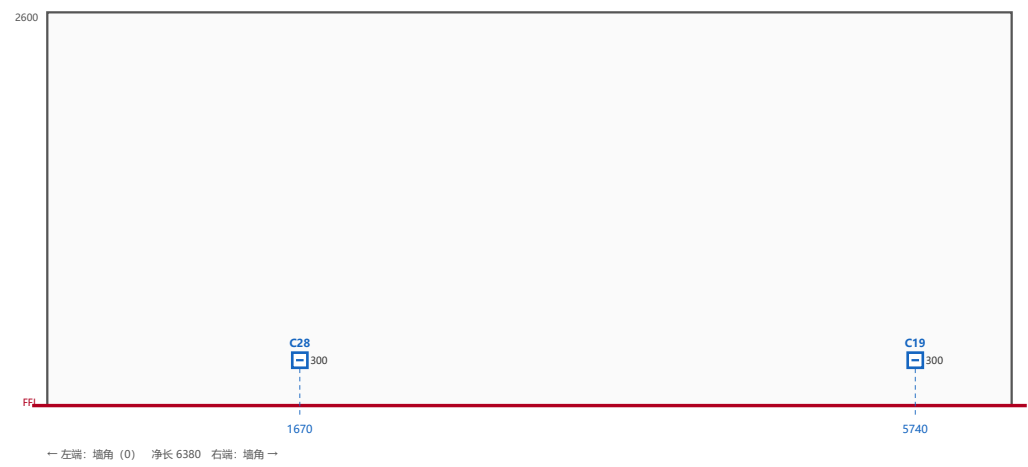


1E13 • 客厅 • 南墙

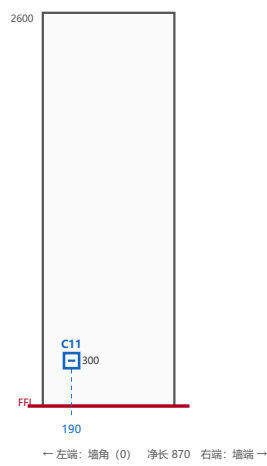


1E14 • 客厅 • 南墙

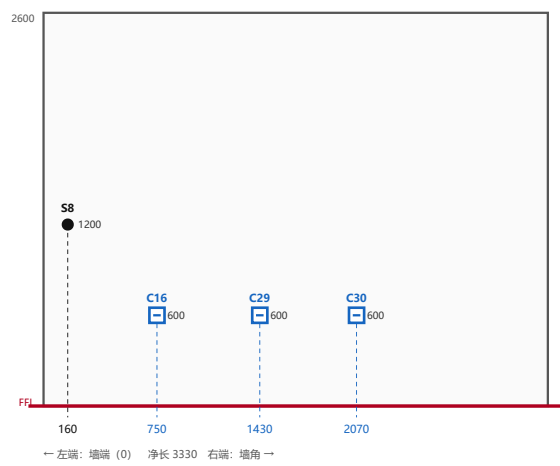

1E15 • 卫生间门外 • 南墙

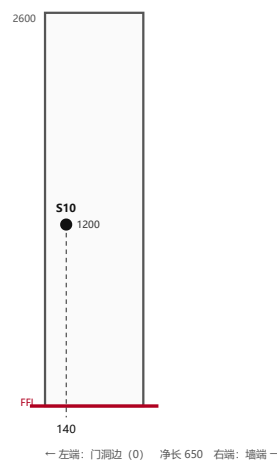


1E16 • 户外 • 东墙

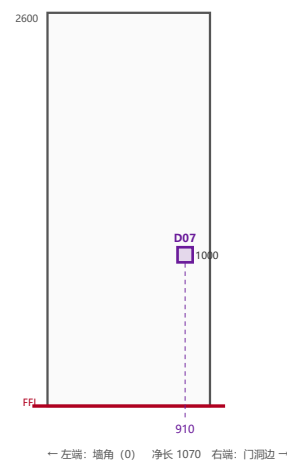


|               |                                     |
|---------------|-------------------------------------|
| 项目 Project    | 27PR 住宅改造 · 27 Penrith Road         |
| 图名 Title      | 一层墙面立面 Wall elevations 1:50         |
| 图号 Sheet      | SO-11 比例 1:50 立面 @A3                |
| 专业 Discipline | 电气定位 Setting out                    |
| 版次 Rev        | A · 2026-10-08 · 施工图 (待持证电工 / 水工复核) |

一层墙面立面 Wall elevations 1:50


1E17 • 户外 • 南墙

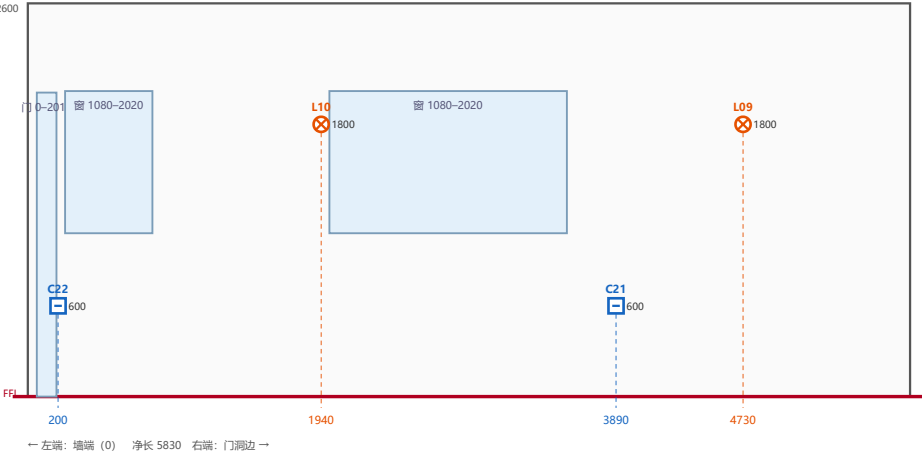


1E18 • 户外 • 西墙

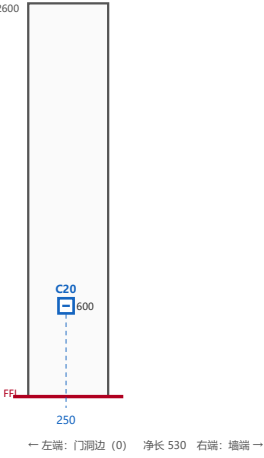


1E19 • 户外 • 西墙

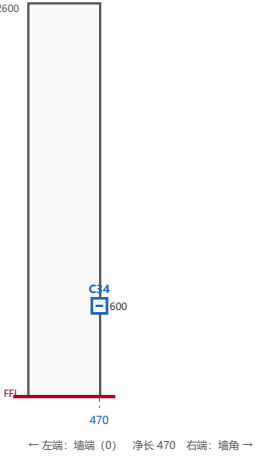


1E20 • 户外 • 西墙

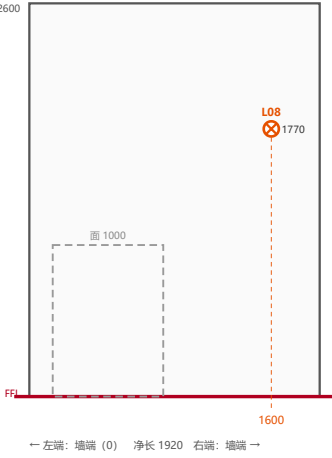


1E21 • 户外 • 西墙

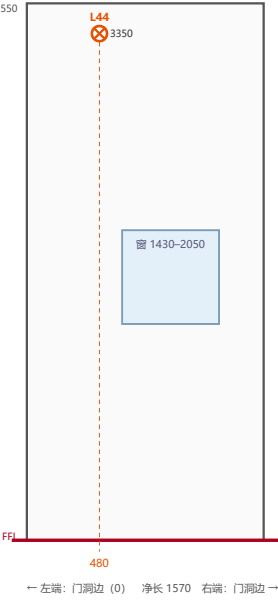


1E22 • 洗衣房 • 东墙

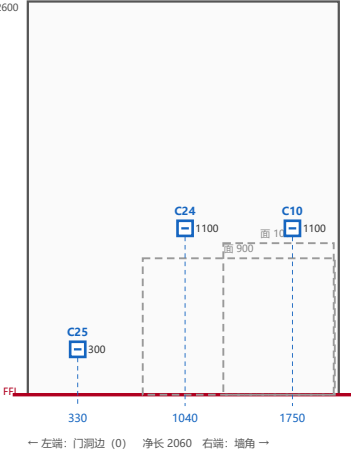


1E23 • 洗衣房 • 东墙

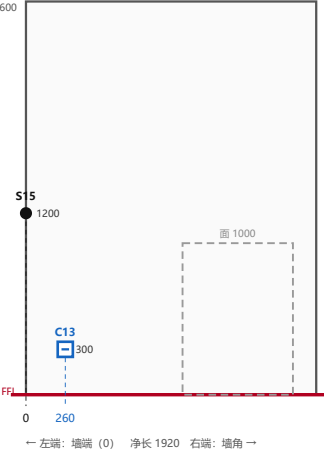


1E24 • 洗衣房 • 南墙

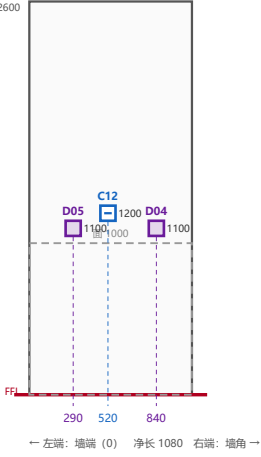

1E25 • 洗衣房门旁 • 西墙

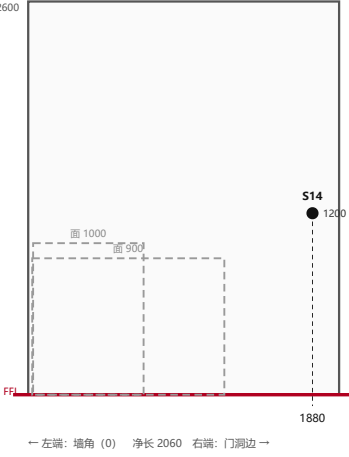


1E26 • 起居室 • 南墙

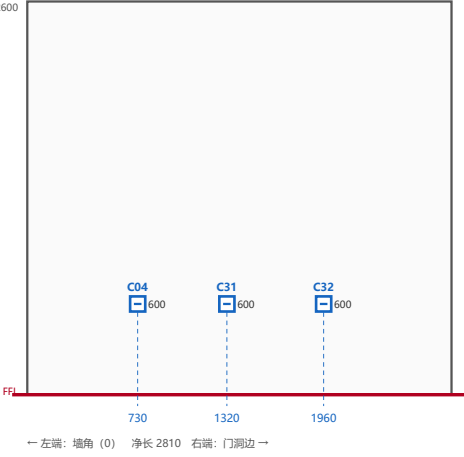


|               |                                     |
|---------------|-------------------------------------|
| 项目 Project    | 27PR 住宅改造 · 27 Penrith Road         |
| 图名 Title      | 一层墙面立面 Wall elevations 1:50         |
| 图号 Sheet      | SO-12 比例 1:50 立面 @A3                |
| 专业 Discipline | 电气定位 Setting out                    |
| 版次 Rev        | A · 2026-10-08 · 施工图 (待持证电工 / 水工复核) |

一层墙面立面 Wall elevations 1:50

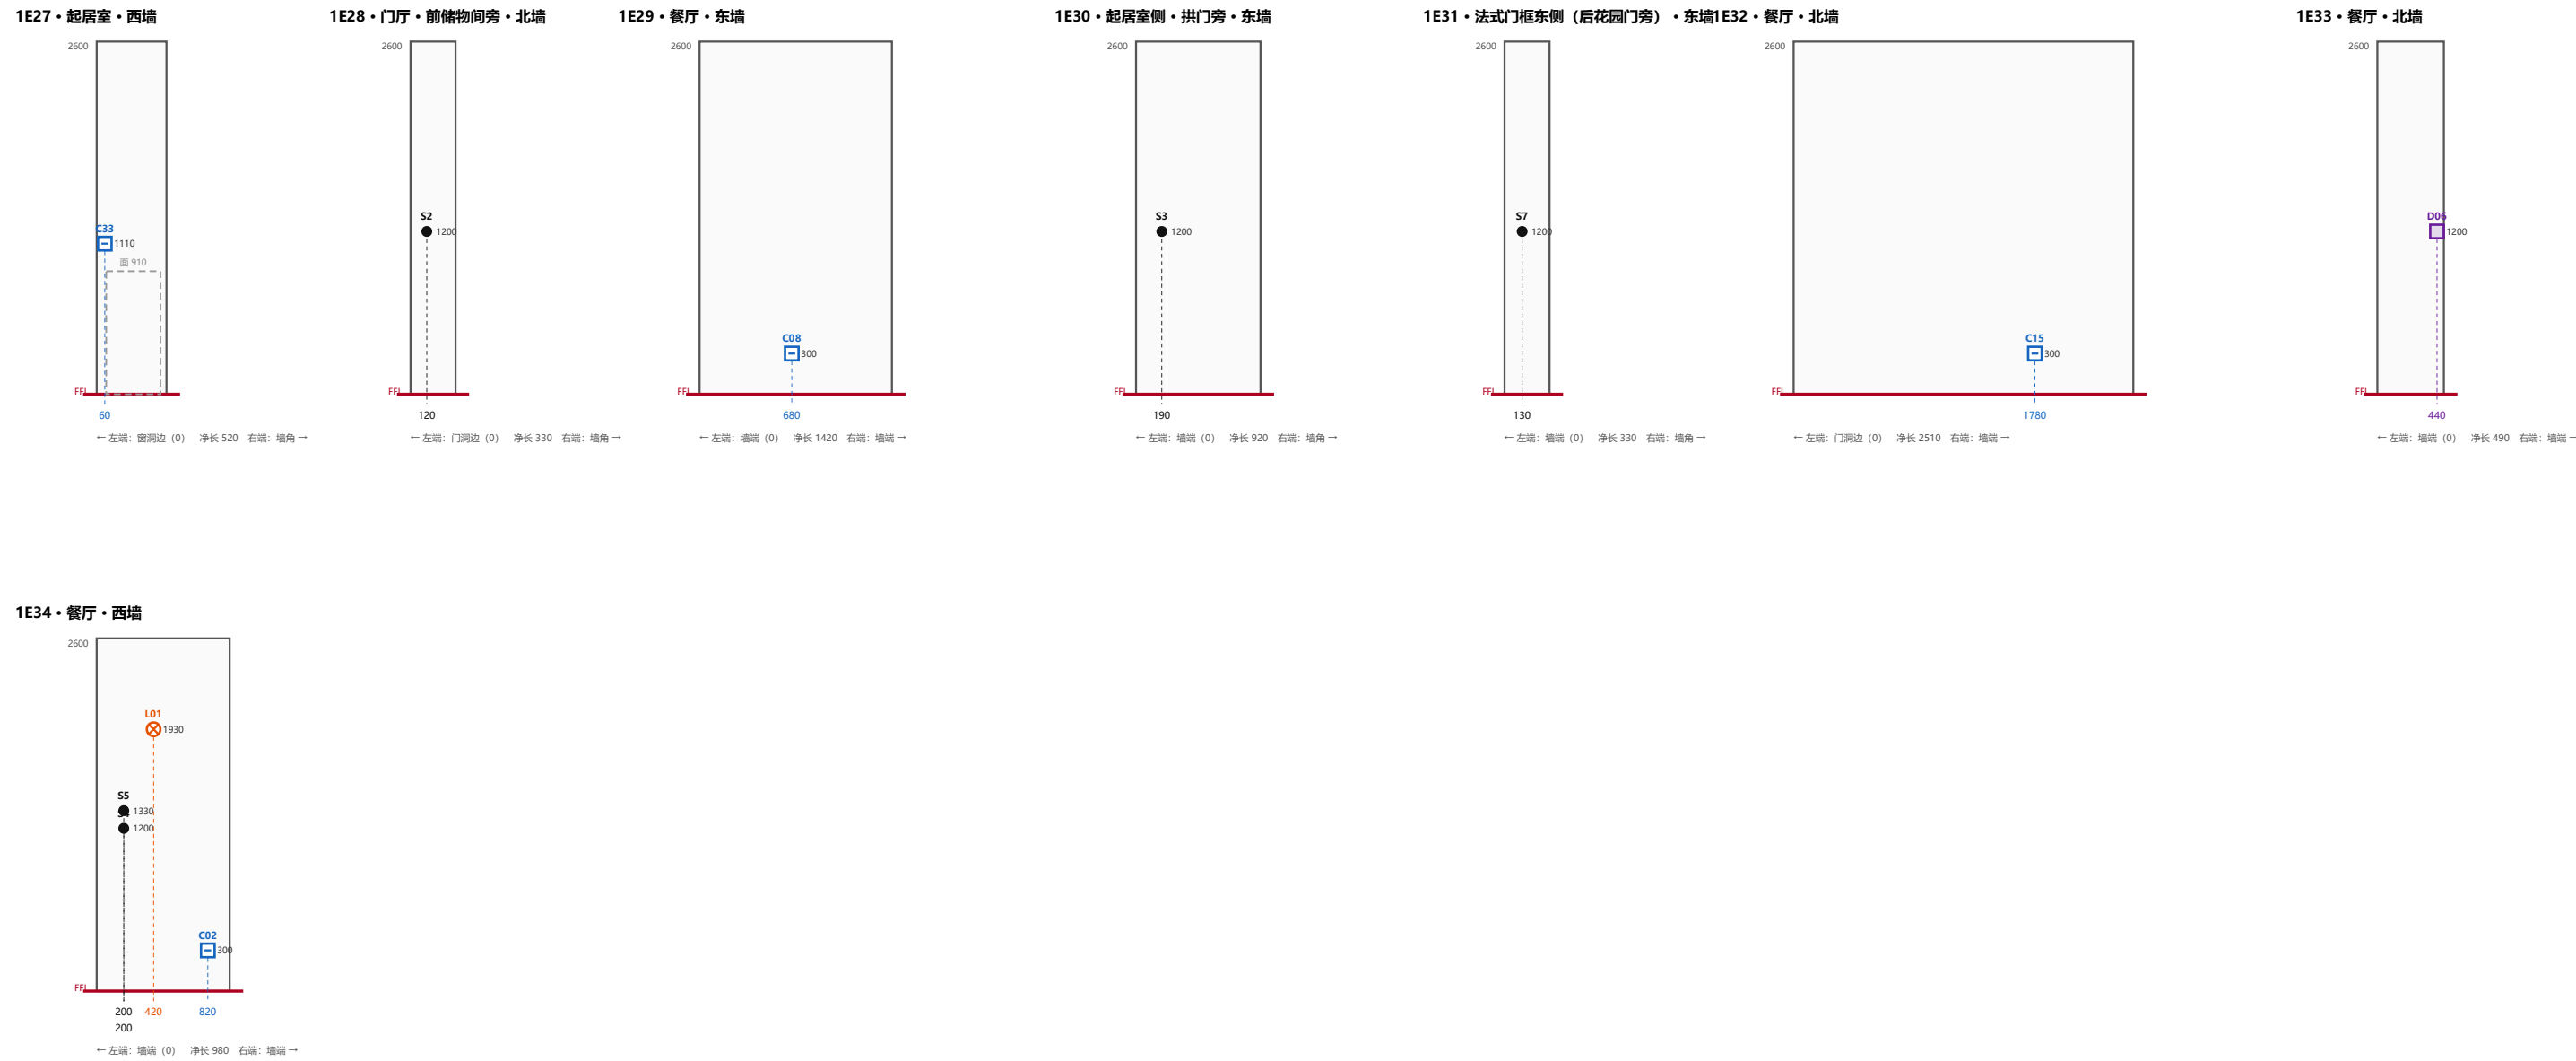

|               |                                     |
|---------------|-------------------------------------|
| 项目 Project    | 27PR 住宅改造 · 27 Penrith Road         |
| 图名 Title      | 一层墙面立面 Wall elevations 1:50         |
| 图号 Sheet      | SO-13 比例 1:50 立面 @A3                |
| 专业 Discipline | 电气定位 Setting out                    |
| 版次 Rev        | A · 2026-10-08 · 施工图 (待持证电工 / 水工复核) |


二层墙面立面 Wall elevations 1:50

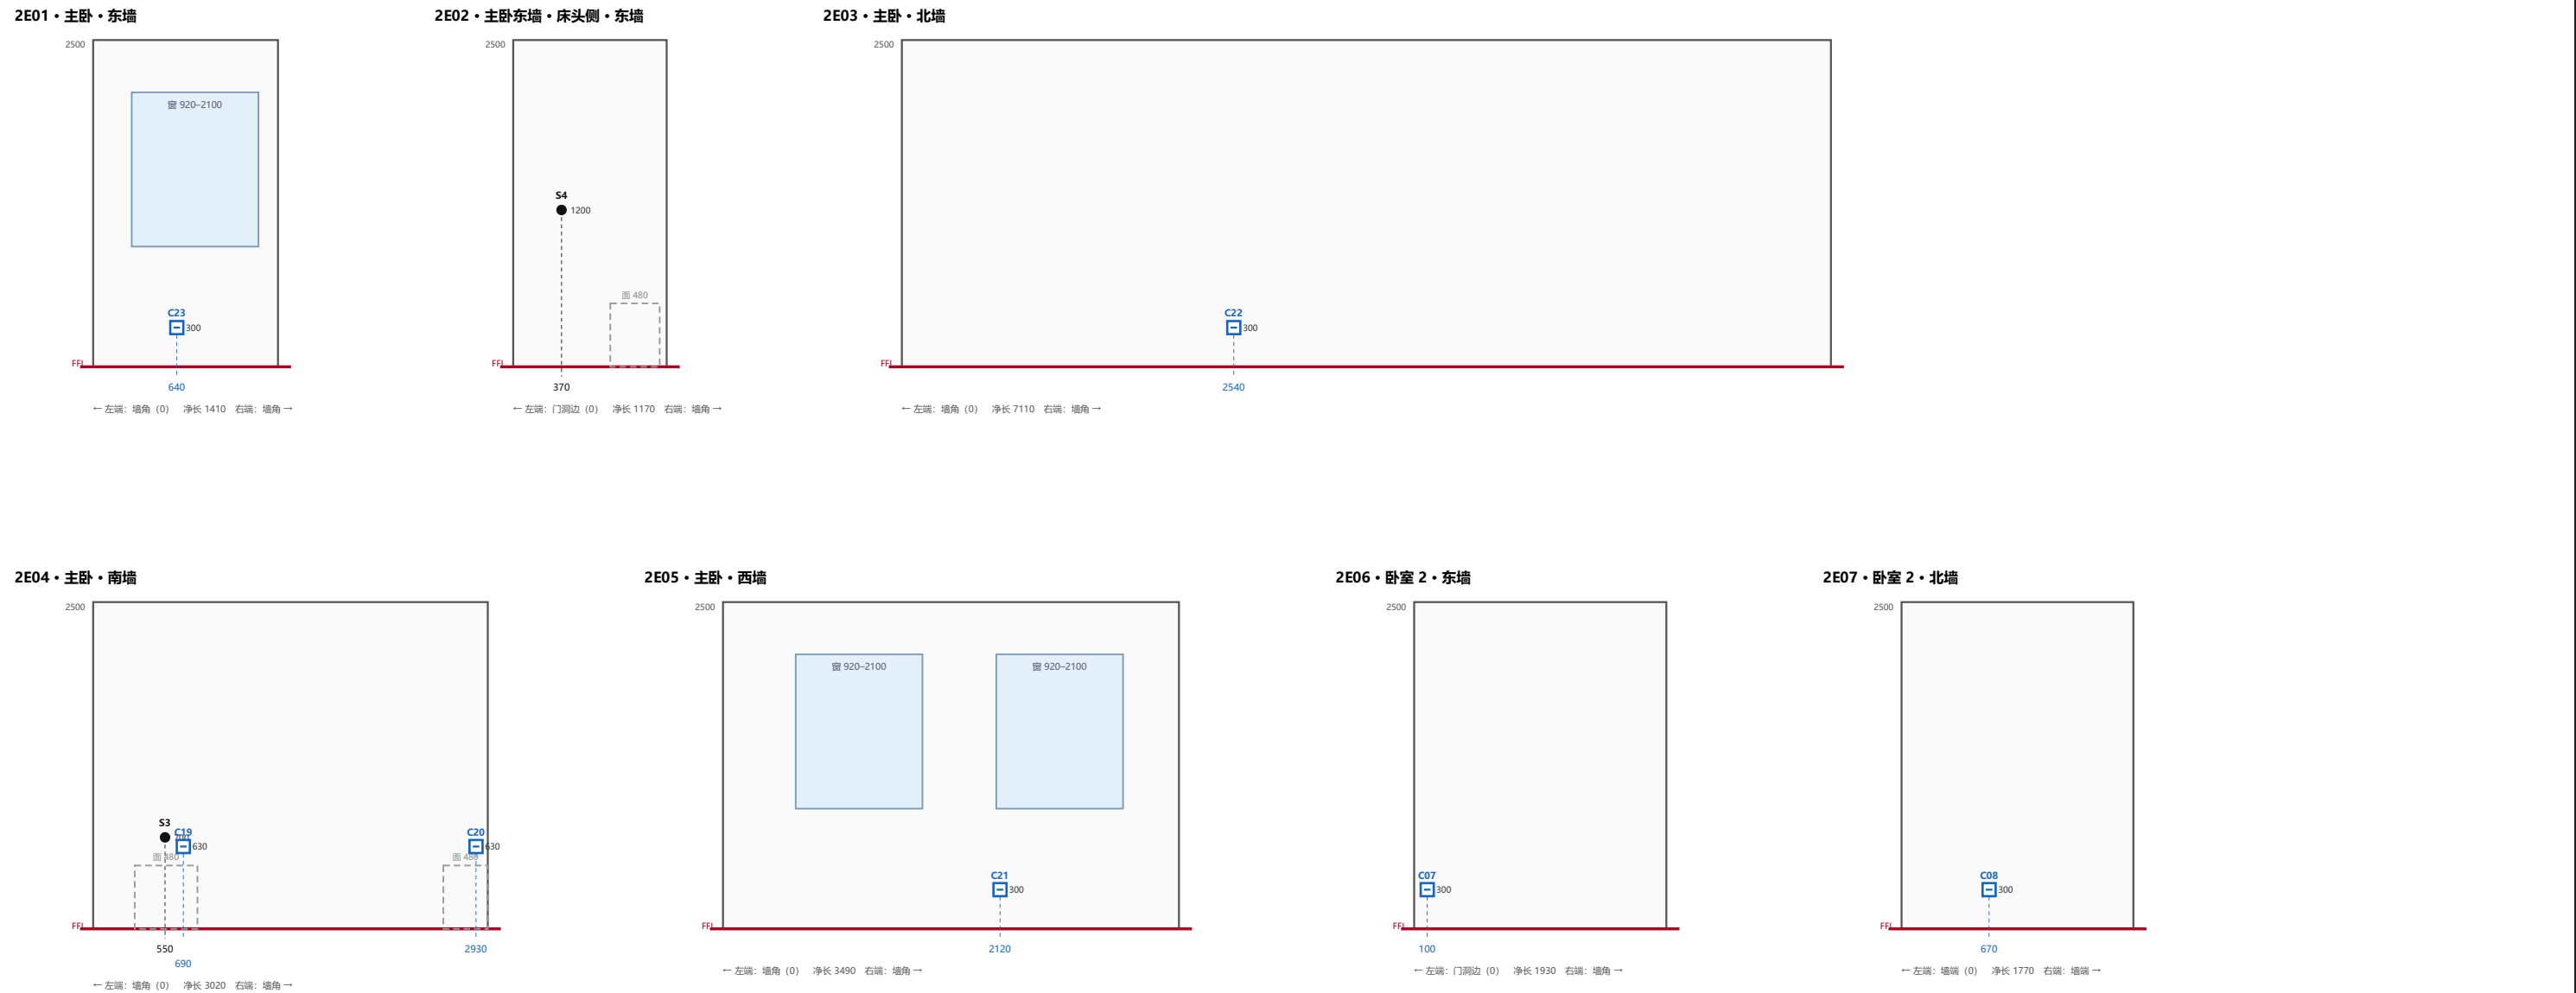


|               |                                     |
|---------------|-------------------------------------|
| 项目 Project    | 27PR 住宅改造 · 27 Penrith Road         |
| 图名 Title      | 二层墙面立面 Wall elevations 1:50         |
| 图号 Sheet      | SO-14 比例 1:50 立面 @A3                |
| 专业 Discipline | 电气定位 Setting out                    |
| 版次 Rev        | A · 2026-10-08 · 施工图 (待持证电工 / 水工复核) |

二层墙面立面 Wall elevations 1:50


2E08 • 卧室 2 • 南墙

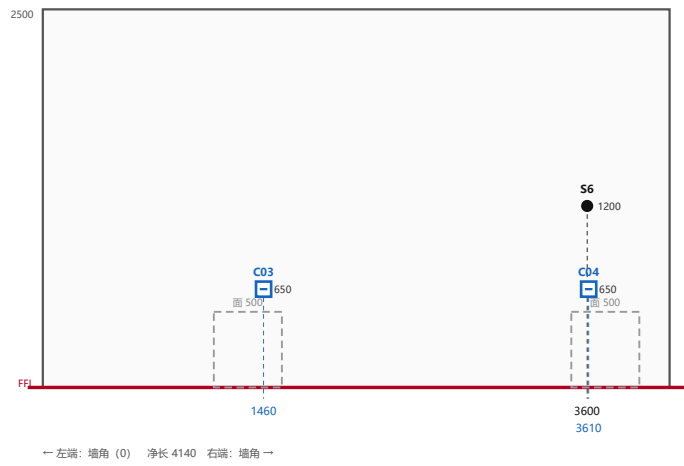


2E09 • 盥洗室门旁 • 西墙

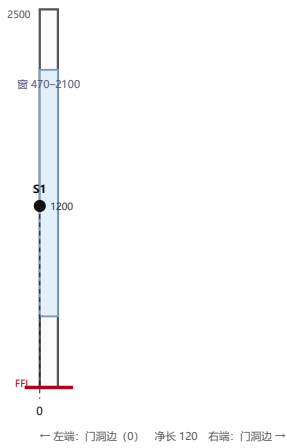


2E10 • 卧室 3 • 东墙

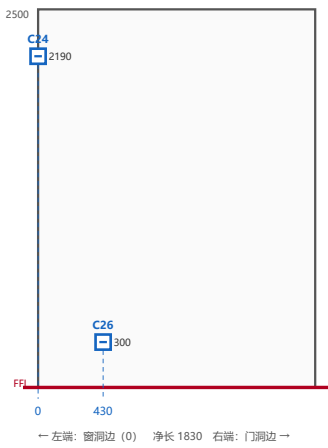


2E11 • 走廊北端 • 东墙

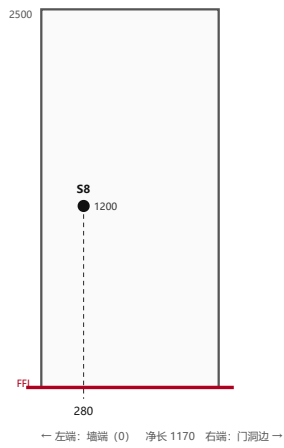


2E12 • 卧室 3 • 北墙

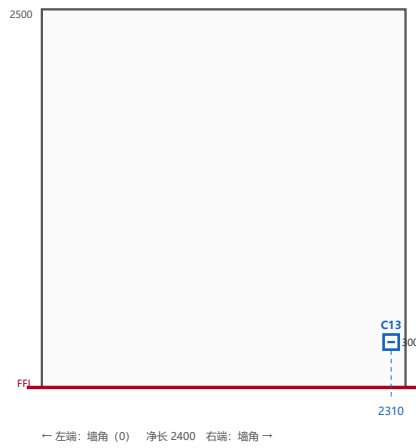


2E13 • 卧室 3 • 南墙

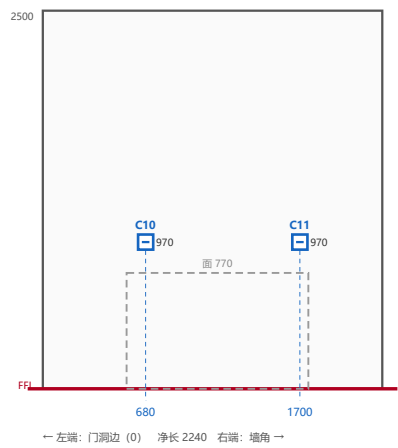


2E14 • 卧室 3 • 西墙

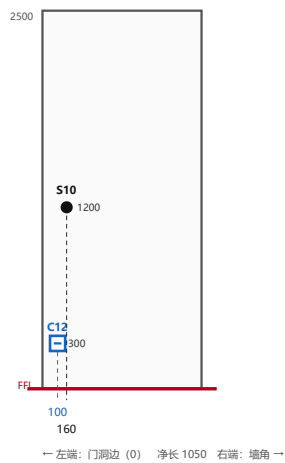


2E15 • 卧室 4 内 • 卫生间门南侧 (隔墙短墙) • 东墙

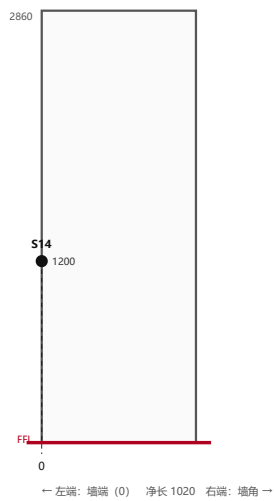


2E16 • 卧室 4 • 北墙

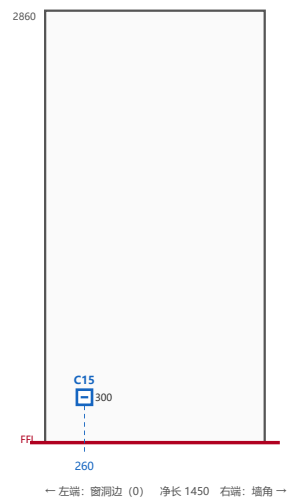

2E17 • 卧室 4 • 北墙

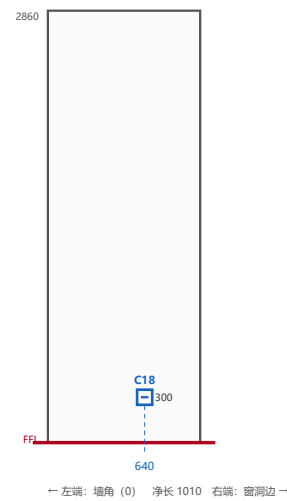


2E18 • 卧室 4 • 南墙

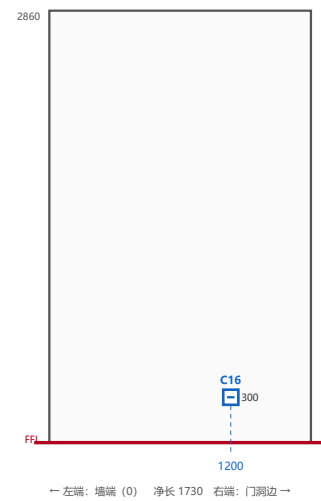


|               |                                     |
|---------------|-------------------------------------|
| 项目 Project    | 27PR 住宅改造 · 27 Penrith Road         |
| 图名 Title      | 二层墙面立面 Wall elevations 1:50         |
| 图号 Sheet      | SO-15 比例 1:50 立面 @A3                |
| 专业 Discipline | 电气定位 Setting out                    |
| 版次 Rev        | A · 2026-10-08 · 施工图 (待持证电工 / 水工复核) |

二层墙面立面 Wall elevations 1:50


2E19 • 卧室 4 • 西墙

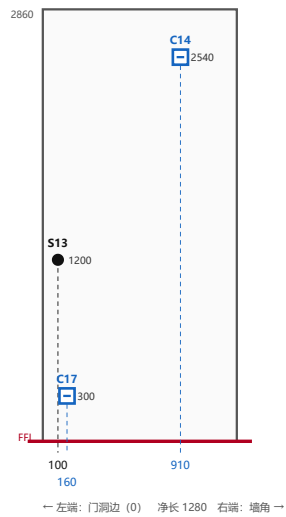


2E20 • 卫生间 • 东墙

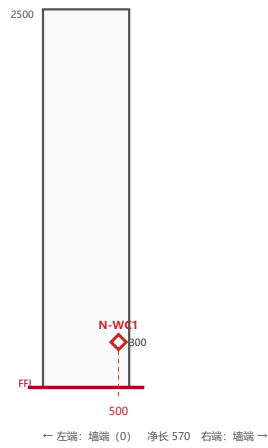


2E21 • 卫生间 • 东墙

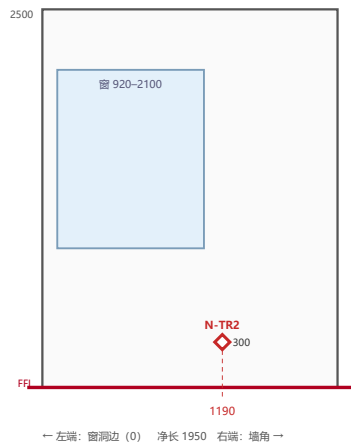


2E22 • 卫生间 • 南墙

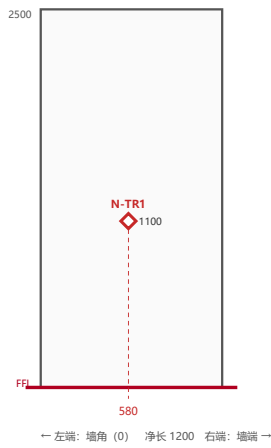


2E23 • 北卫生间门外 • 西墙

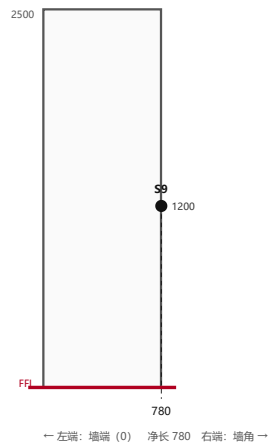


2E24 • 走廊南端 • 楼梯口 • 北墙

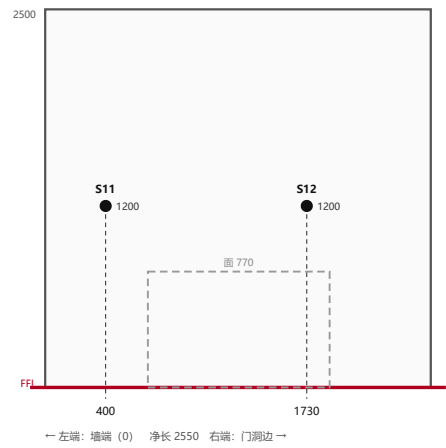


2E25 • 楼梯 • 南墙

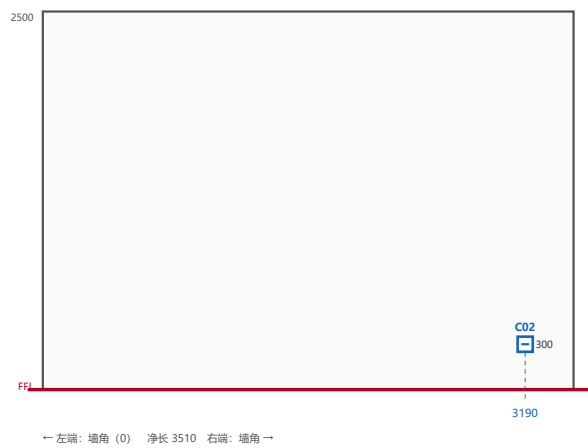


2E26 • 电梯 • 东墙

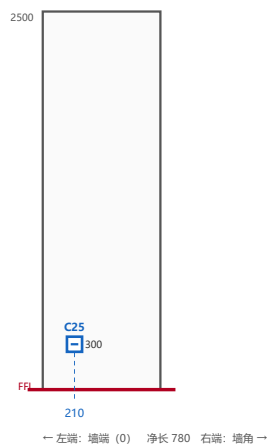


2E27 • 西卫生间门外 • 东墙

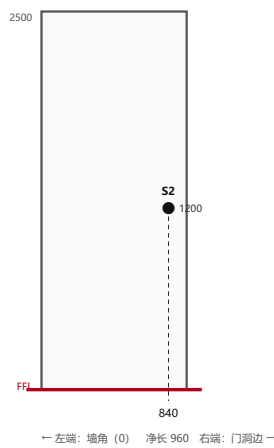


2E28 • 盥洗室 • 南墙

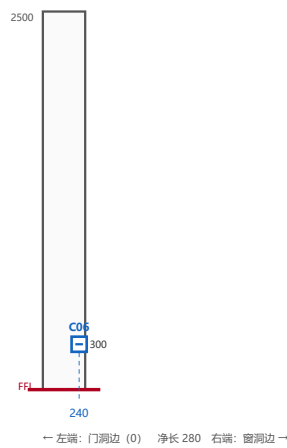

2E29 • 盥洗室 • 西墙

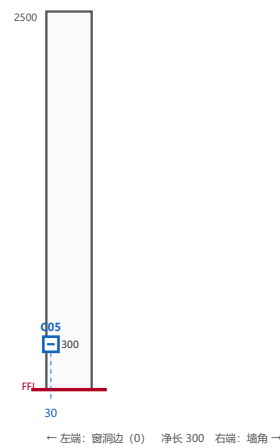


2E30 • 衣帽间 • 东墙

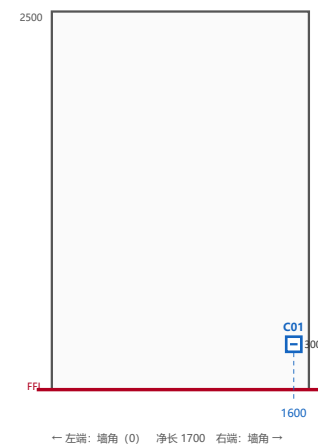


|               |                                     |
|---------------|-------------------------------------|
| 项目 Project    | 27PR 住宅改造 · 27 Penrith Road         |
| 图名 Title      | 二层墙面立面 Wall elevations 1:50         |
| 图号 Sheet      | SO-16 比例 1:50 立面 @A3                |
| 专业 Discipline | 电气定位 Setting out                    |
| 版次 Rev        | A · 2026-10-08 · 施工图 (待持证电工 / 水工复核) |

二层墙面立面 Wall elevations 1:50


2E31 · 衣帽间 · 北墙

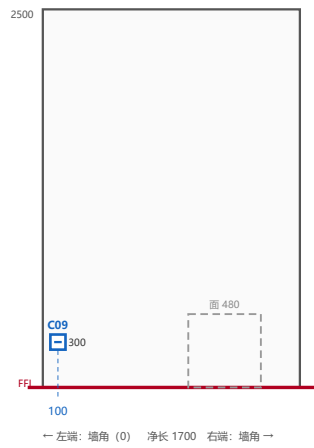

2E32 · 衣帽间门旁 · 北墙

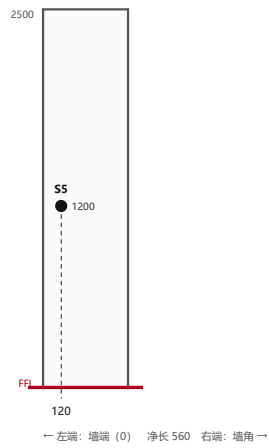

2E33 · 卧室2 门旁 (门西侧短墙, 卧室2 一侧, 锁侧) · 东墙

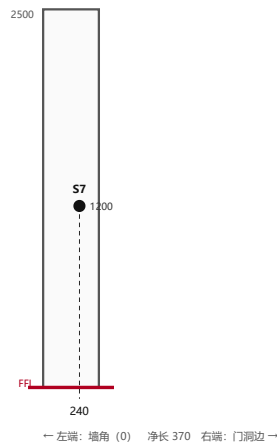

|               |                                     |
|---------------|-------------------------------------|
| 项目 Project    | 27PR 住宅改造 · 27 Penrith Road         |
| 图名 Title      | 二层墙面立面 Wall elevations 1:50         |
| 图号 Sheet      | SO-17 比例 1:50 立面 @A3                |
| 专业 Discipline | 电气定位 Setting out                    |
| 版次 Rev        | A · 2026-10-08 · 施工图 (待持证电工 / 水工复核) |